



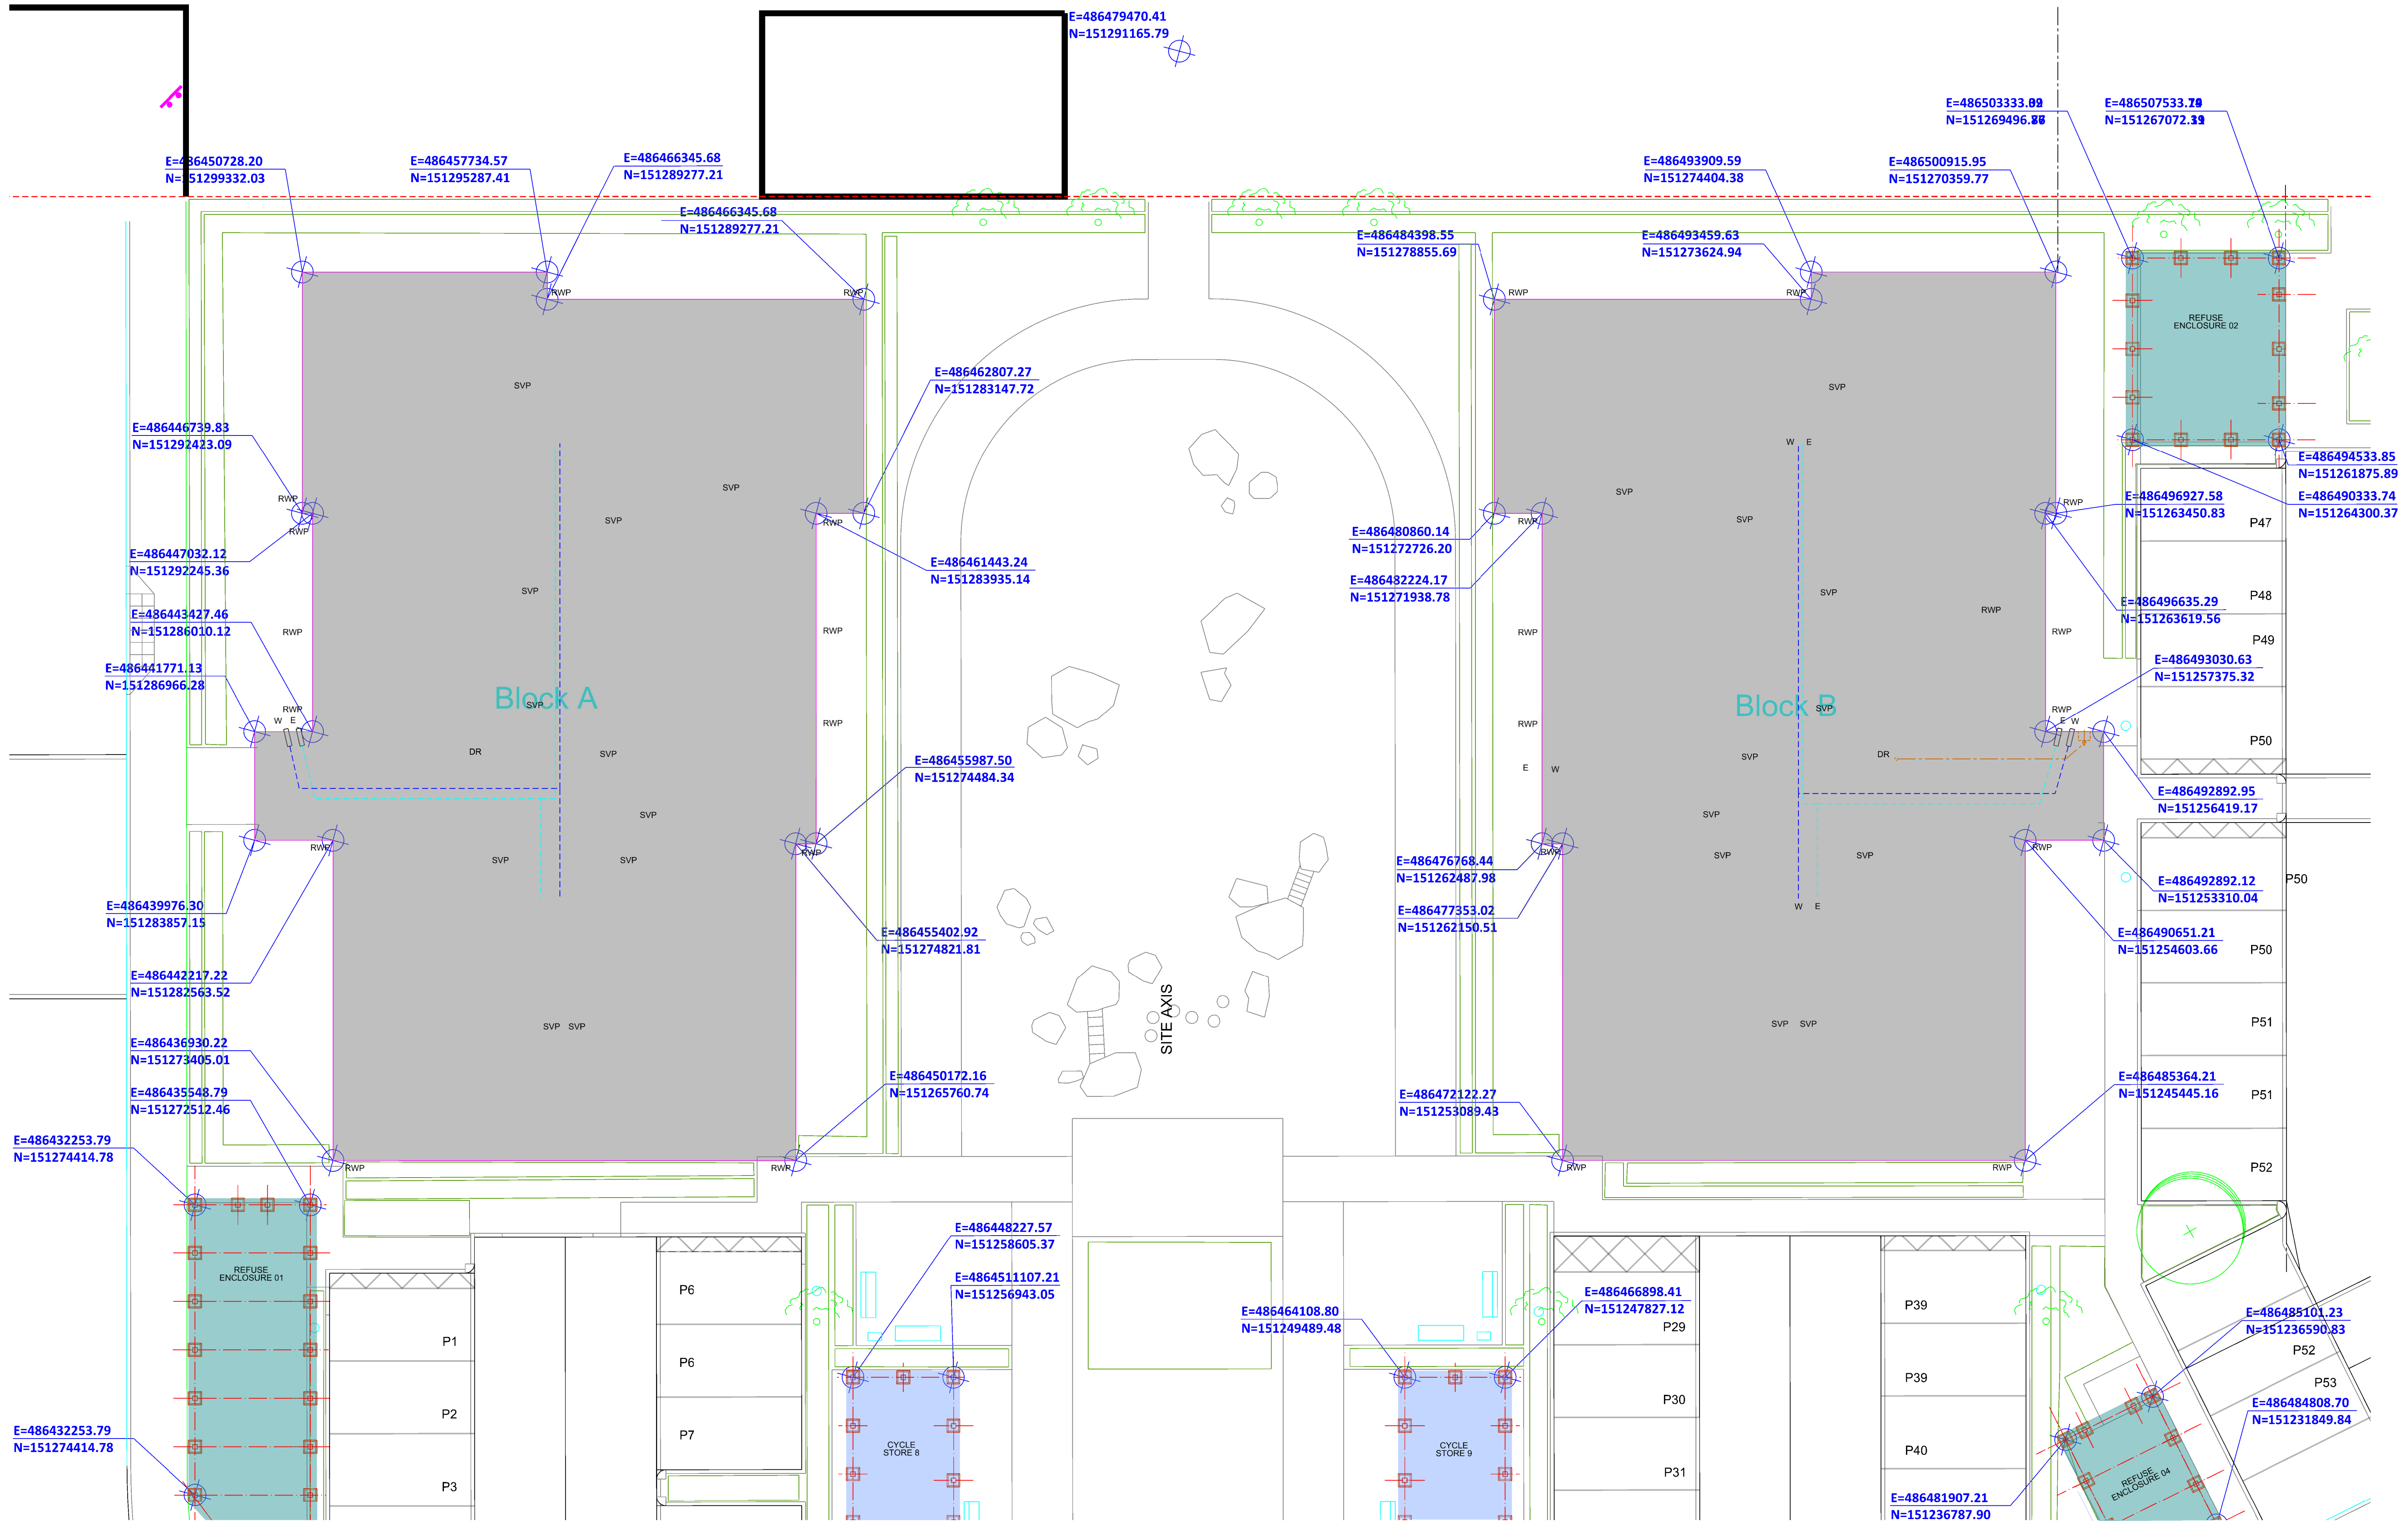

NOTES
Do not scale this drawing - use figured dimensions only.
All dimensions are to be checked before implementation.
Any discrepancies are to be advised immediately.
All information is copyright of DLA Architects Practice and may not be used or reproduced without prior permission.

REVISIONS
C1 27.03.2018 CONSTRUCTION ISSUE, - Bin & cycle store revised and set out

CYCLE PARKING
REFUSE AREA

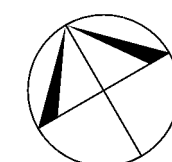

GUNHILL DEVELOPMENT ZONE
GRAINGER PLC
SITE LAYOUT- BLOCK A & B SETTING OUT
DATE AUG 2017
DRAWING NUMBER 1132-04
SCALE 1:100 @ A1
REVISION C1
STATUS CONSTRUCTION

DLA ARCHITECTS PRACTICE
INTEGRATED ARCHITECTURE
50 North Thirteenth Street
CENTRAL MILTON KEYNES, MK9 3BP
T: 01908 259719 F: 01908 605747
email: mail@dla-architects.com
© DLA ARCHITECTS PRACTICE LTD