



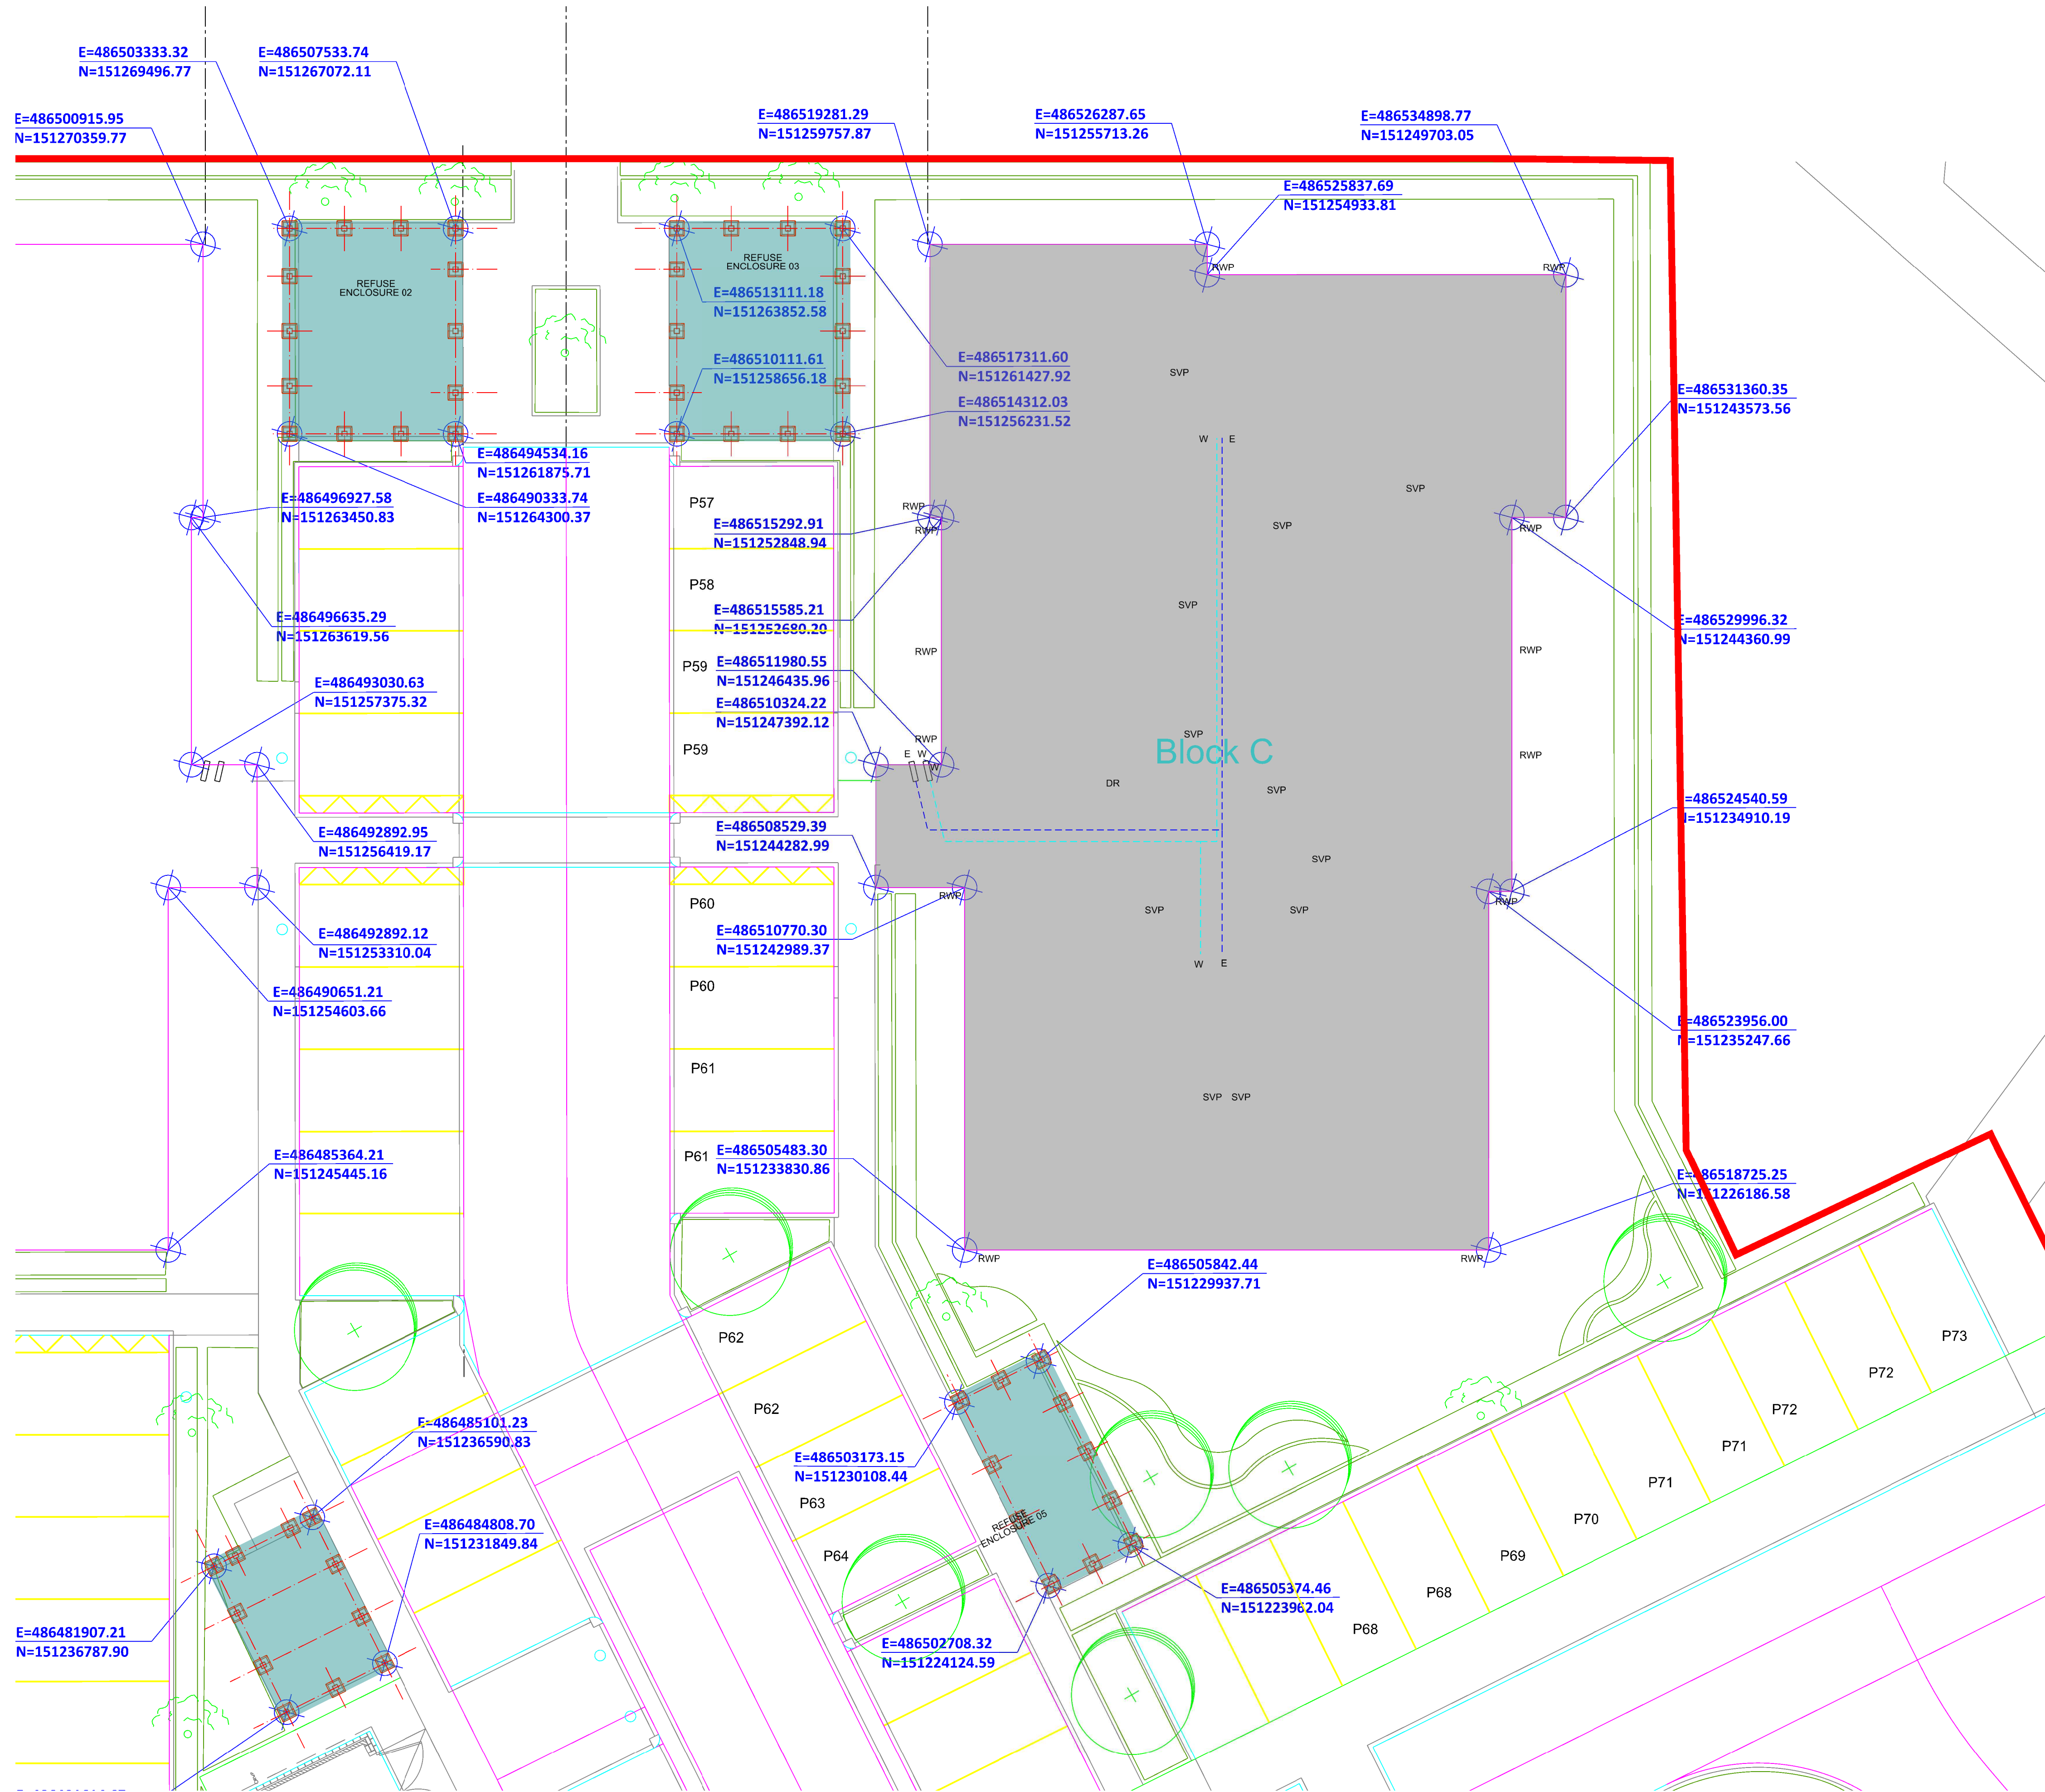

NOTES
Do not scale this drawing -
use figured dimensions only.
All dimensions are to be
checked before implementation.
Any discrepancies are to
be advised immediately.
All information is copyright of
DLA Architects Practice and
may not be used or reproduced
without prior permission.

REVISIONS
C1 27.03.2018 CONSTRUCTION ISSUE - Bin & cycle stores revised and set out

CYCLE PARKING
REFUSE AREA

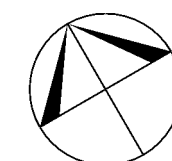

GUNHILL DEVELOPMENT ZONE
GRAINGER PLC
SITE LAYOUT- BLOCK C SETTING OUT
DATE: SEPT 2017
DRAWING NUMBER: 1132-05
SCALE: 1:100 @ A1
REVISION: C1
STATUS: CONSTRUCTION

DLA ARCHITECTS PRACTICE
INTEGRATED ARCHITECTURE
50 North Thirteenth Street
CENTRAL MILTON KEYNES, MK9 3BP
T: 01908 259719 F: 01908 605747
email: mail@dla-architects.com
© DLA ARCHITECTS PRACTICE LTD