




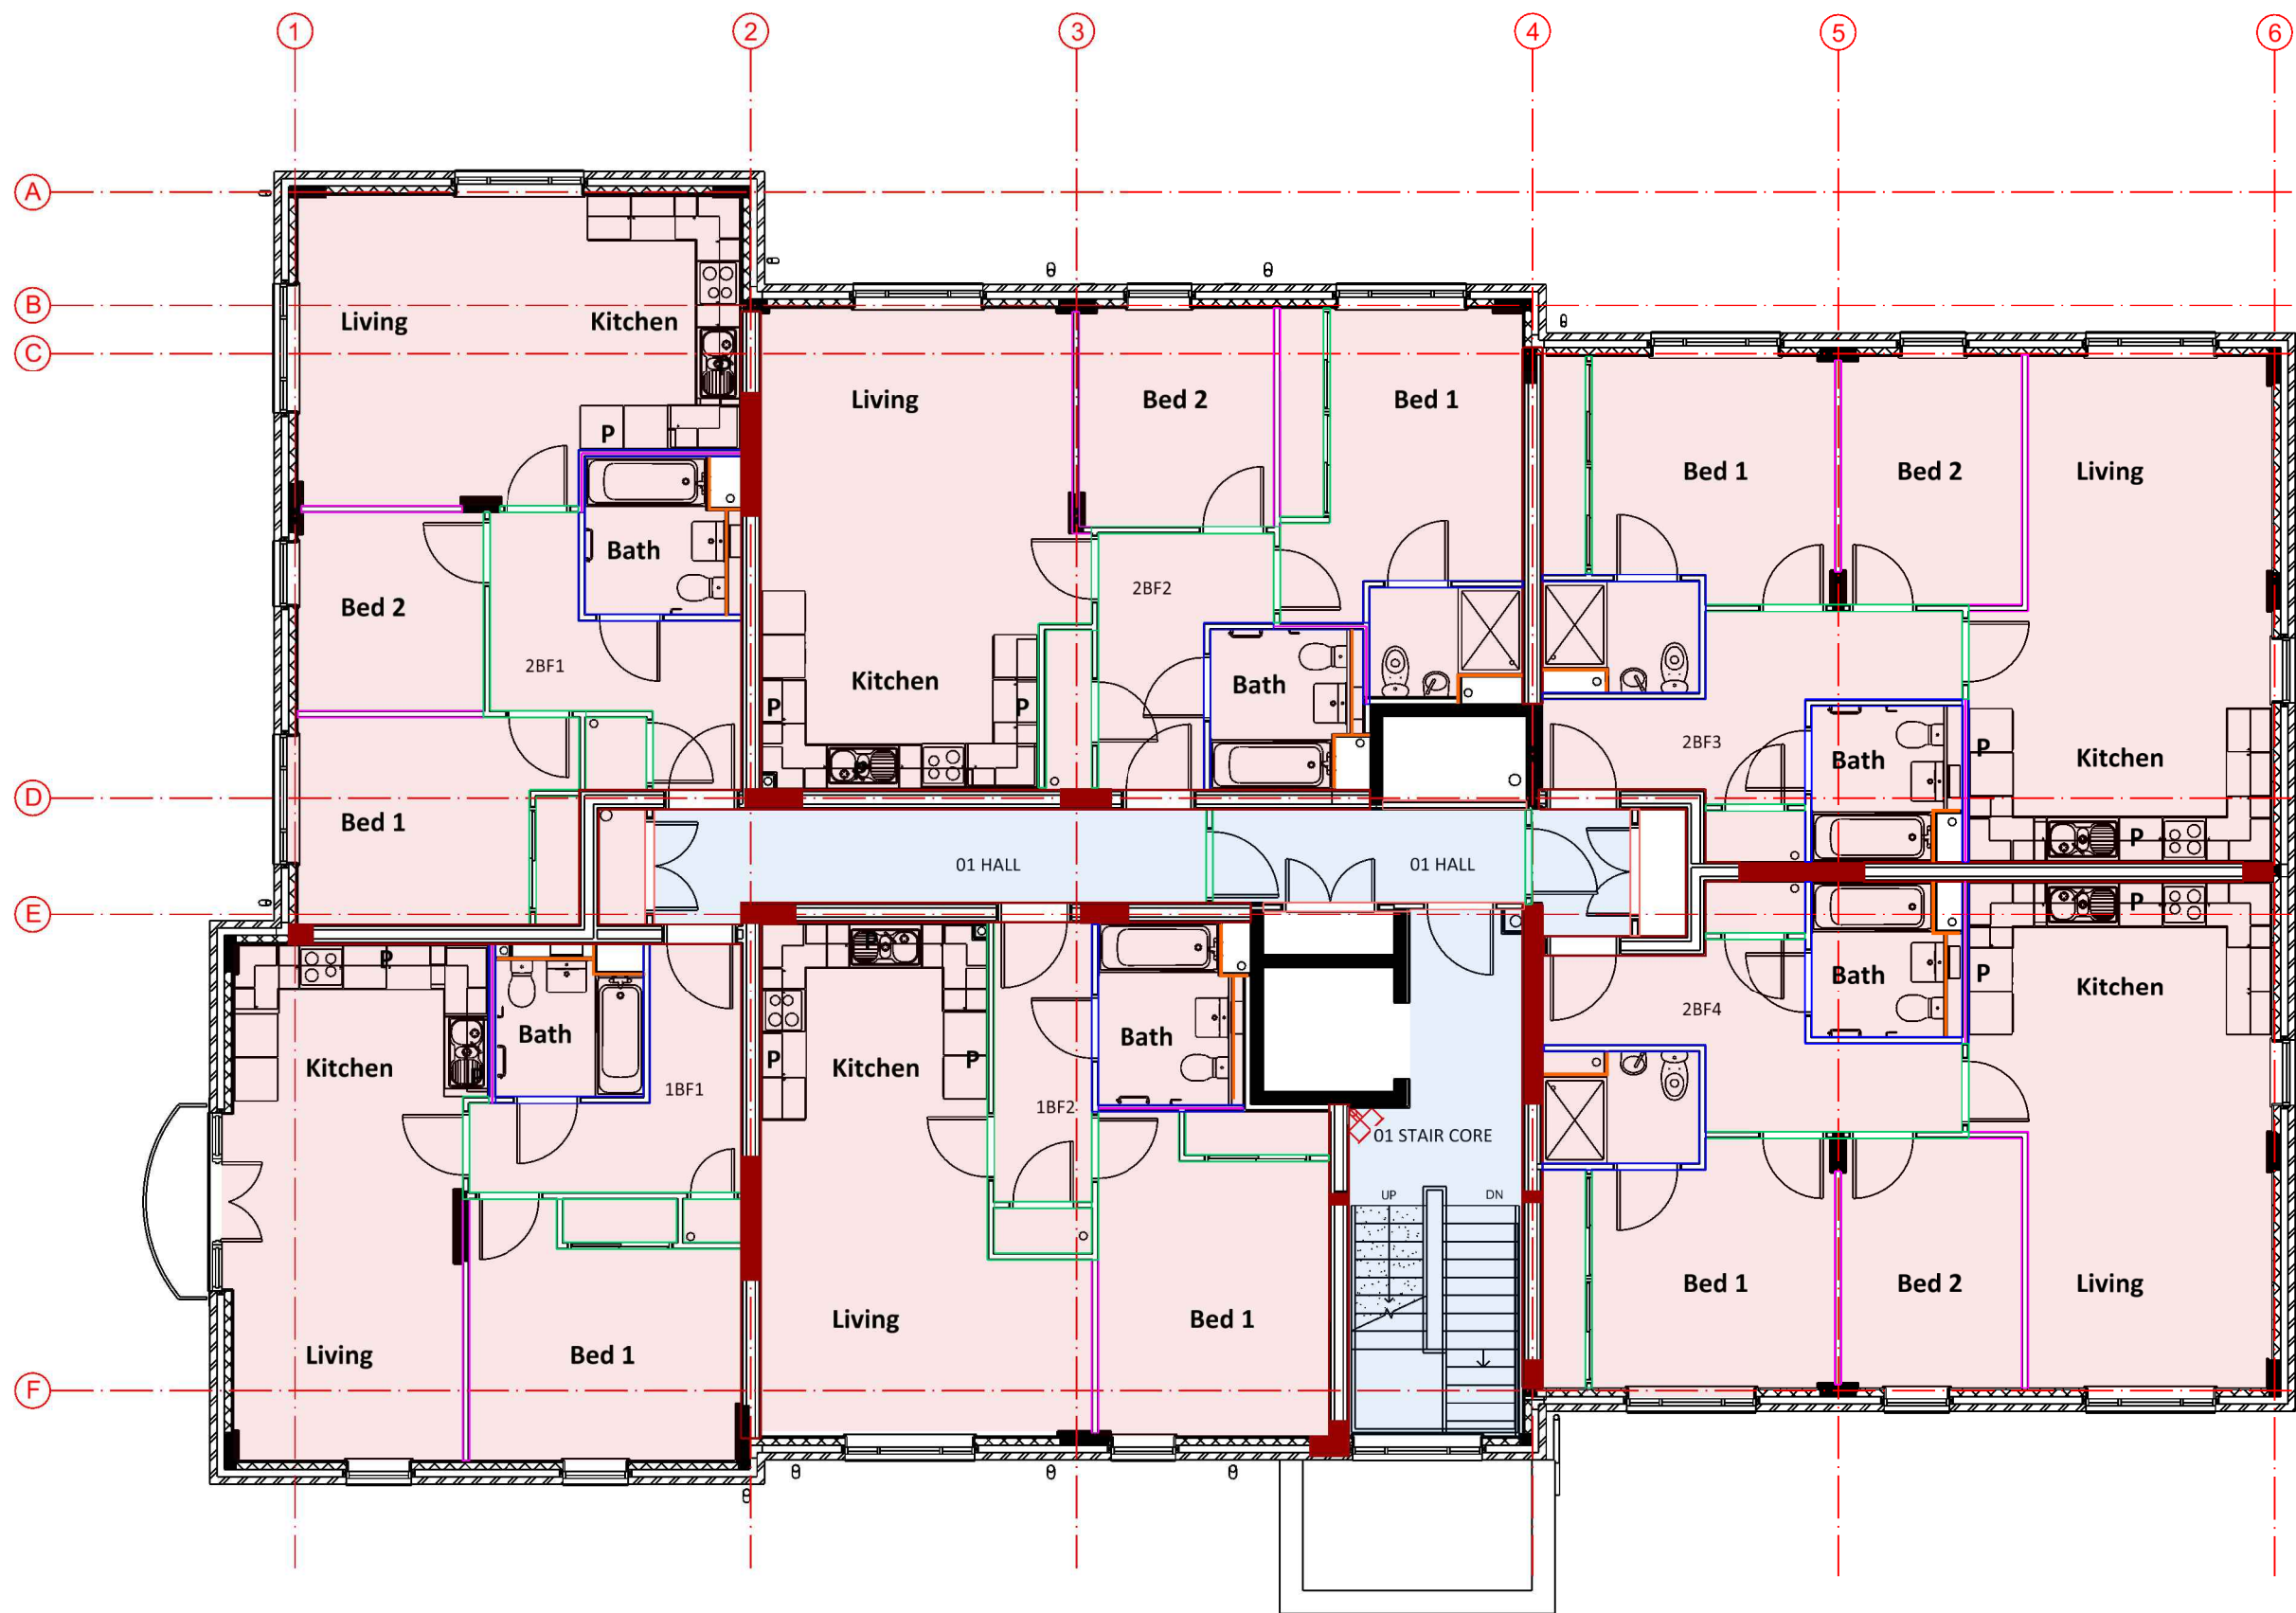


Proposed First/Second/Third Floor Plan

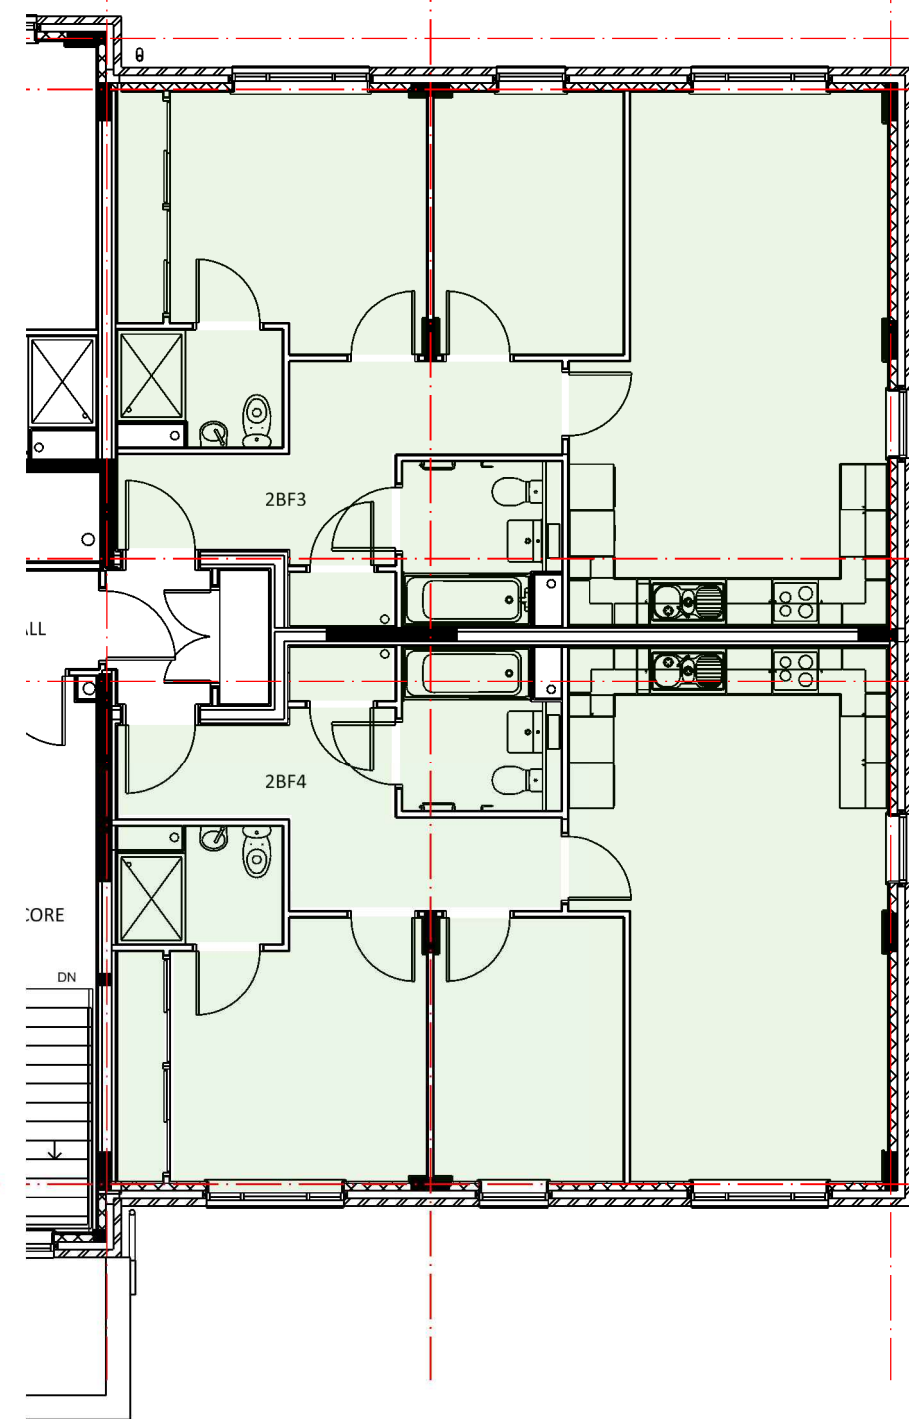

Top Floor 2BF3 & 2BF4
All walls as lower floors ceiling to be 30 minute fire rated

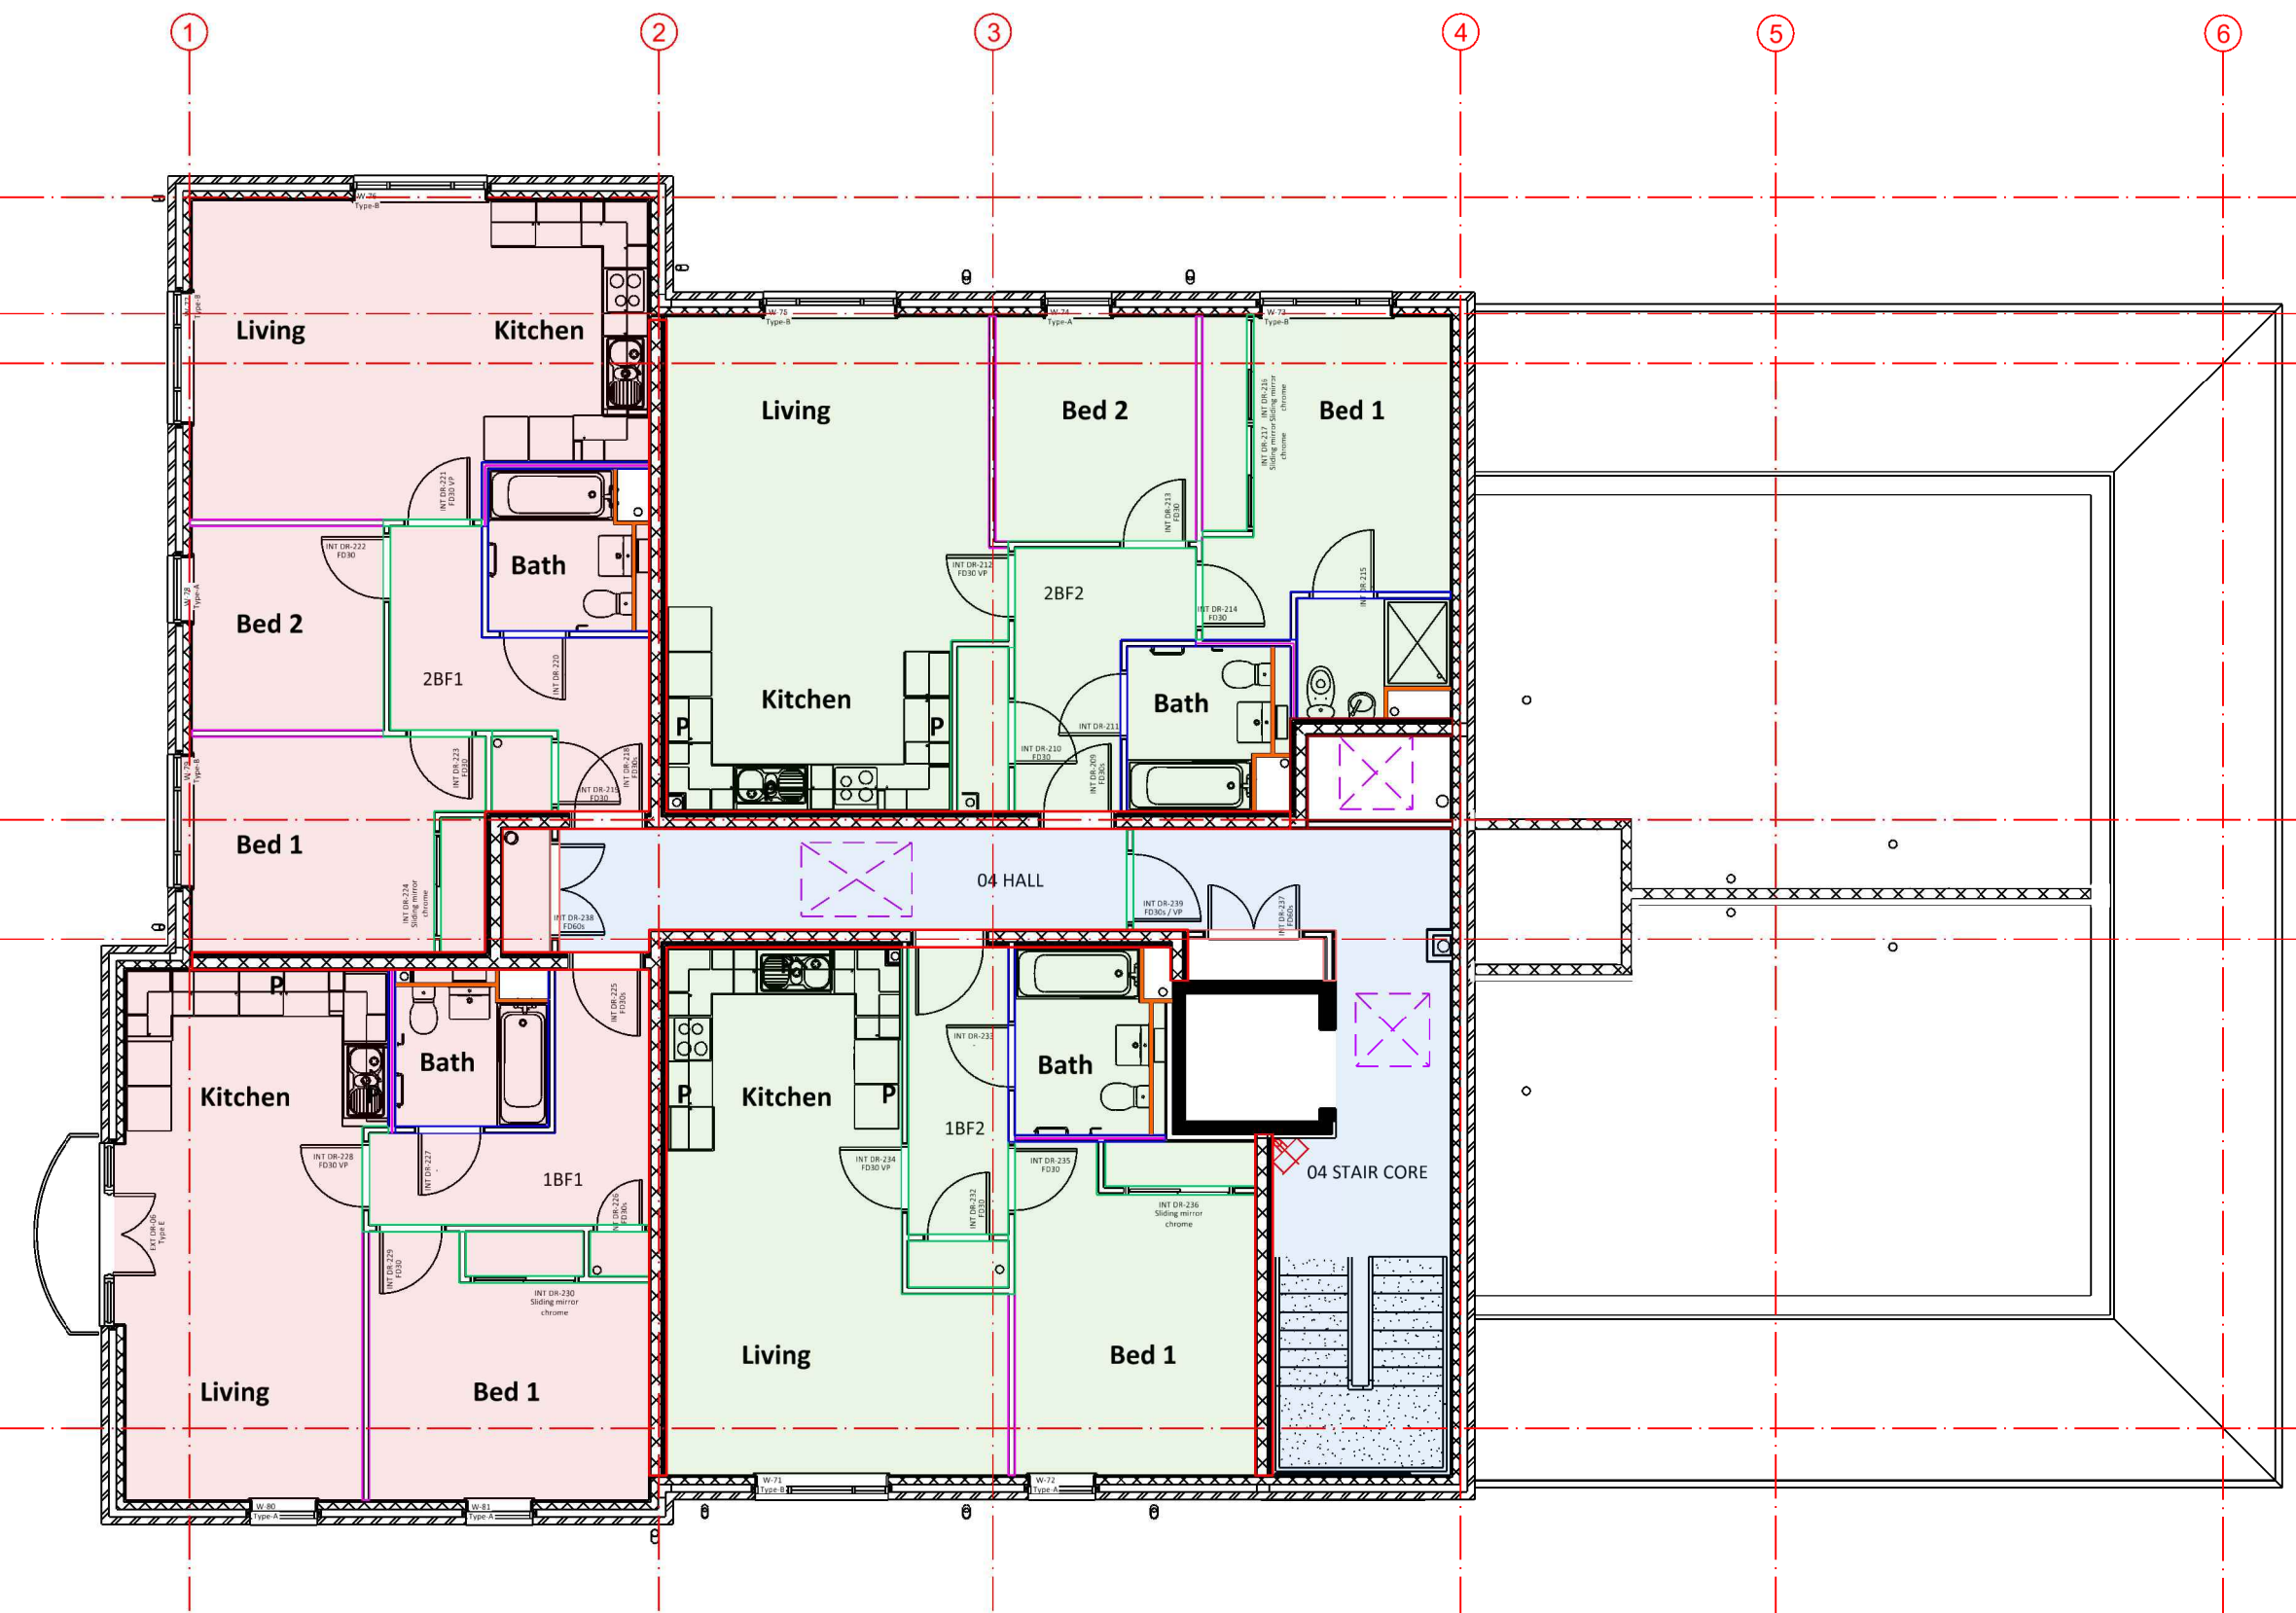

Proposed Fourth Floor Plan

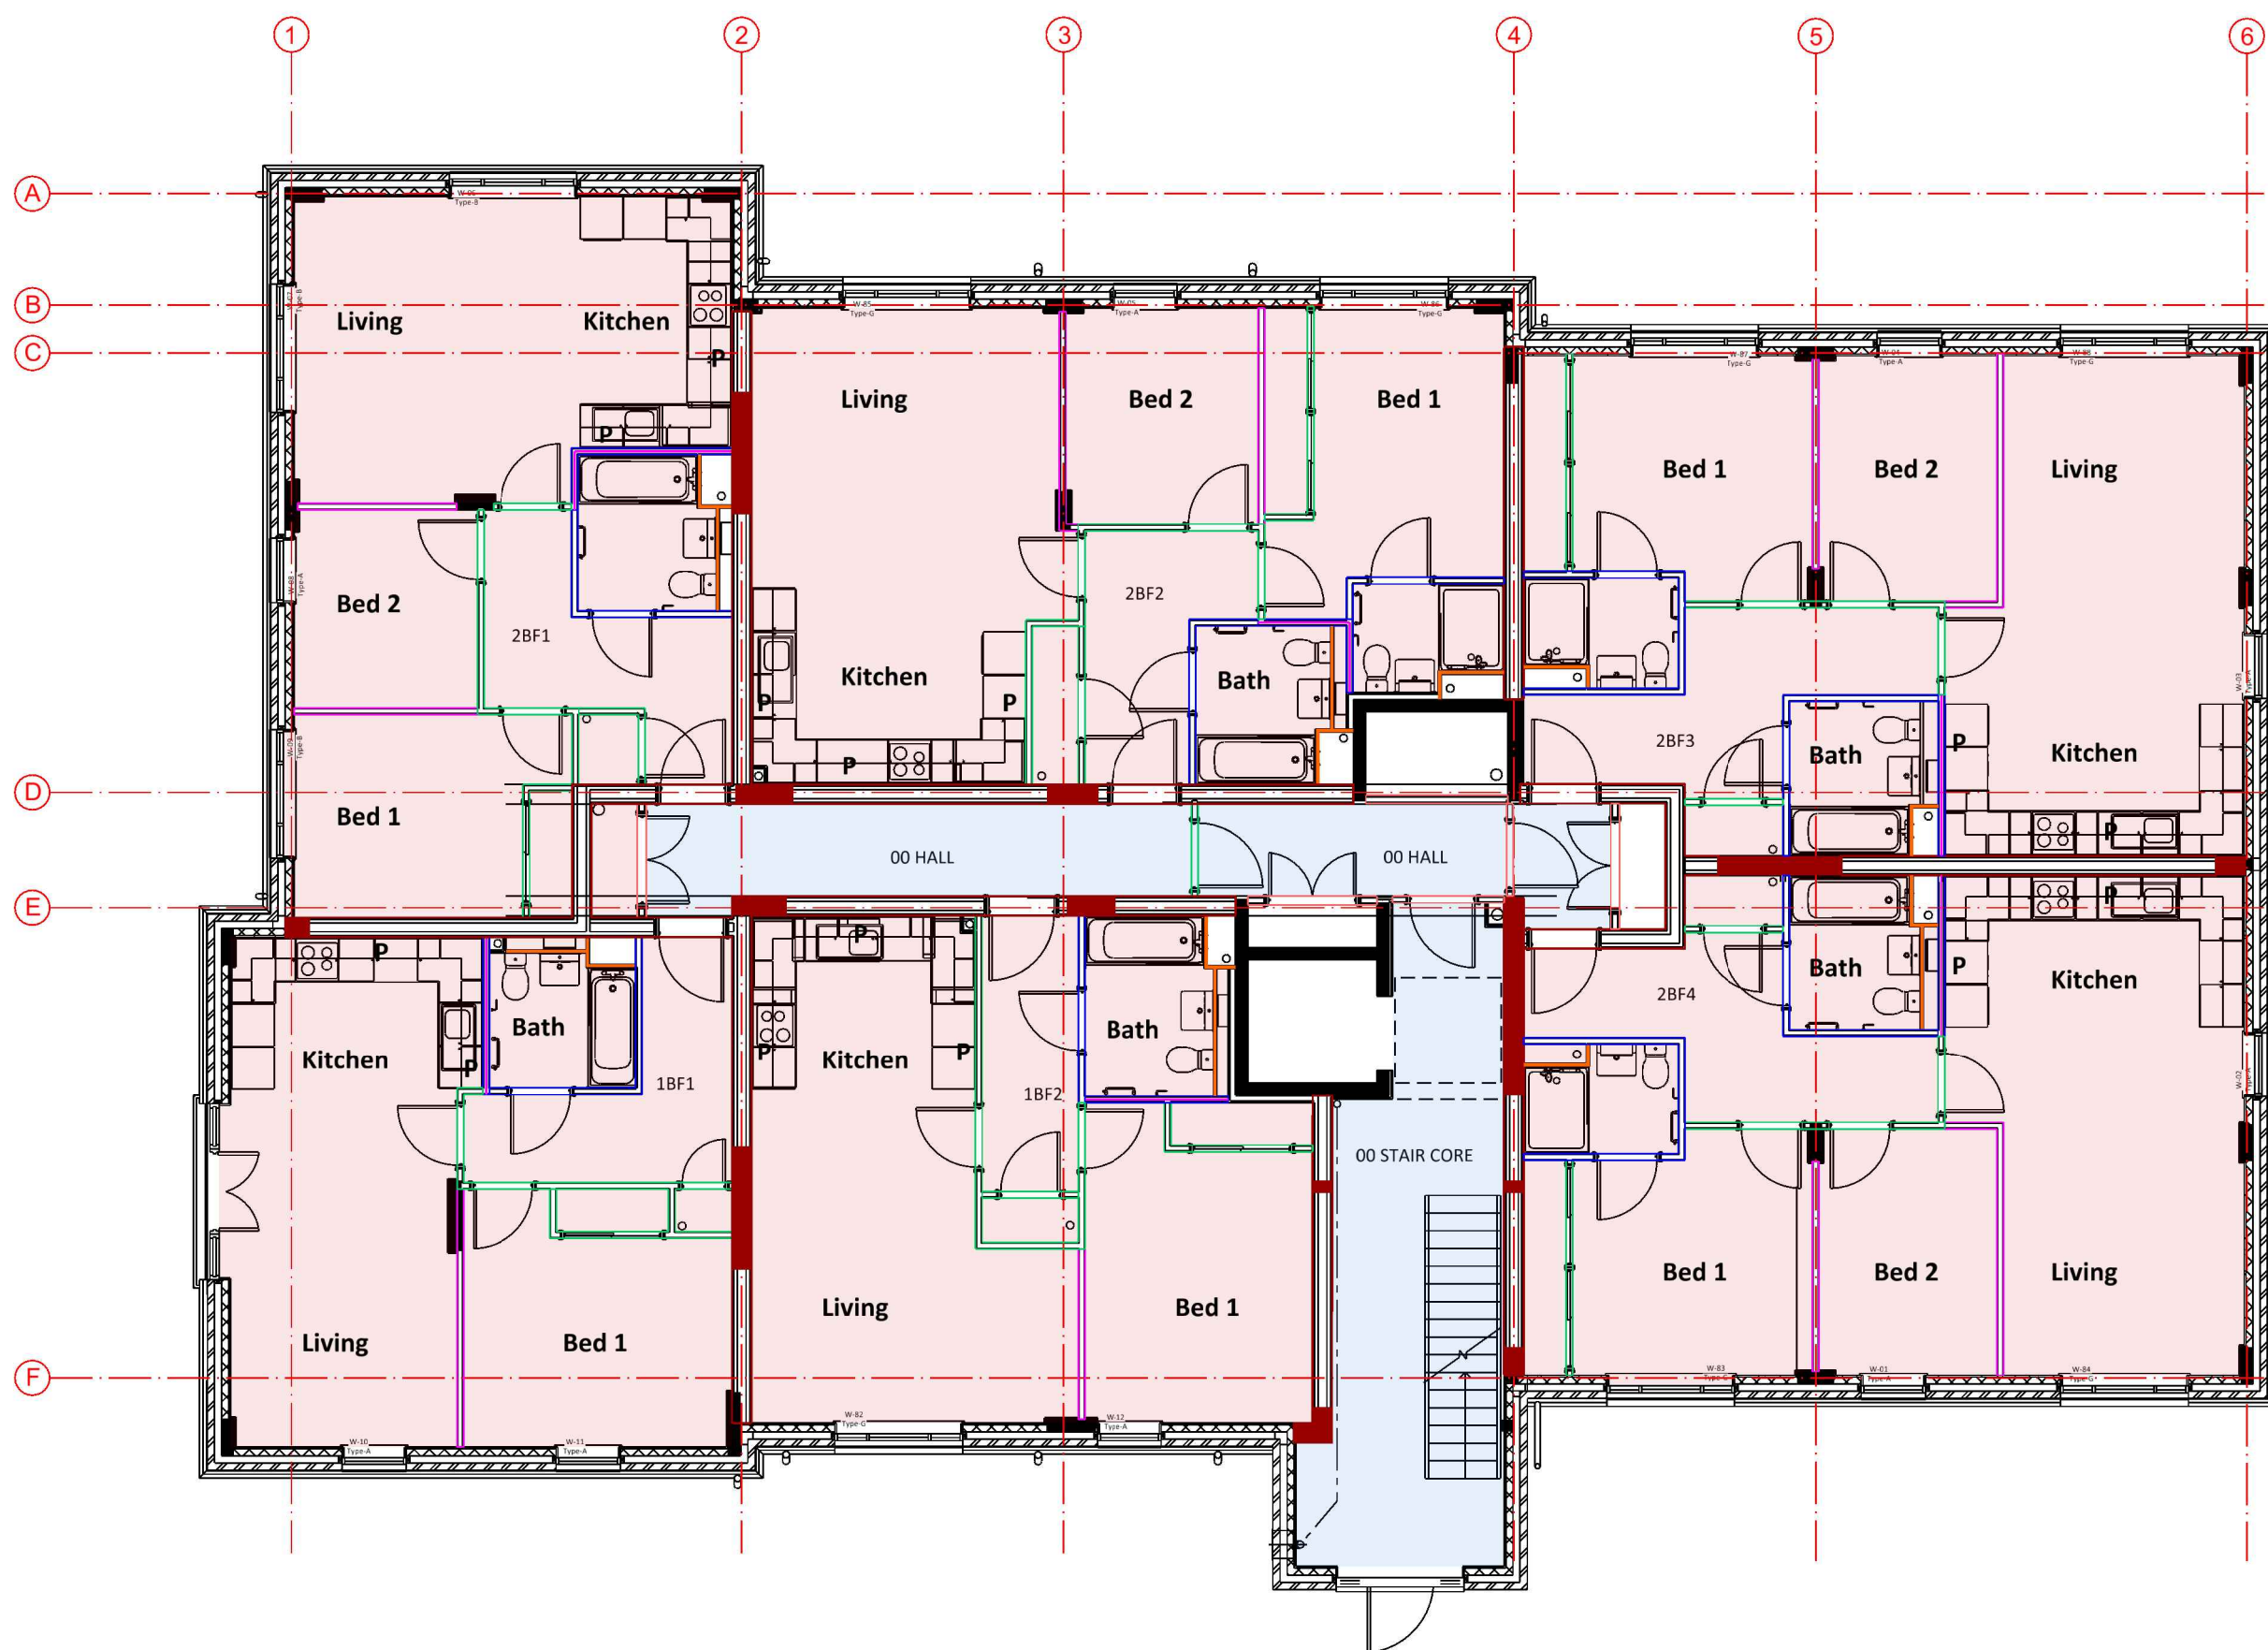

Proposed Ground Floor Plan

BLOCK A		
PLOT NUMBER	FLAT TYPE	
1, 7, 13, 19, 25	1BF1	
2, 8, 14, 20, 26	1BF2	
3, 9, 15, 21, 27	2BF1	
4, 10, 16, 22, 28	2BF2	
5, 11, 17, 23	2BF3	
6, 12, 18, 24	2BF4	

BLOCK B		
PLOT NUMBER	FLAT TYPE	
29, 35, 41, 47, 53	1BF1	
30, 36, 42, 48, 54	1BF2	
31, 37, 43, 49, 55	2BF1	
32, 38, 44, 50, 56	2BF2	
33, 39, 45, 51	2BF3	
34, 40, 46, 52	2BF4	

BLOCK C		
PLOT NUMBER	FLAT TYPE	
58, 64, 70, 76	1BF1	
57, 63, 69, 75	1BF2	
59, 65, 71, 77	2BF1	
60, 66, 72, 78	2BF2	
61, 67, 73	2BF3	
62, 68, 74	2BF4	

Walls:

- Party/Compartment Wall:**
TYPE -IPW1 Concrete shear wall with linings as detail Refer to 1132-INT 01 Specification K10/155A
- Party/Compartment Wall:**
TYPE -IPW2 Gypwall Quiet Refer to 1132-INT 02 Specification K10/125A
- Party/Compartment Wall:**
TYPE -IPW4 140mm Dense Blockwork Walls with Linings as detail Refer to 1132-218 Specification K10/155B
- Internal Partition: NFR + FD30**
TYPE -IW1 GypWall Classic 97mm overall wall thickness. One layer of 12.5mm WallBoard each side of Gypframe 70 S 50 "C" Studs, Specification K10/120C
- Internal Partition - Sound Rated: 40dB**
TYPE -IW2 GypWall Classic 97mm overall wall thickness. One layer of 12.5mm Gyproc Wallboard each side of Gypframe 70 S 50 "C" Studs with 25mm Isover APR 1200 within the cavity. Specification K10/120D
- Internal Partition - Plywood Lined:**
TYPE -IW3 GypWall Classic 97mm overall wall thickness. One layer of 12.5mm Gyproc Wallboard to one side & One layer of 9mm WBP plywood to half height fixed between studs and one layer of 12.5mm Moisture resistant board to the wet side on Gypframe 70 S 50 "C" Studs. 25mm Isover APR 1200 within the cavity where required. Specification K10/120E to achieve 40dB

- Internal Partition: FD60**
TYPE -IW4 GypWall Classic 102mm overall wall thickness. One layer of 15mm Fireline board each side of Gypframe 70 S 50 "C" Studs, Specification K10/120F

Ceilings:

- Apartment Acoustic Ceiling:**
TYPE -C1 Casoline MF Ceiling Refer to 1132-INT 01 Specification K10/220B
- Common Area Acoustic Ceiling:**
TYPE -C2 Class C Sound Absorbent board Specification K10/220A 15mm Gyproc Fireline board to be incorporated to top floor common area
- Fire Rated Ceiling: 30 minutes**
TYPE -C3 15mm Gyproc Fireline board Specification K10/245C

Lift Shaft Lining:
Refer to Drawing 220 IW4

Allow for plywood lining to kitchen walls to full extent of the worktops

All partitions extend to underside of floor

Water-resistant Backing Board:
12.5mm Moisture resistant plasterboard on timber framework for tiling

NOTES
Do not scale this drawing - use figured dimensions only. All dimensions are to be checked before implementation. Any discrepancies are to be advised immediately. All information is copyright of DLA Architects Practice and may not be used or reproduced without prior permission.

REVISIONS
P2 14/11/2017
C1 10/04/2018

Plot numbers for each block and additional insulation for apartment 1BF2 added
Specification notes updated

Note:
Blocks B & C Similar

CAREYS
GUN HILL DEVELOPMENT ZONE - PHASE 1
BLOCK A - INTERNAL WALL & CEILING LININGS

DATE: Oct 2017
DRAWING NUMBER: 1132-200

SCALE: 1:100@A1
REVISION: C1

STATUS: INFORMATION

DLA ARCHITECTS PRACTICE
INTEGRATED ARCHITECTURE

50 North Thirteenth Street
CENTRAL MILTON KEYNES, MK9 3BP
T: 01908 259719 F: 01908 605747
email: mail@dla-architects.com

© DLA ARCHITECTS PRACTICE LTD