
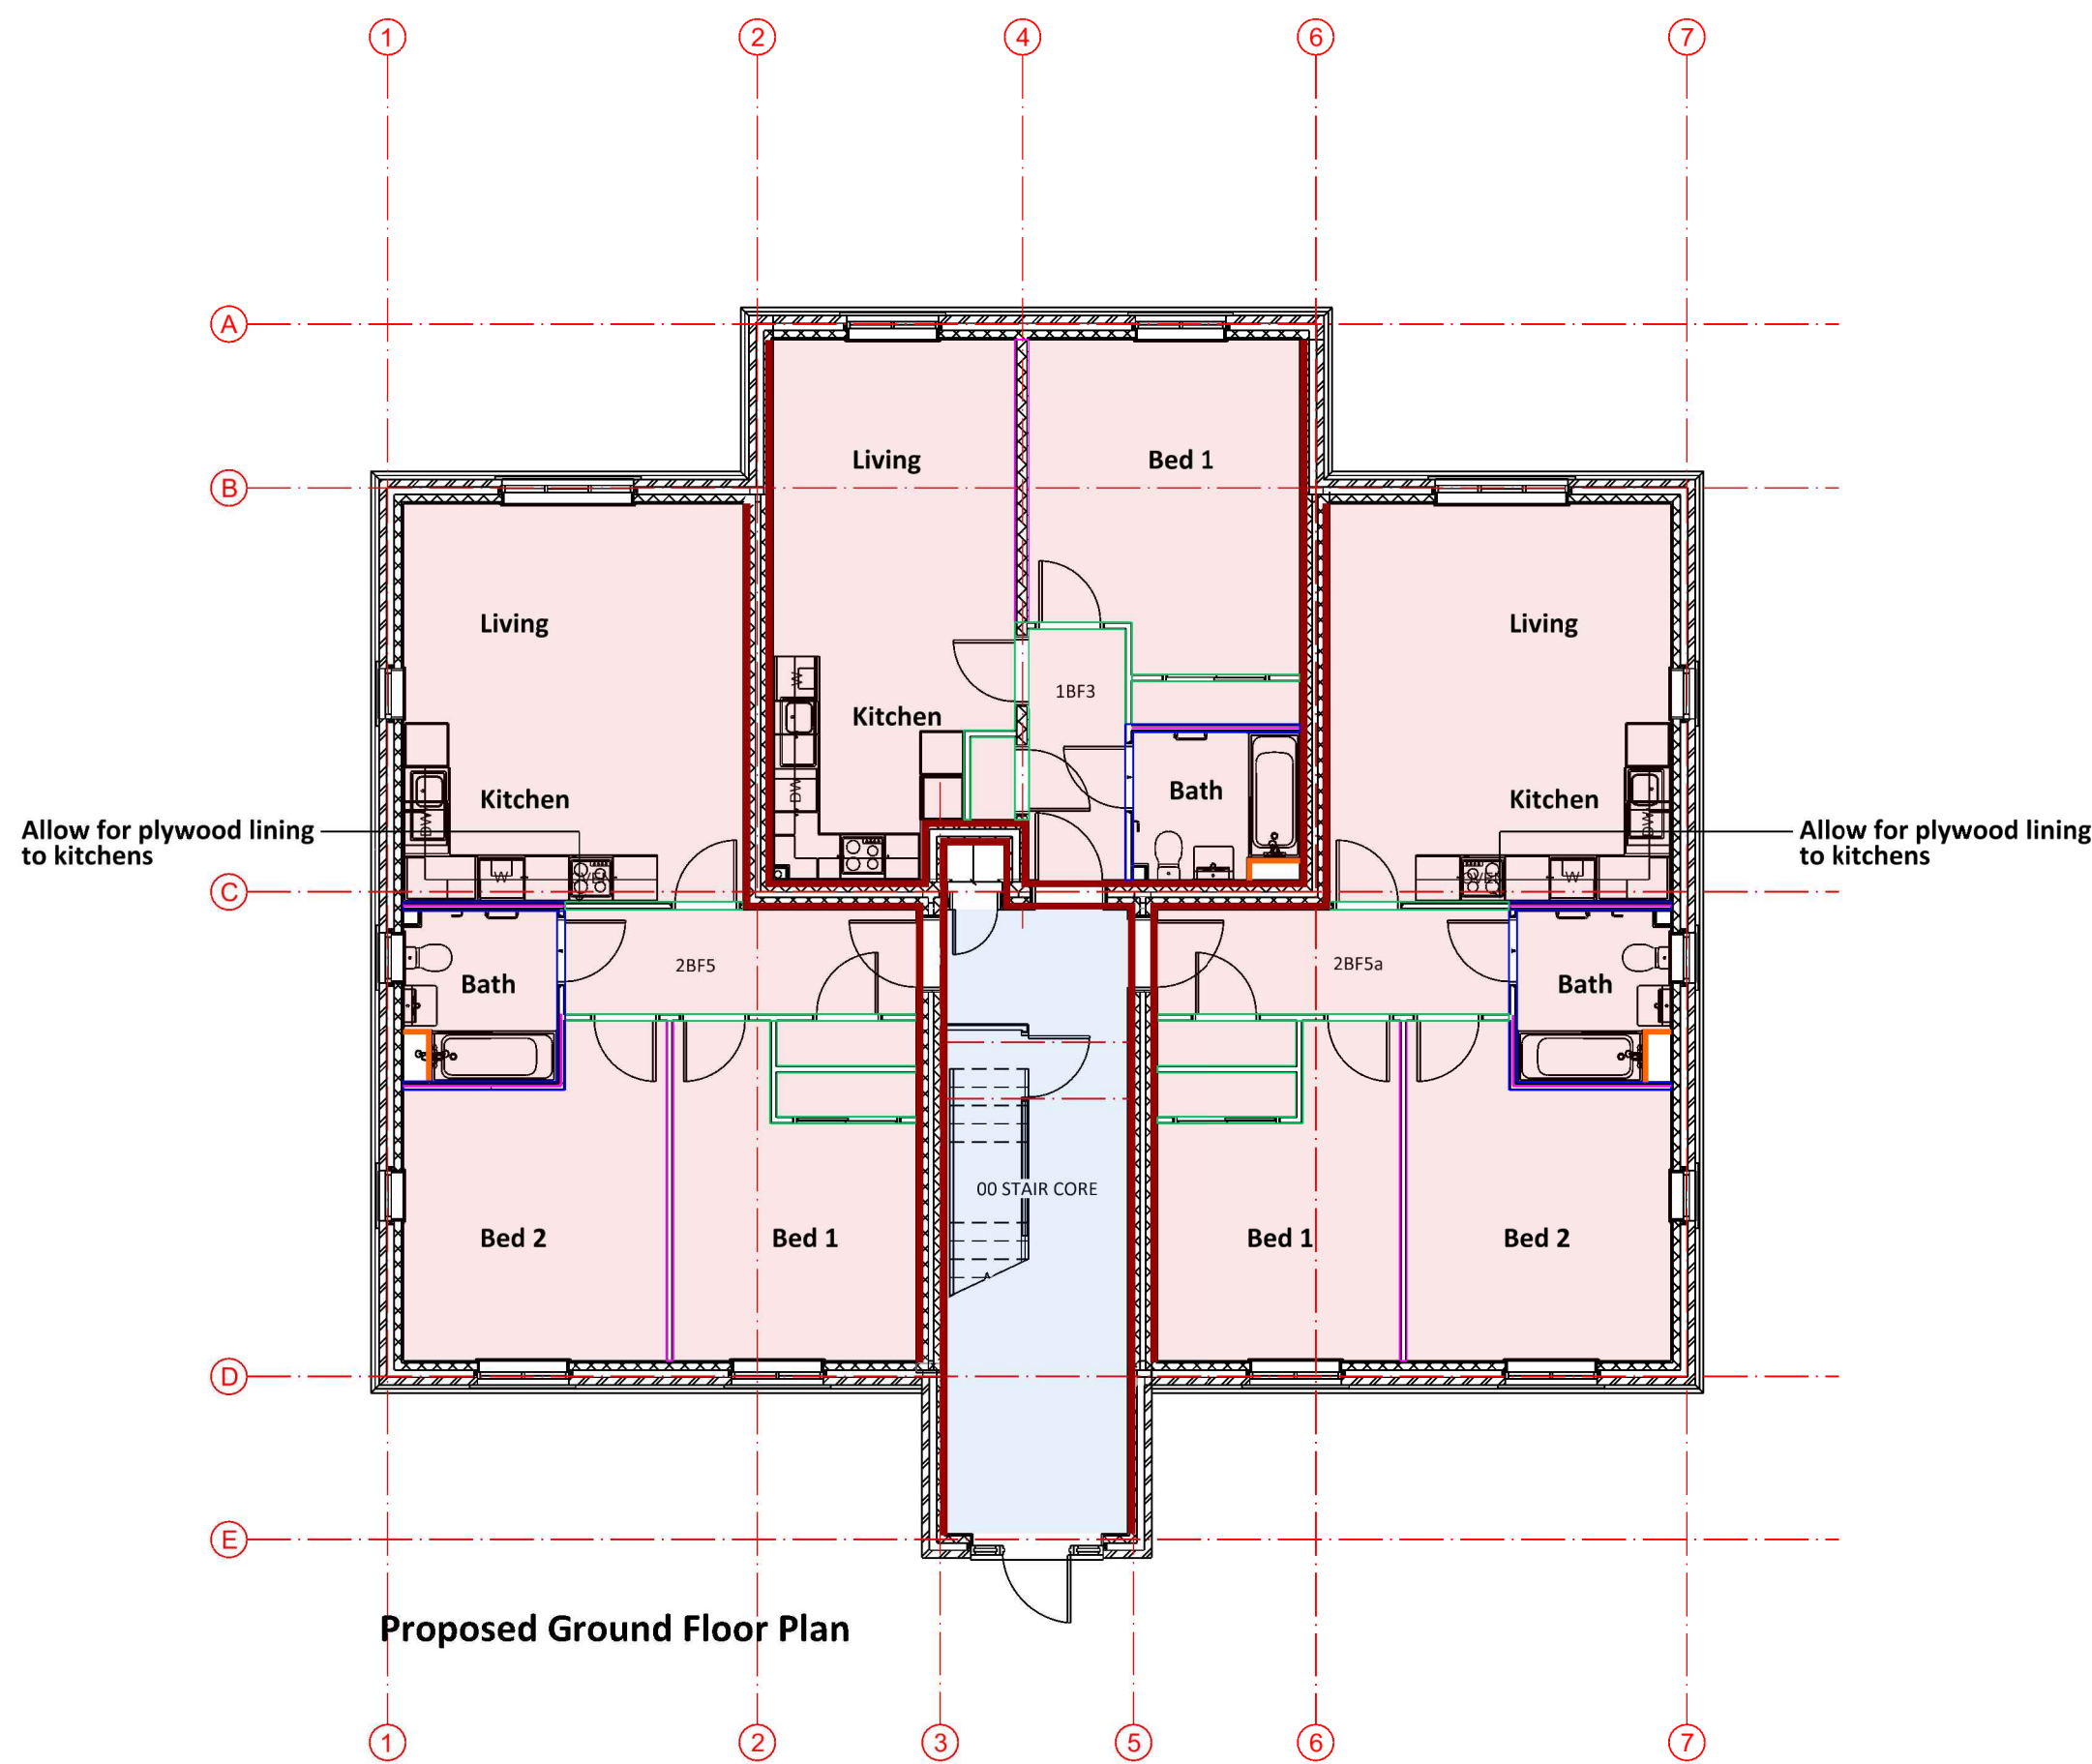
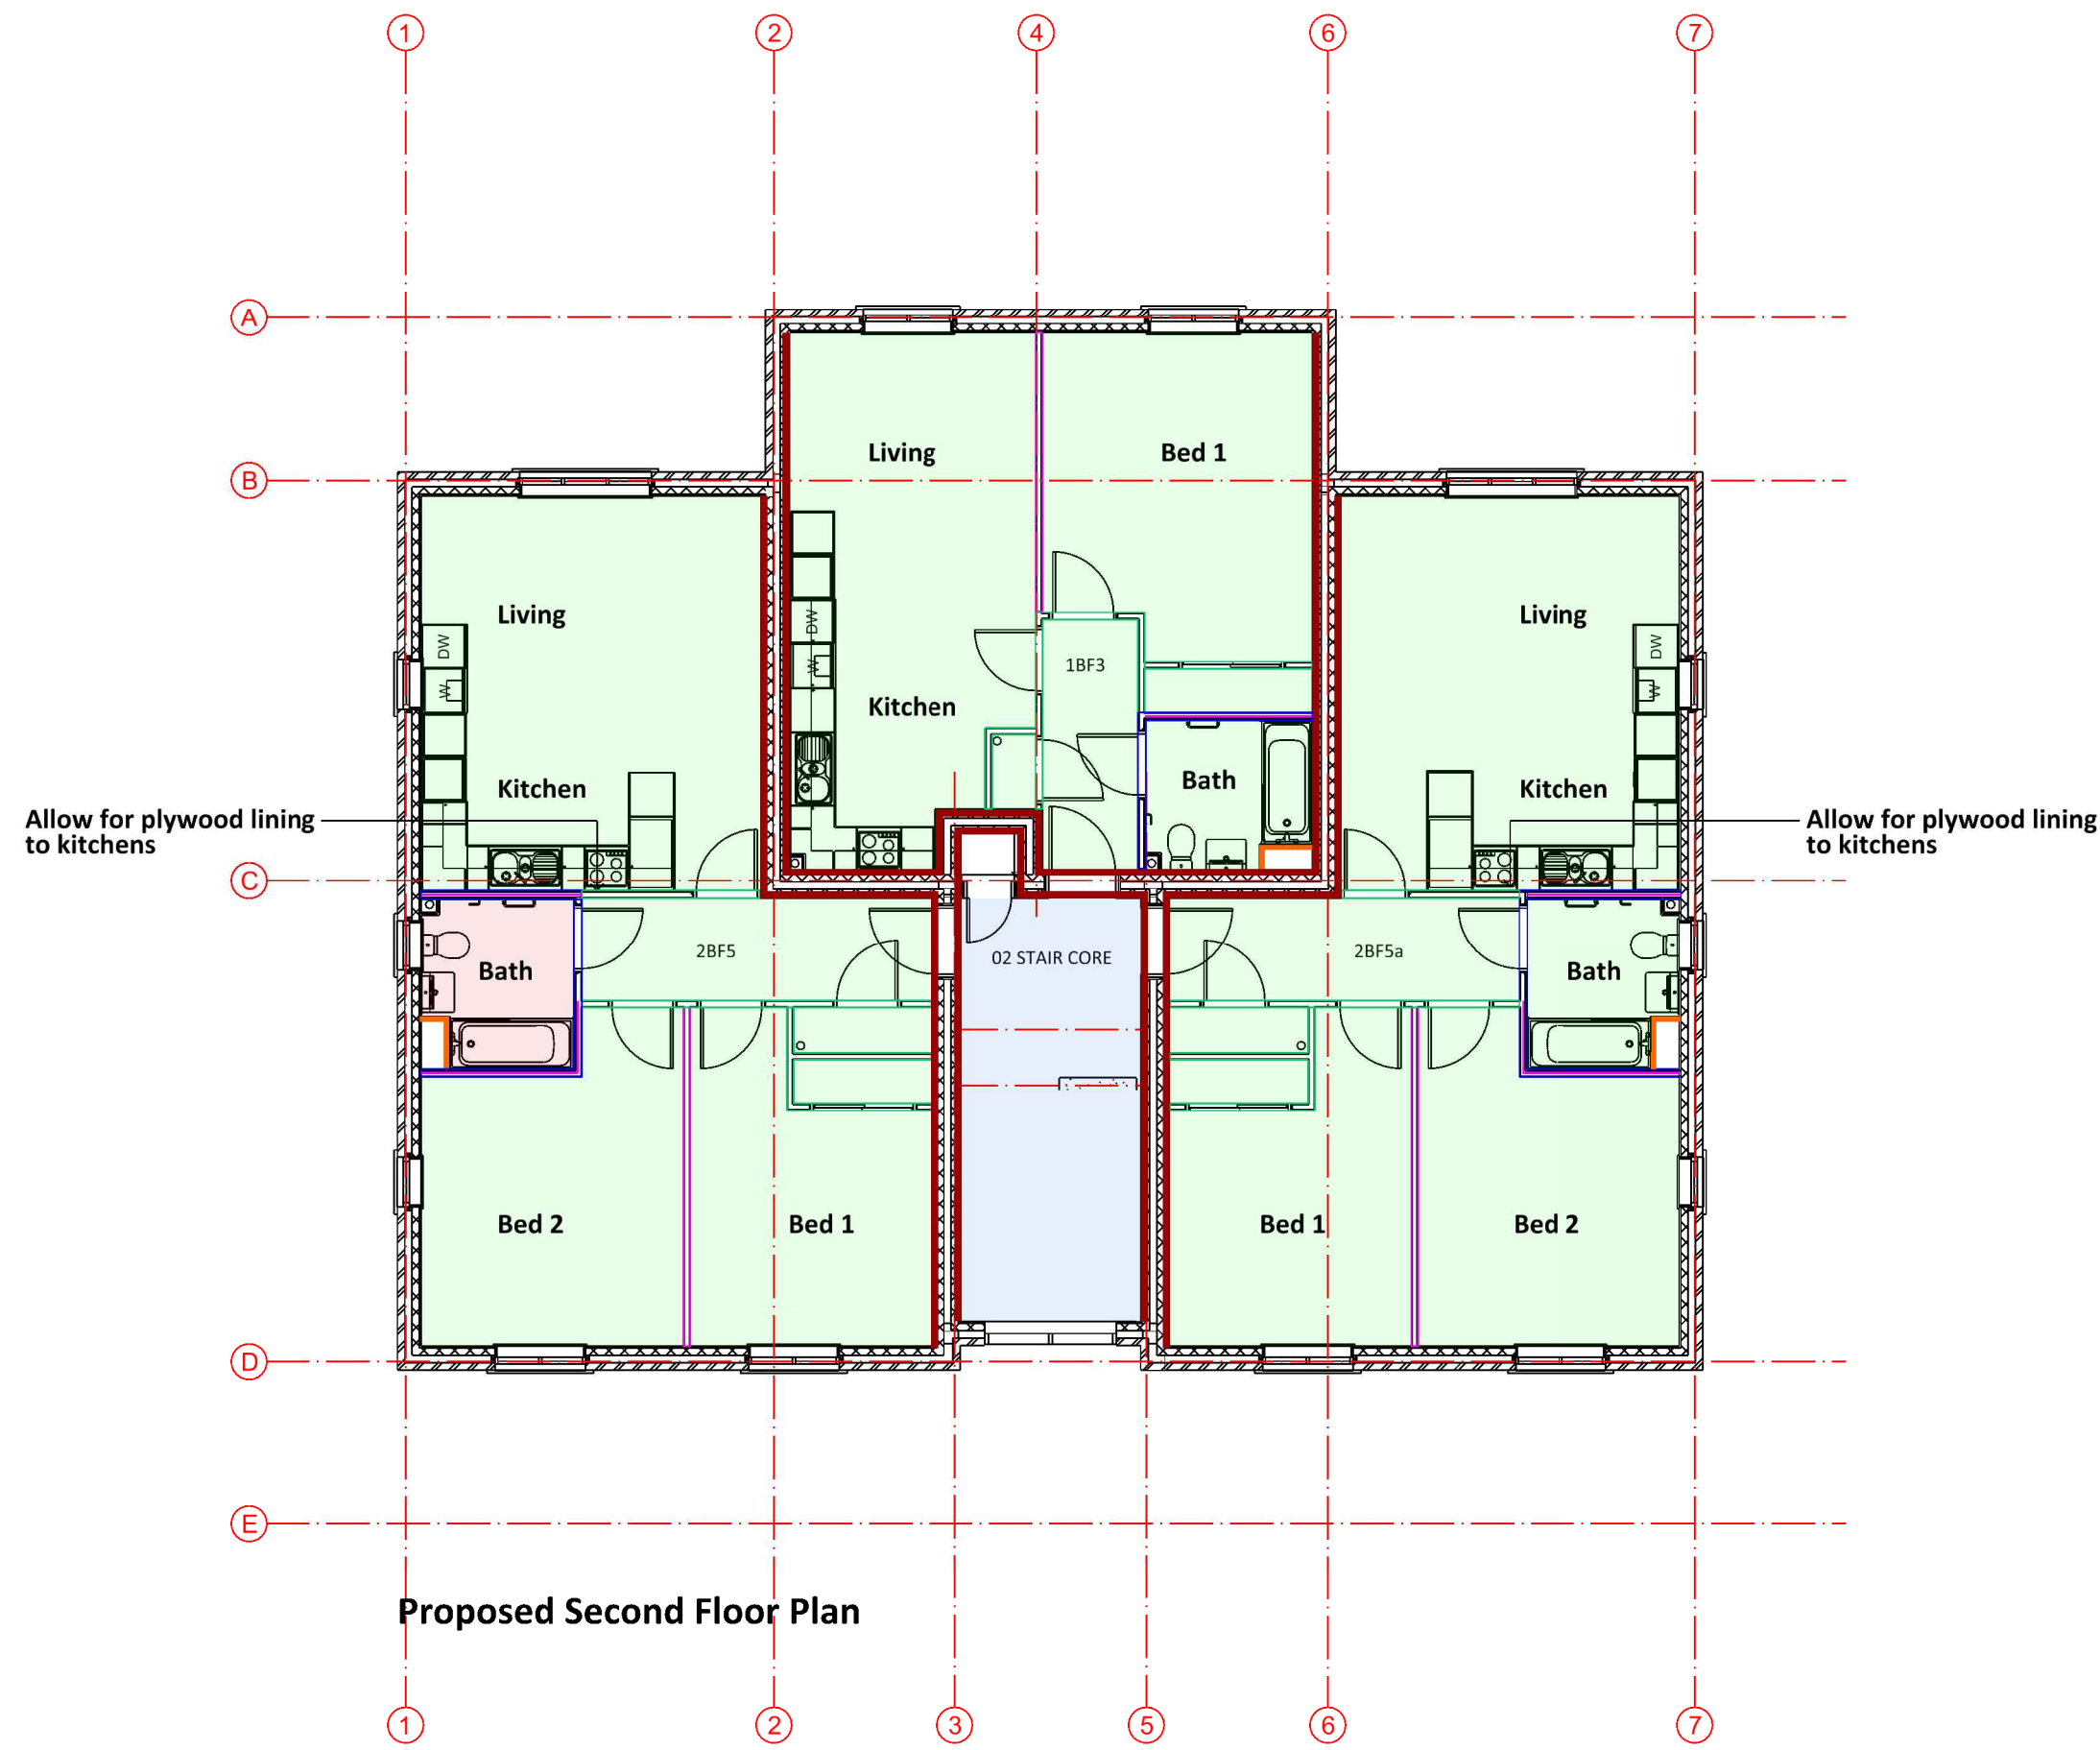


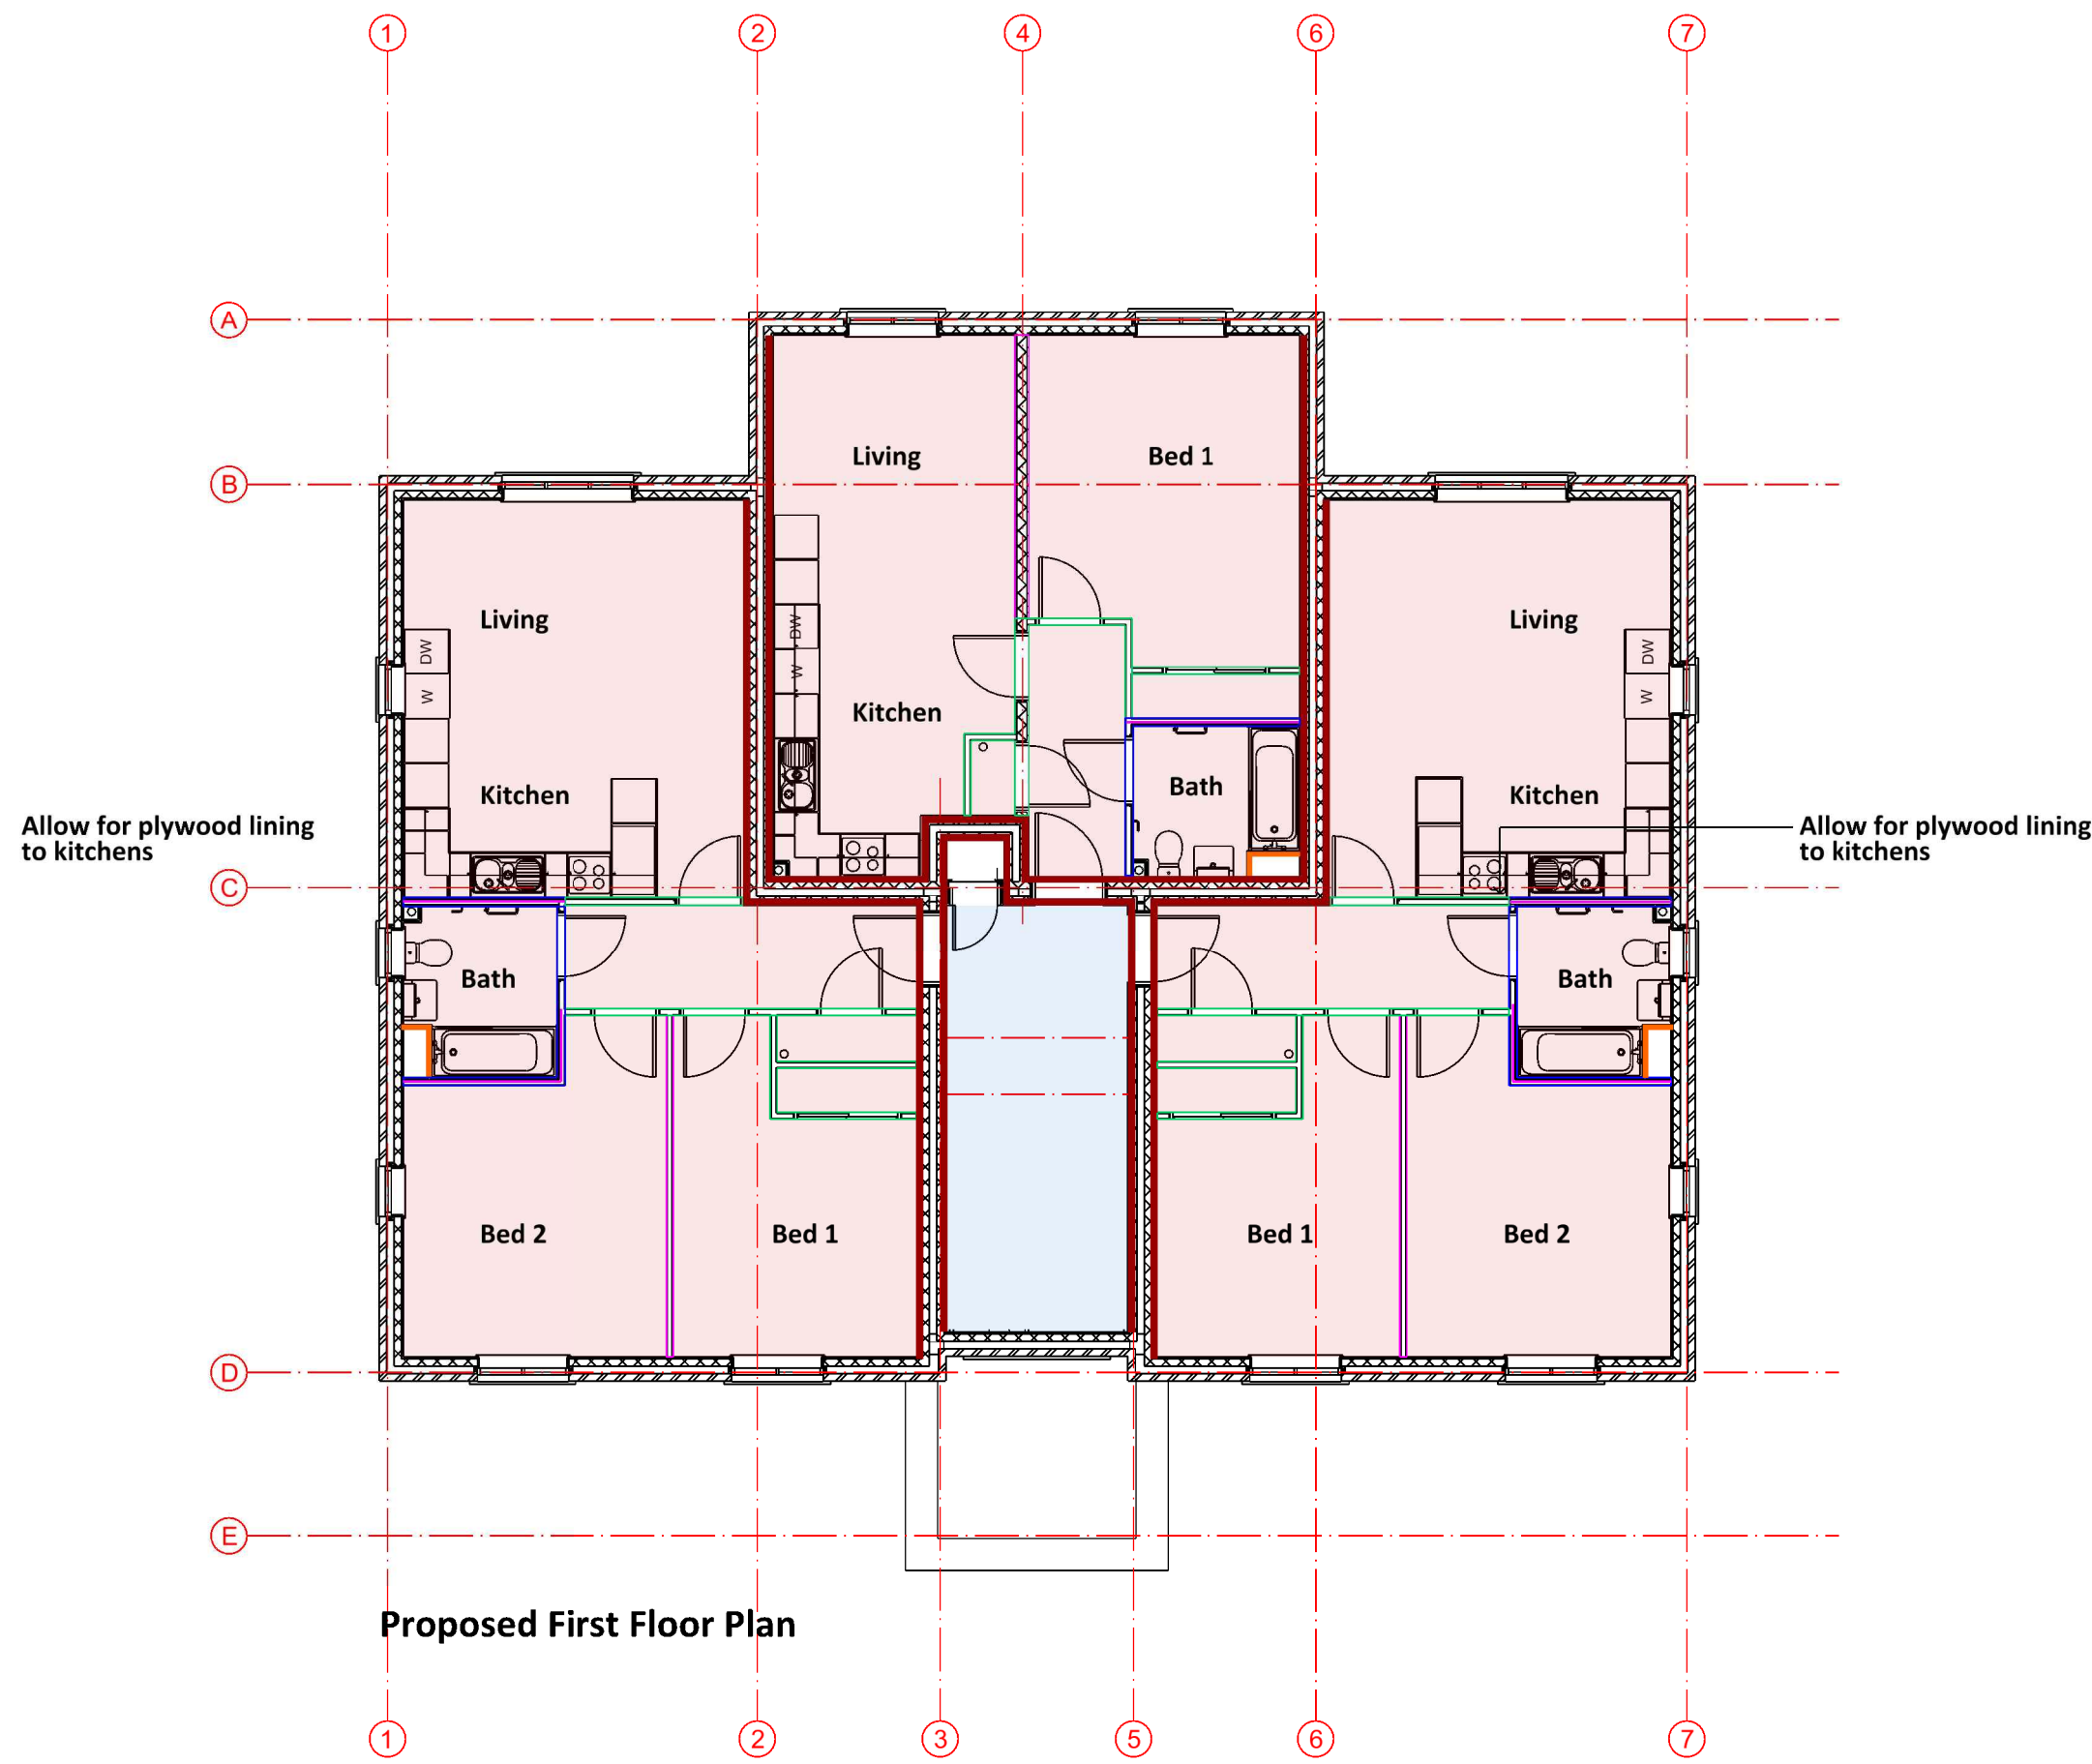

Walls:

- Party/Compartment Wall: 60 Minute FR**
TYPE -IPW3 1 Layer of 12.5mm Gyproc Soundbloc on plaster dabs to blockwork party wall Refer to 1132-212 Specification K10/156A
- Internal Partition: NFR + FD30**
TYPE -IW1 GypWall Classic 97mm overall wall thickness. One layer of 12.5mm WallBoard each side of Gypframe 70 S 50 "C" Studs, Specification K10/120C
- Internal Partition - Sound Rated: 40dB**
TYPE -IW2 GypWall Classic 97mm overall wall thickness. One layer of 12.5mm Gyproc Soundbloc each side of Gypframe 70 S 50 "C" Studs with 25mm Isover APR 1200 within the cavity. Specification K10/120D
- Internal Partition - Plywood Lined:**
TYPE -IW3 GypWall Classic 97mm overall wall thickness. One layer of 12.5mm Gyproc Wallboard to one side & One layer of 9mm WBP plywood to half height fixed between studs and one layer of 12.5mm Moisture resistant board to the wet side on Gypframe 70 S 50 "C" Studs. 25mm Isover APR 1200 within the cavity where required. Specification K10/120E to achieve 40dB
- Water-resistant Backing Board:**
12.5mm Moisture resistant plasterboard on timber framework for tiling

Ceilings:

- Apartment Acoustic Ceiling:**
TYPE -C1b Casoline MF Ceiling with 15mm Soundbloc board Refer to 1132-INT 01 Specification K10/220C
- Common Area Acoustic Ceiling:**
TYPE -C2 Class C Sound Absorbent board 15mm Gyproc Fireline board to be incorporated to top floor common area Specification K10/220A
- Fire Rated Ceiling: 30 minutes**
TYPE -C3 15mm Gyproc Fireline board Specification K10/245C

NOTES
Do not scale this drawing - use figured dimensions only.
All dimensions are to be checked before implementation.
Any discrepancies are to be advised immediately.
All information is copyright of DLA Architects Practice and may not be used or reproduced without prior permission.

REVISIONS
C1 10.04.2018 Specification notes updated

CAREYS
GUN HILL DEVELOPMENT ZONE - PHASE 1
BLOCK D - INTERNAL WALL & CEILING LININGS
DATE Oct 2017
DRAWING NUMBER 1132-203
SCALE 1:100@A1
REVISION C1
STATUS CONSTRUCTION

DLA ARCHITECTS PRACTICE
INTEGRATED ARCHITECTURE
50 North Thirteenth Street
CENTRAL MILTON KEYNES, MK9 3BP
T: 01908 259719 F: 01908 605747
email: mail@dl-a-architects.com
© DLA ARCHITECTS PRACTICE LTD