
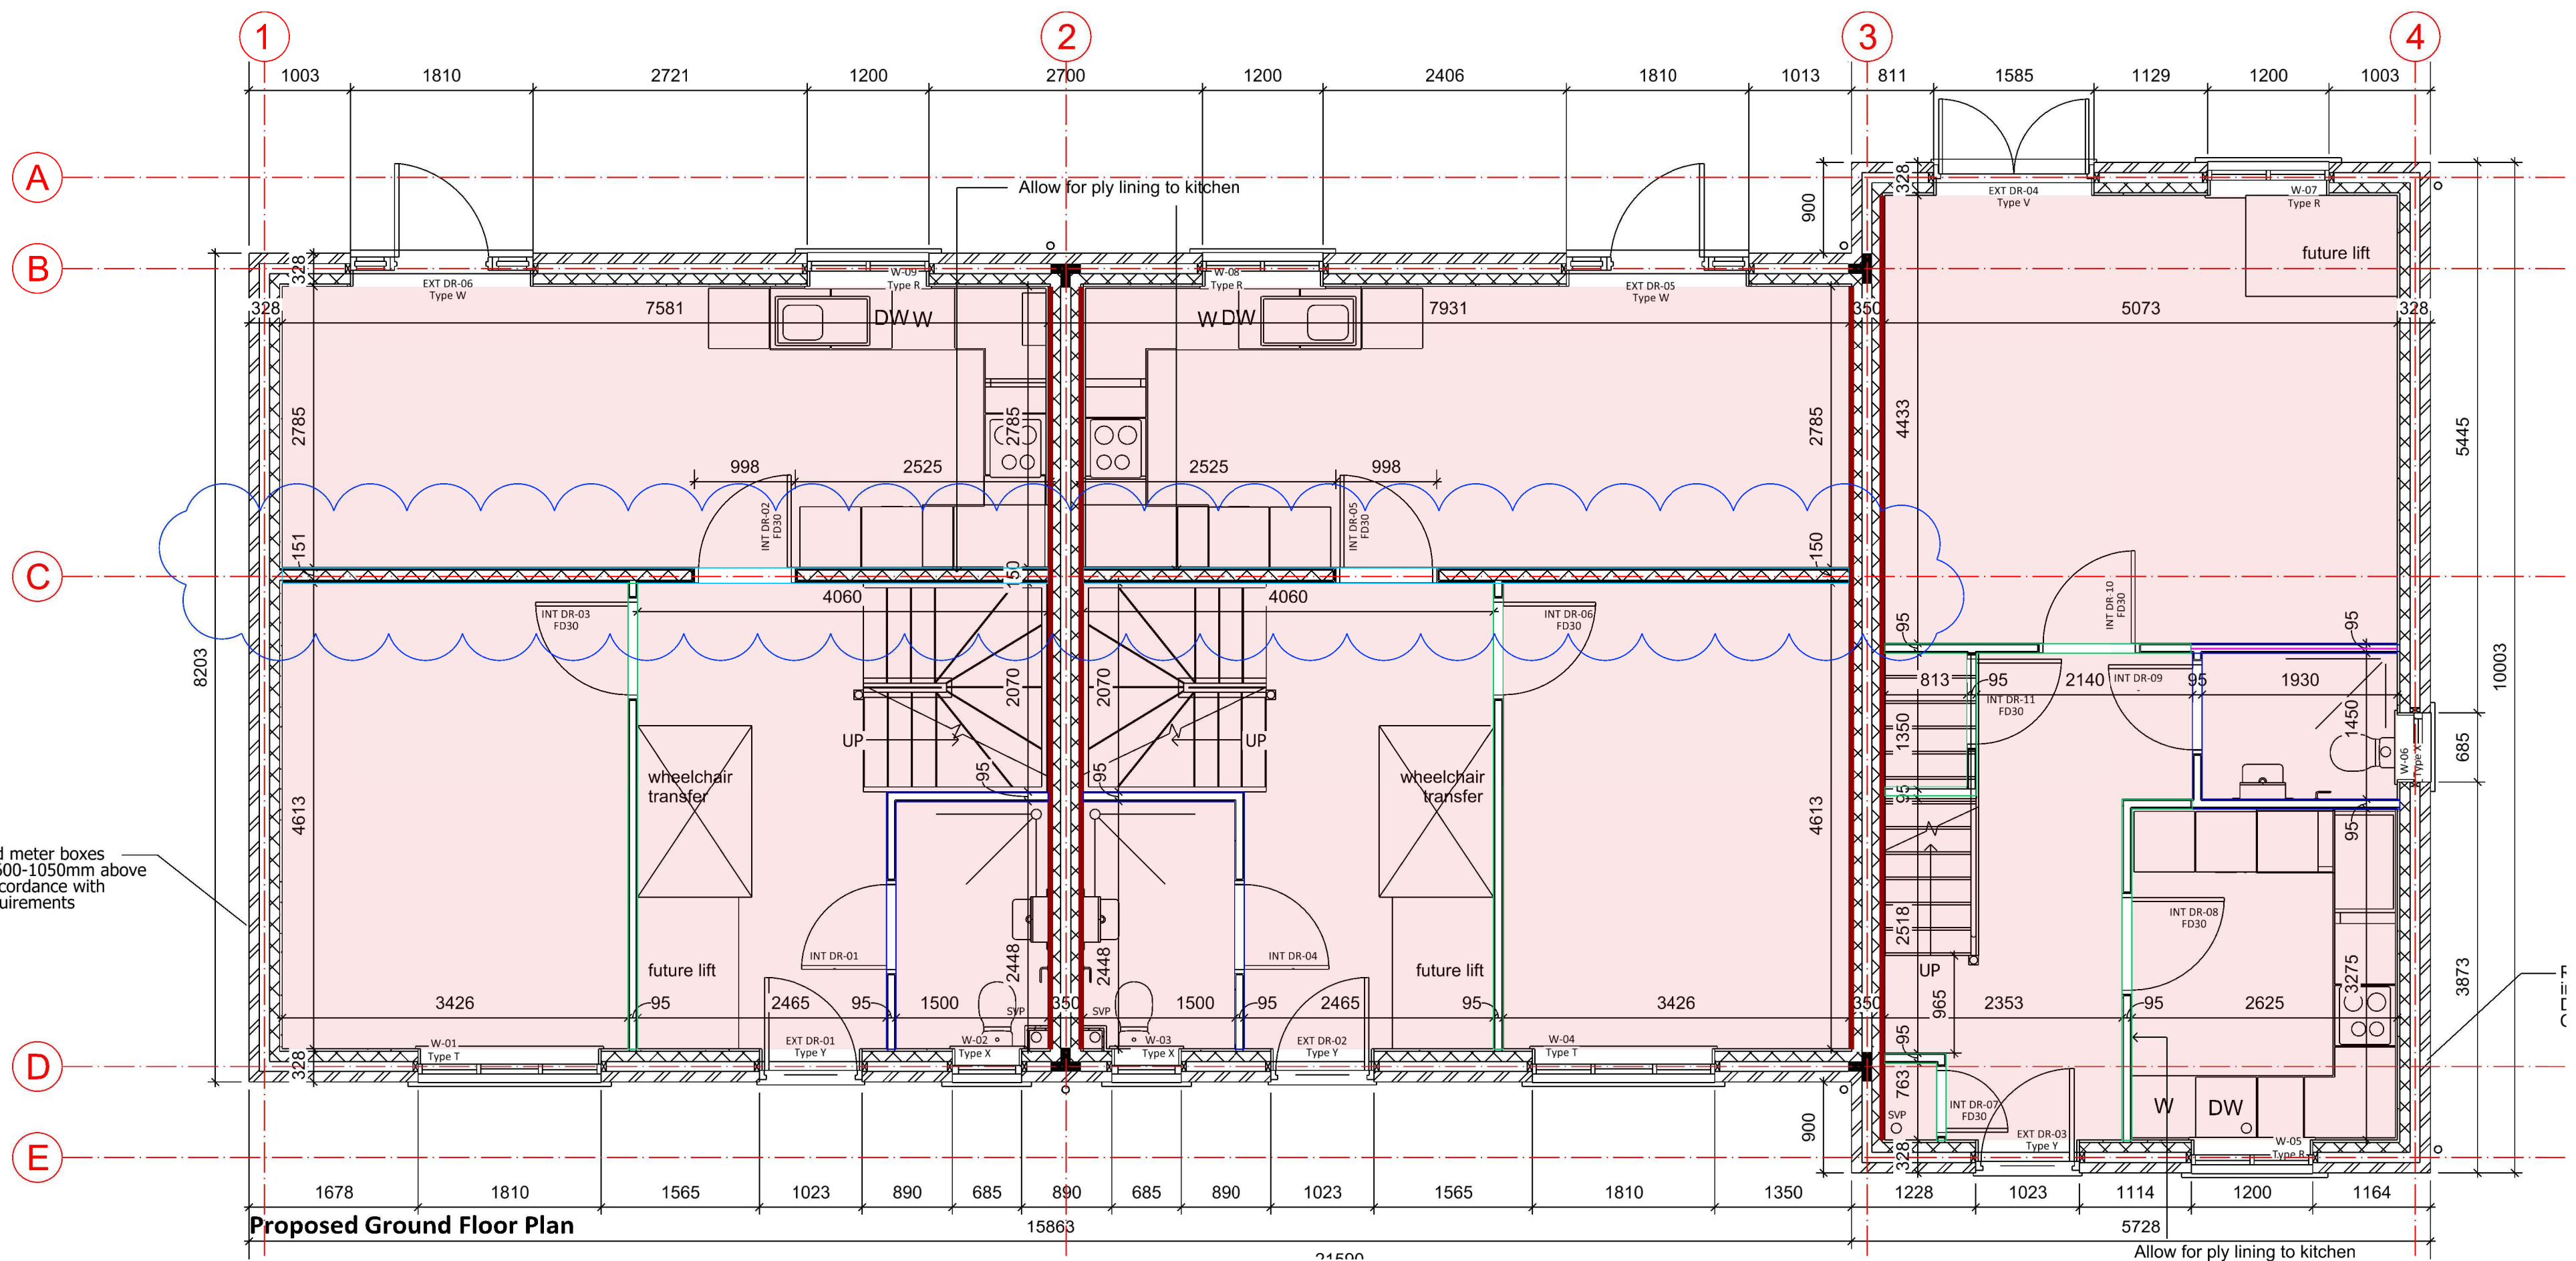


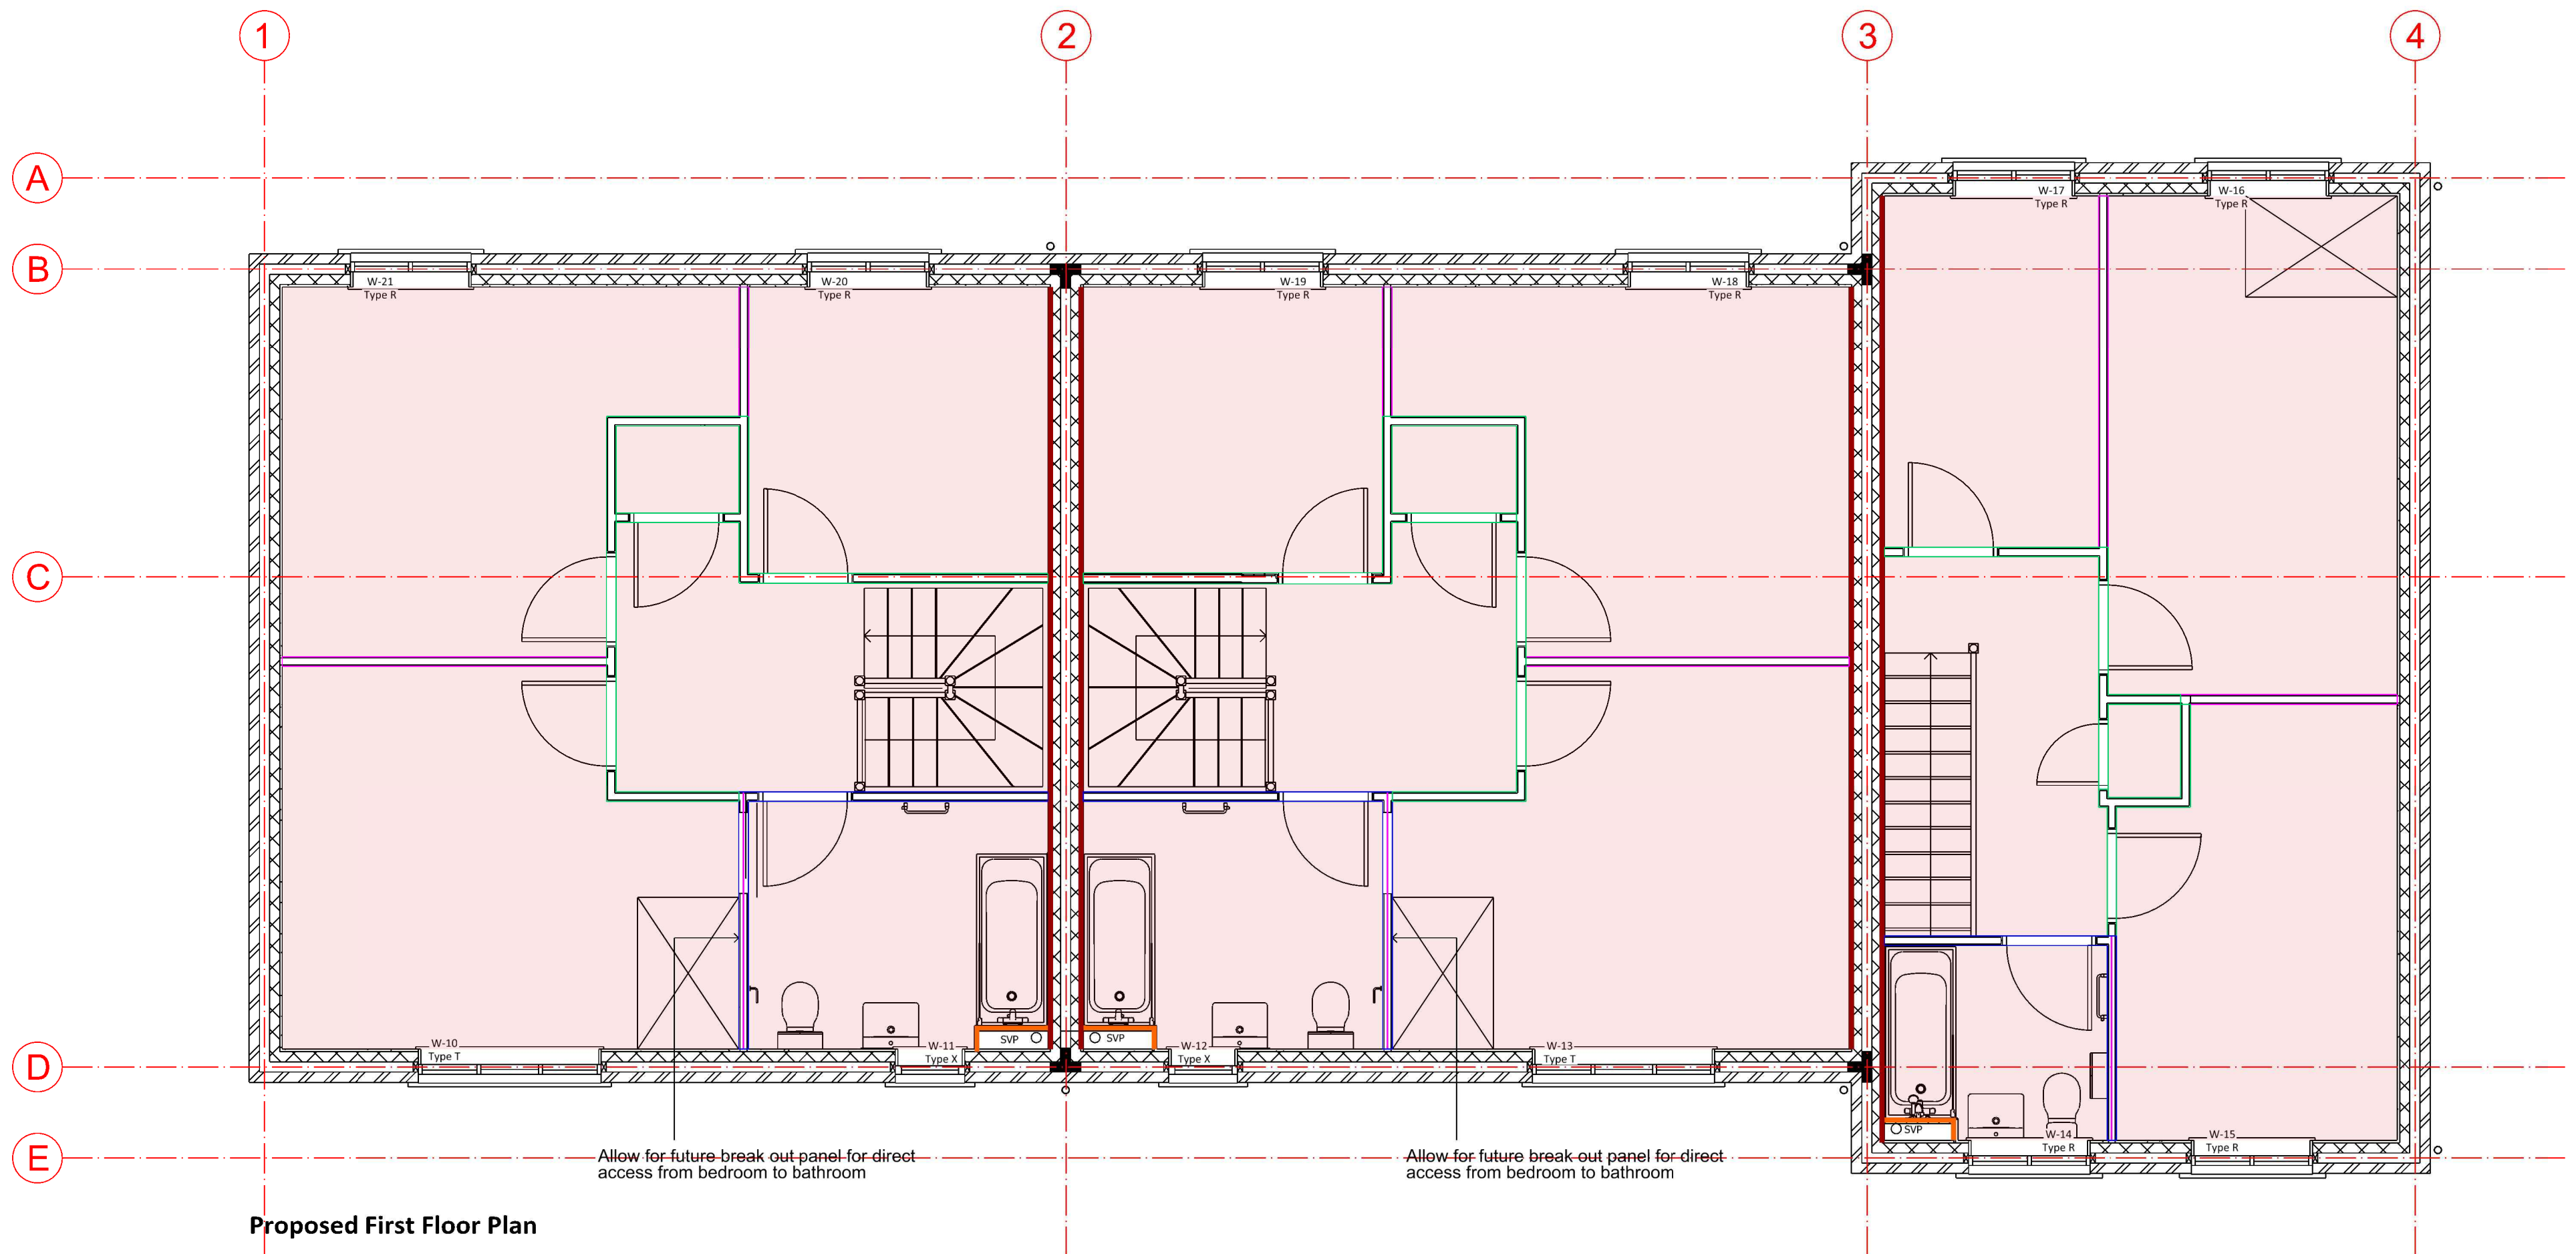

Walls:

- Party/Compartment Wall:**
TYPE -IPW3 1 Layer of 12.5mm Gyproc Soundbloc on plaster dabs to blockwork party wall Refer to 1132-213 & 217 Specification K10/156A
- Internal Partition: NFR + FD30**
TYPE -IW1 GypWall Classic 97mm overall wall thickness. One layer of 12.5mm WallBoard each side of Gypframe 70 S 50 "C" Studs, Specification K10/120C
- Internal Partition - Sound Rated: 40dB**
TYPE -IW2 GypWall Classic 97mm overall wall thickness. One layer of 12.5mm Gyproc Wallboard each side of Gypframe 70 S 50 "C" Studs with 25mm Isover APR 1200 within the cavity. Specification K10/120D
- Internal Partition - Plywood Lined:**
TYPE -IW3 GypWall Classic 97mm overall wall thickness. One layer of 12.5mm Gyproc Wallboard to one side & One layer of 9mm WBP plywood to half height fixed between studs and one layer of 12.5mm Moisture resistant board to the wet side on Gypframe 70 S 50 "C" Studs. 25mm Isover APR 1200 within the cavity where required. Specification K10/120E to achieve 40dB
- Water-resistant Backing Board:**
12.5mm Moisture resistant plasterboard on timber framework for tiling
- Internal Partition - Blockwork**
TYPE -IW4 1 Layer of 12.5mm Gyproc Soundbloc on plaster dabs each side of 100mm blockwork partition

Ceilings:

- Houses Acoustic Ceiling:**
TYPE -C4 Plasterboard Lining to Posi-Joists Refer to 1132-217 Specification K10/245A

NOTES
Do not scale this drawing - use figured dimensions only. All dimensions are to be checked before implementation. Any discrepancies are to be advised immediately. All information is copyright of DLA Architects Practice and may not be used or reproduced without prior permission.

REVISIONS
C1 10/04/2018 Specification notes amended
C2 15/05/2018 Central wall to plots 102 & 103 changed to blockwork

Buttress walls:
Option to line both sides of walls with 12mm plywood to form a buttress to omit the wind posts identified by Rolton's. This is to be reviewed in terms of costs comparison

Additional plywood Lining to be incorporated where radiators fixed to walls final location need to be co-ordinated with M&E contractor

CARYES
GUN HILL DEVELOPMENT ZONE - PHASE 1
HOUSES, PLOTS 102-104 - WALL & CEILING LININGS
DATE Oct 2017
DRAWING NUMBER 1132-205
SCALE 1:50@A1
REVISION C2
STATUS CONSTRUCTION

DLA ARCHITECTS PRACTICE
INTEGRATED ARCHITECTURE
50 North Thirteenth Street
CENTRAL MILTON KEYNES, MK9 3BP
T: 01908 259719 F: 01908 605747
email: mail@dla-architects.com

© DLA ARCHITECTS PRACTICE LTD