




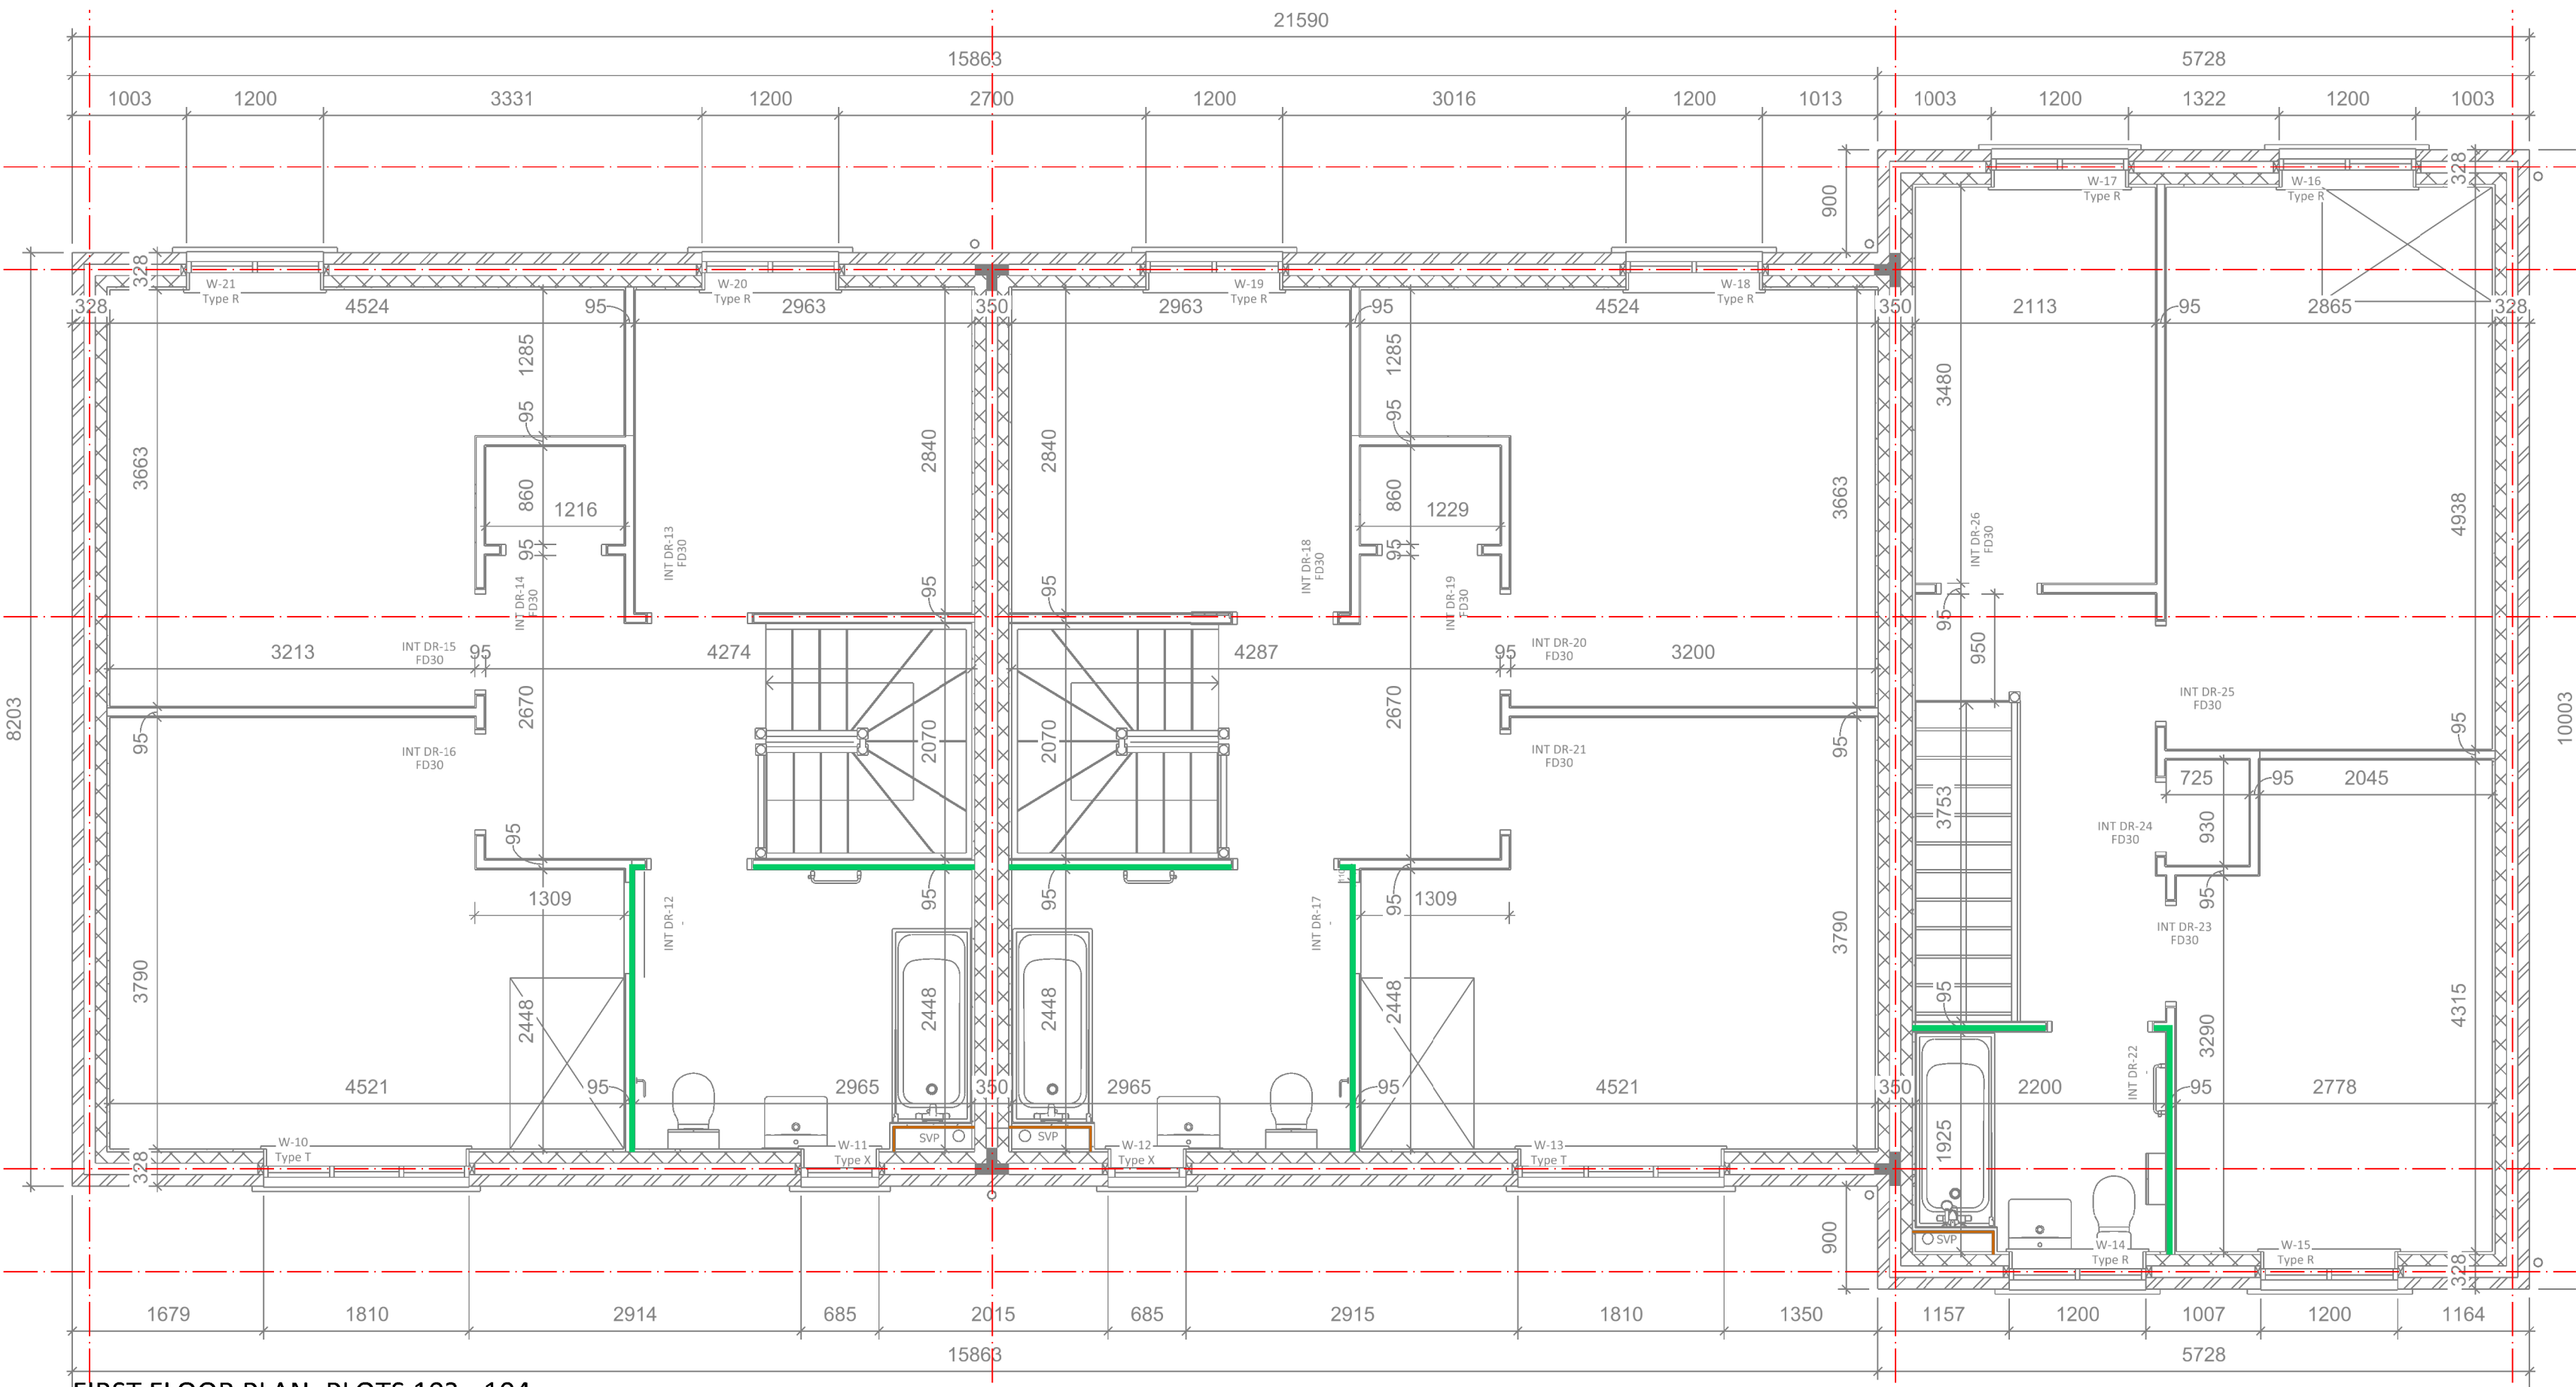


FIRST FLOOR PLAN: PLOTS 102 - 104

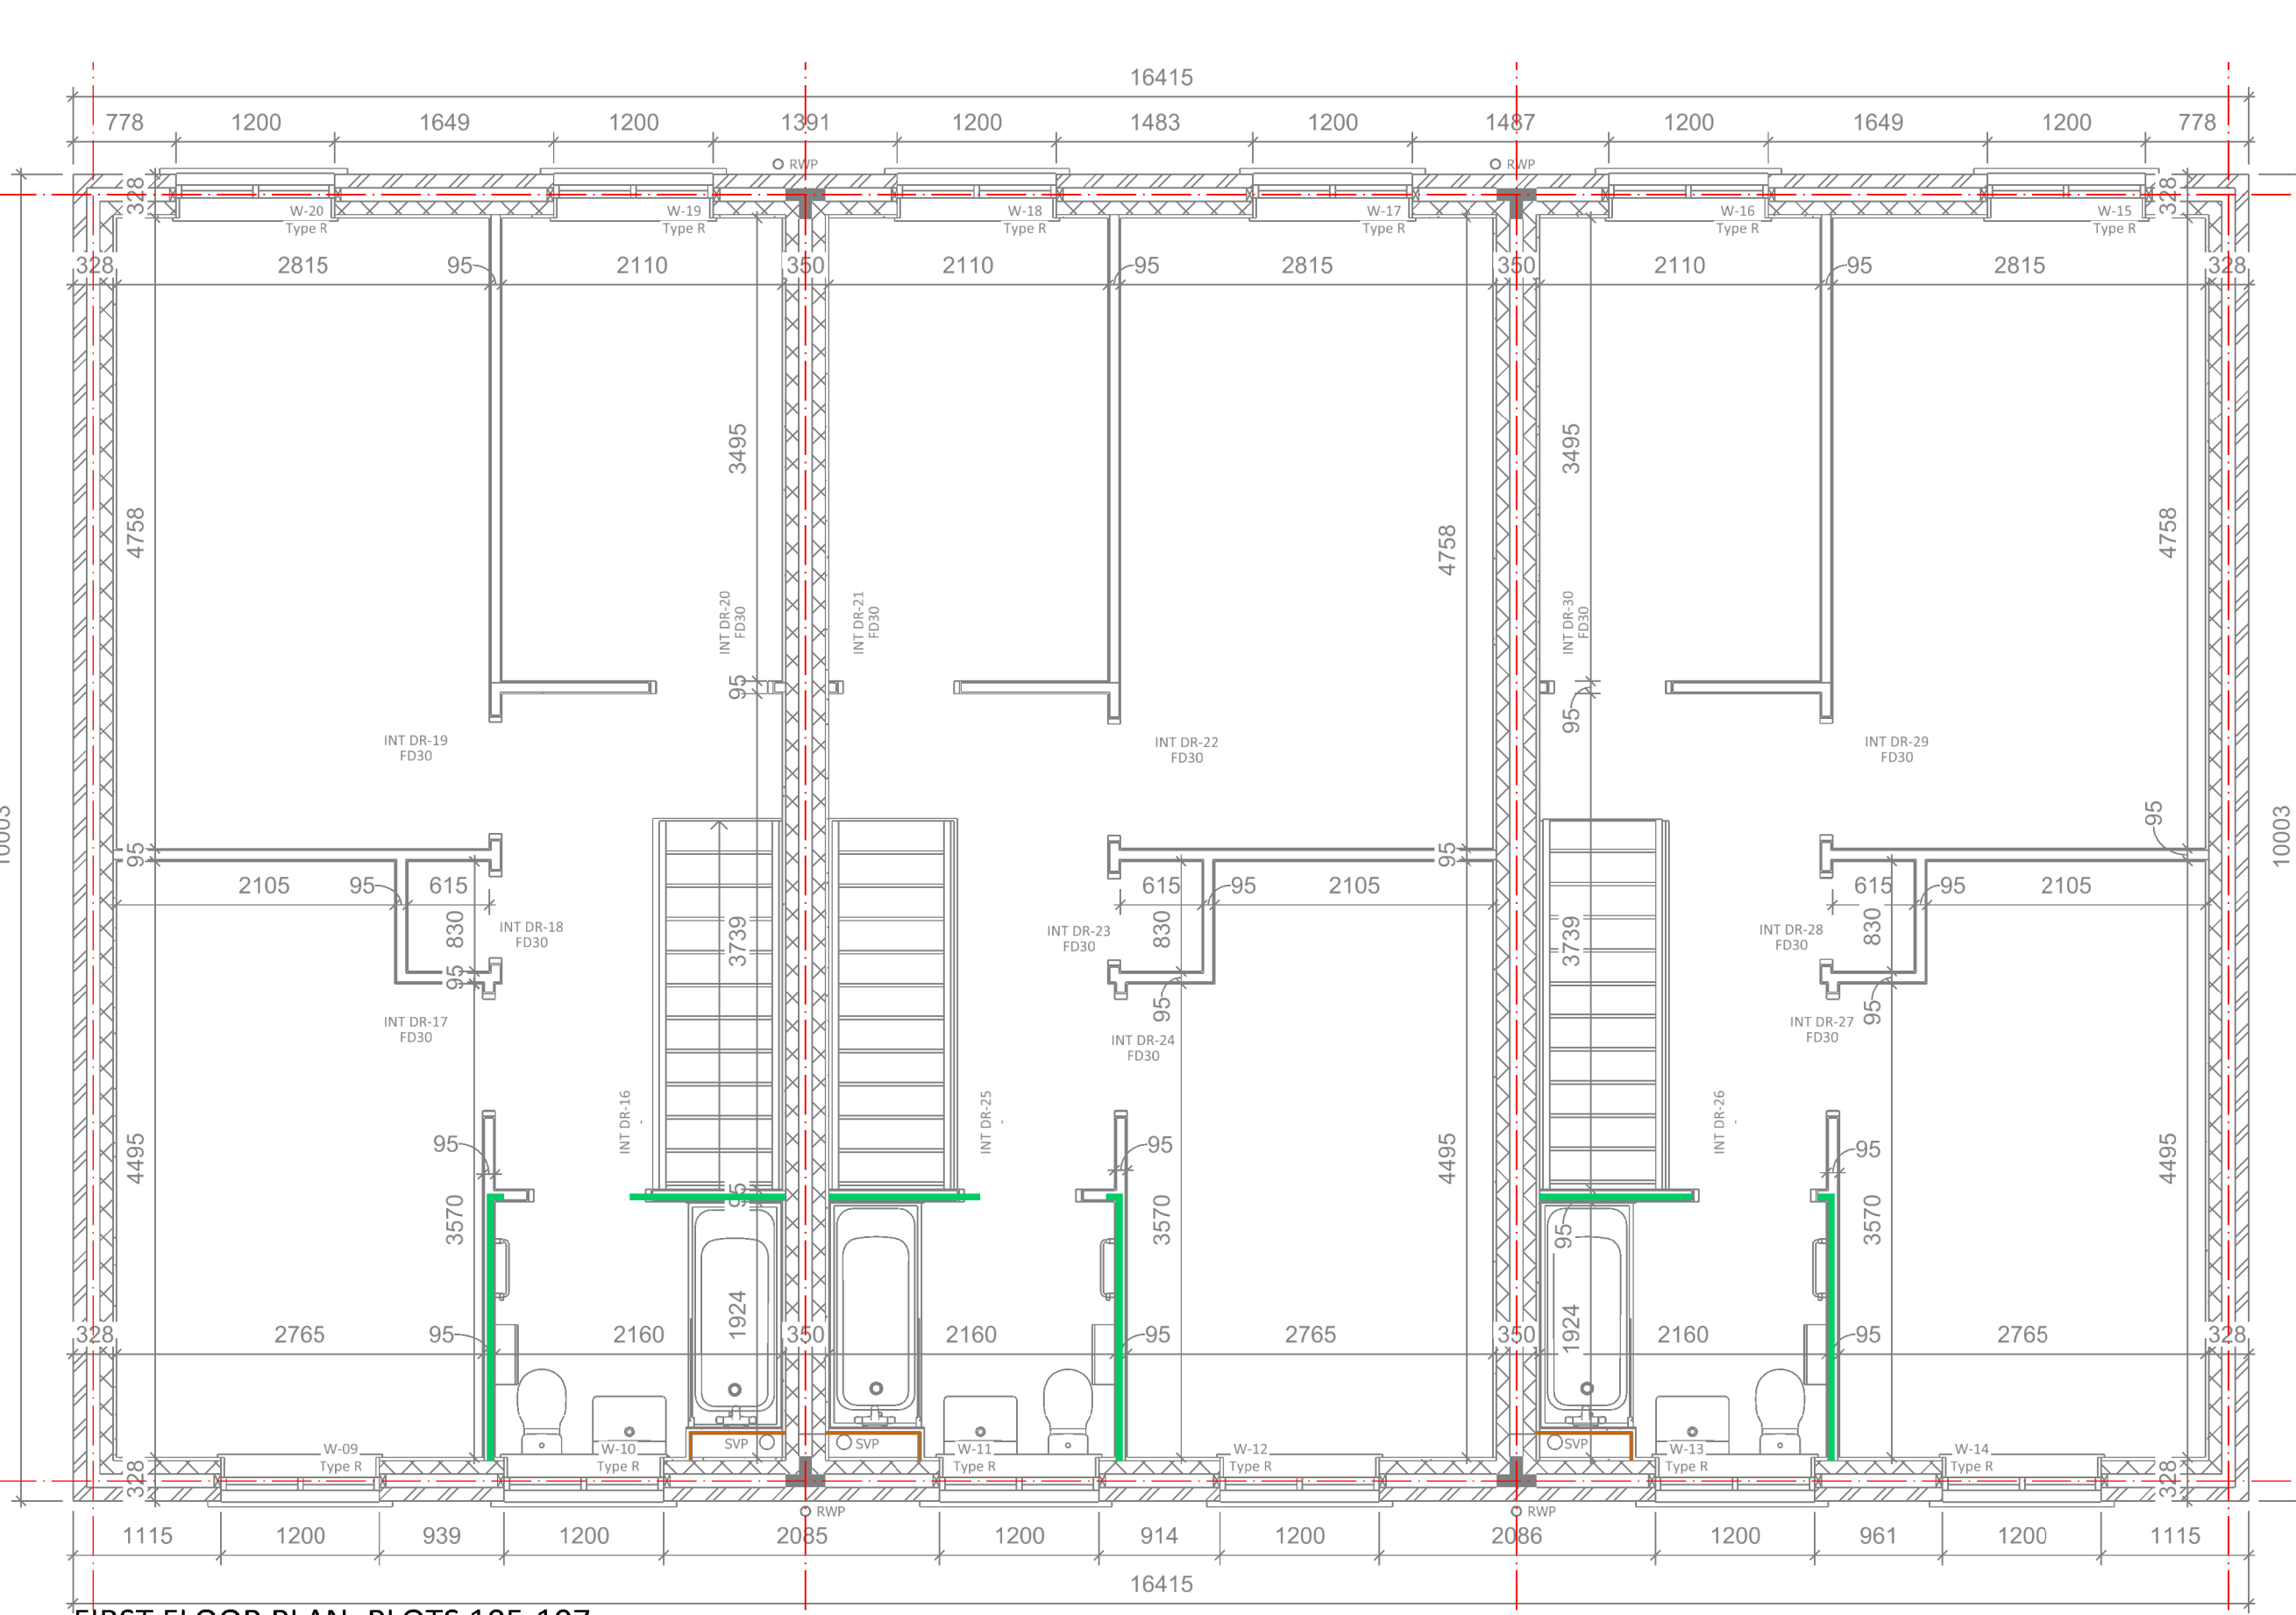

FIRST FLOOR PLAN: PLOTS 105-107

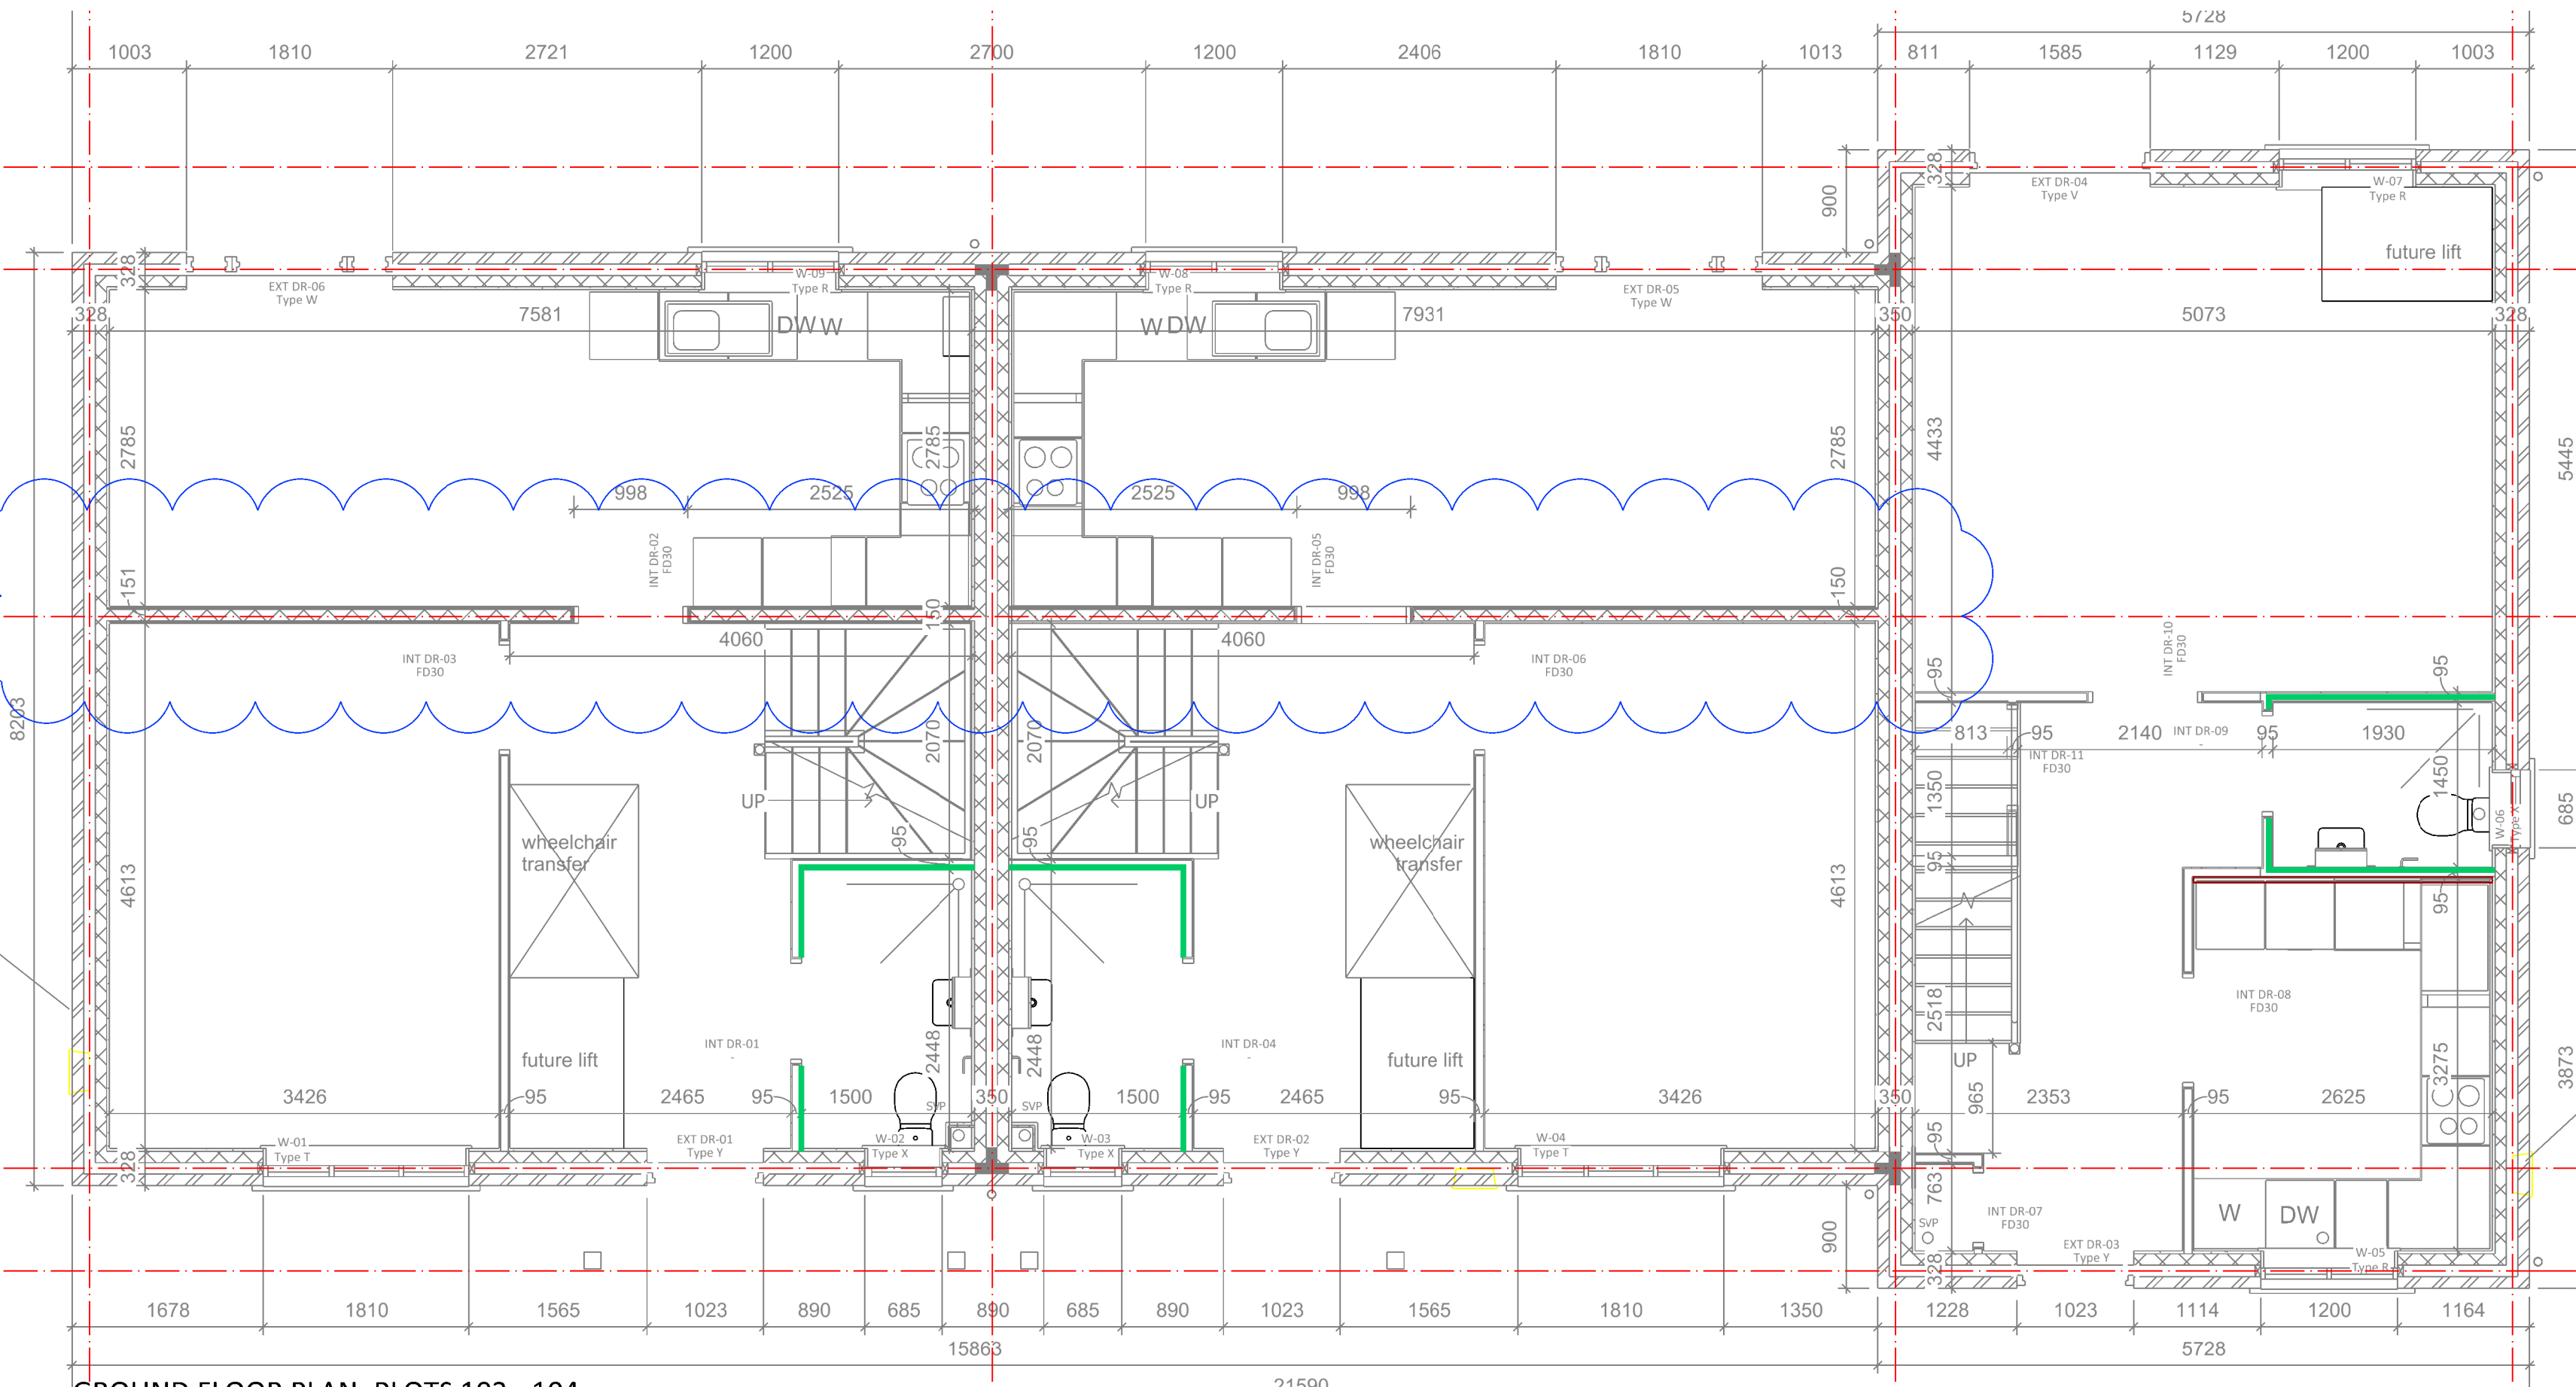

GROUND FLOOR PLAN: PLOTS 102 - 104

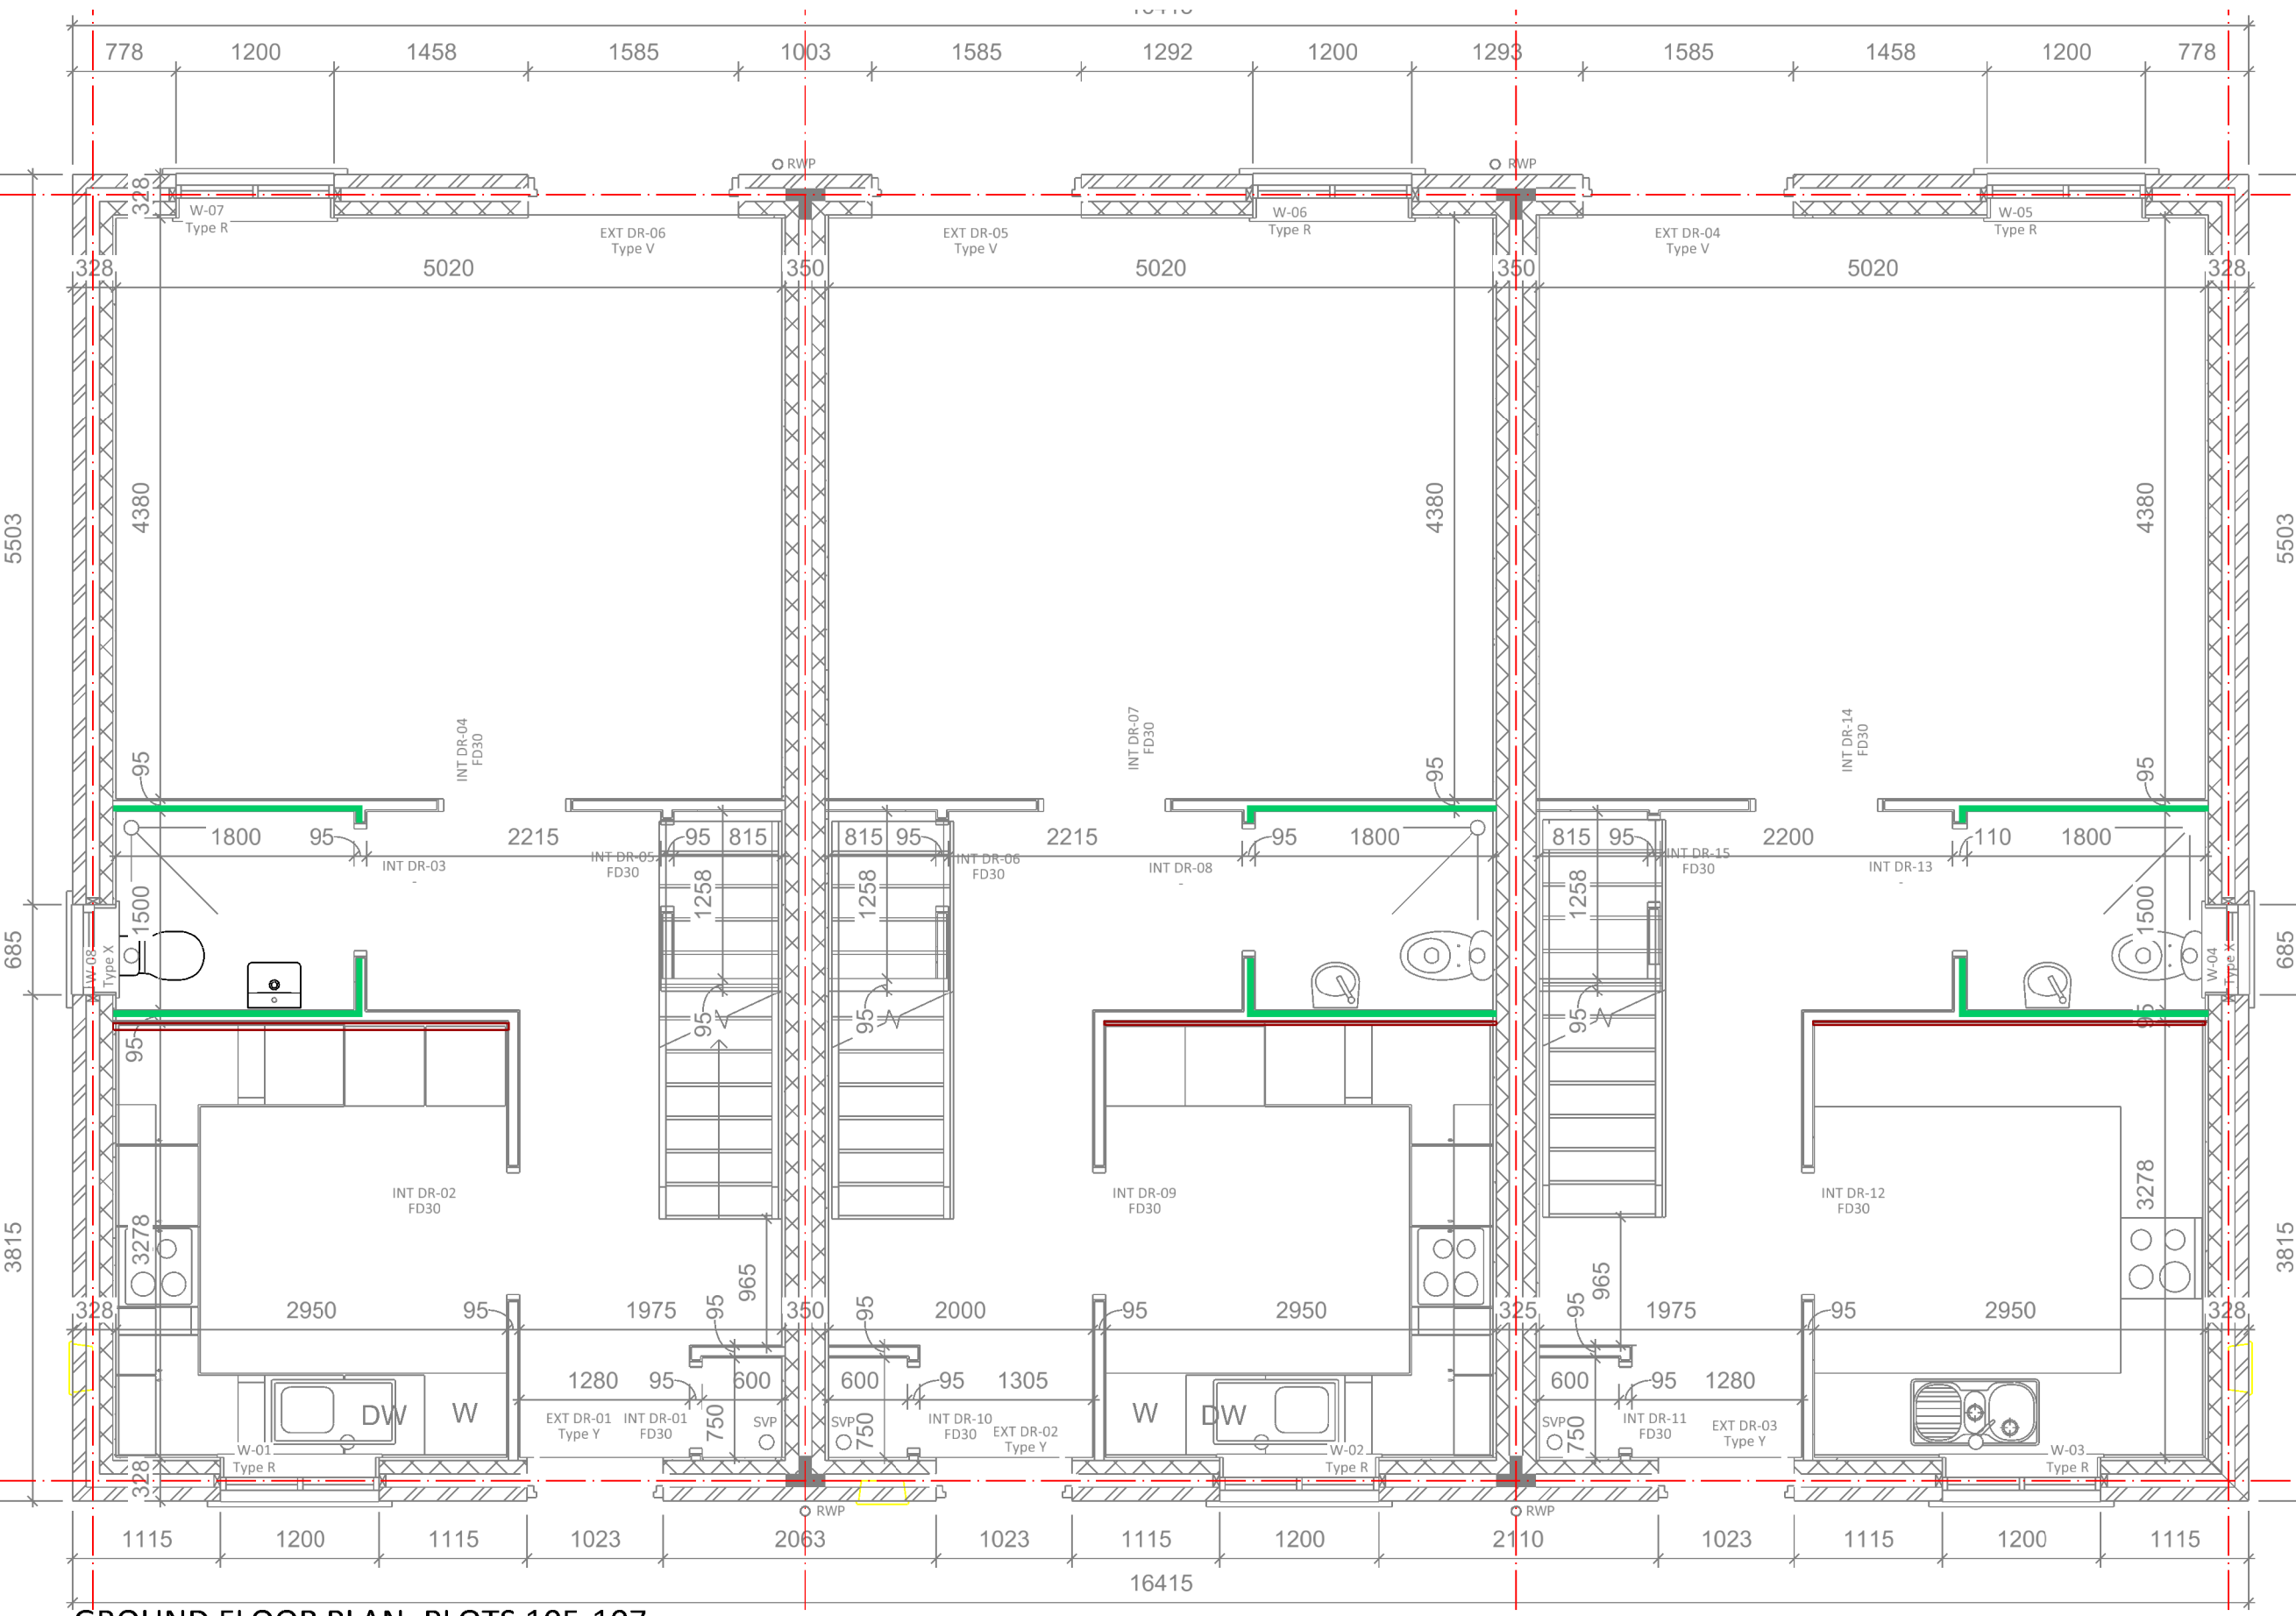

GROUND FLOOR PLAN: PLOTS 105-107

FOR REVIEW / AGREEMENT

NOTES
Do not scale this drawing - use figured dimensions only.
All dimensions are to be checked before implementation.
Any discrepancies are to be advised immediately.
All information is copyright of DLA Architects Practice and may not be used or reproduced without prior permission.

REVISIONS
P2 27/02/2018 Buttress walls removed in line with Rolton's amended details
P3 15/05/2018 Central wall plots 102 & 103 changed to blockwork

PLYWOOD LININGS & PATTERESSES

- PLYWOOD PATTERESSES TO FIXING OF KITCHEN UNITS LOCATED BETWEEN STUDS SET AT HEIGHT TO SUIT KITCHEN WALL UNITS 9mm x 600 high, width to suit studs set at 1500mm height to u/s above FFL
- 15mm OR 9mm T&C PLYWOOD LINING POSITIONED WITHIN PARTITION ON INSIDE OF PLASTERBOARD TO BE FULL HEIGHT OR TO BE FIXED BETWEEN STUDS TO HALF HEIGHT
- 9mm PLYWOOD A MIN 1500mm WIDE REQUIRED FOR BUTTRESS WALLS
- FULL HEIGHT ON INSIDE OF PLASTERBOARD
- 15mm WBP PLYWOOD BEHIND DUCTWORK

CAREYS
GUN HILL DEVELOPMENT ZONE - PHASE 1
TERRACE HOUSES 102 - 107 - PLYWOOD LININGS

DATE	SCALE	STATUS
Jan 2018	1:50	INFORMATION
DRAWING NUMBER	REVISION	
1132-209	P3	

DLA ARCHITECTS PRACTICE
INTEGRATED ARCHITECTURE

50 North Thirteenth Street
CENTRAL MILTON KEYNES, MK9 3BP
T: 01908 259719 F: 01908 605747
email: mail@dla-architects.com

© DLA ARCHITECTS PRACTICE LTD