
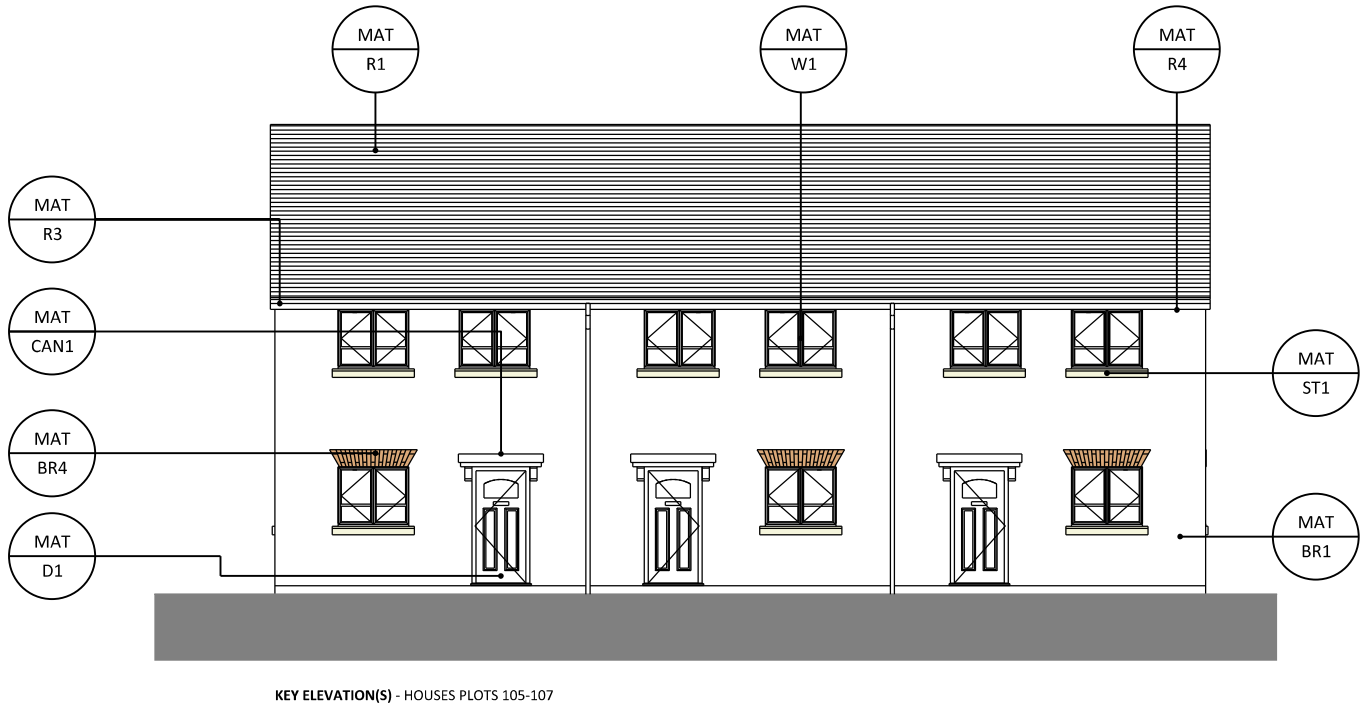


LEGEND To be in conjunction Materials Summary Doc 1132-MAT-SUM & Material Detail drawings 1132-23 - 1132-26		
MATERIAL BR1: Facing brickwork Ibstock Multi-orange 0772 Location(s): ALL unit types	MAT	BR1
MATERIAL BR2: Facing brickwork - projecting plinth detail Ibstock Multi-orange 0772 Location(s): As indicated	MAT	BR2
MATERIAL BR3: Facing brickwork - projecting detail 10mm Ibstock Multi-orange 0772 Location(s): As indicated	MAT	BR3
MATERIAL BR4: Facing brickwork - Splayed Header Detail Ibstock Multi-orange 0772 Location(s): As indicated	MAT	BR4
MATERIAL BR5: Facing brickwork - Soldier Course Detail Ibstock Multi-orange 0772 Location(s): As indicated	MAT	BR5
MATERIAL ST1: GRS (Glass Reinforced Stone) Product Keystone GRS - Portland dry cast Location(s): Window cills as indicated	MAT	ST1
MATERIAL ST2: GRS (Glass Reinforced Stone) Product Keystone GRS - Portland dry cast Location(s): High level coping stones	MAT	ST2
MATERIAL C1: Resin Product WM Boyle - White Painted Location(s): High level cornices	MAT	C1
MATERIAL BAL1: Balcony by specialist fabricator In accordance with Roltons design Location(s): Apartments A, B and C only	MAT	BAL1
MATERIAL CAN1: Canopy by specialist GRP Production Glass Fibre Location(s): Apartments A, B and C only	MAT	CAN1
MATERIAL R1: Natural Spanish Slate - Cupa18 CUPAPIZARRAS Location(s): All Roofs	MAT	R1
MATERIAL R2: Dormer(s) GRP Production Glass Fibre Location(s): As indicated	MAT	R2
MATERIAL R3: Fascia board: White uPVC Location(s): All Roofs	MAT	R3
MATERIAL R4: Gutters & downpipes: Black uPVC Location(s): All Roofs	MAT	R4
MATERIAL W1: Windows & Doors(s) - Aluminium system ALUK 58BW/BD Colour - Grey RAL 7016 Location(s): All units	MAT	W1
MATERIAL D1: Entrance Doors(s) - Composite door system Solidor - London Range Location(s): All Houses (only)	MAT	D1
1132-21-P4	SCALE:NTS	DATE:15/11/2017
All information is copyright of DLA Architects Practice and may not be used or reproduced without prior permission. © COPYRIGHT DLA ARCHITECTS PRACTICE LTD		

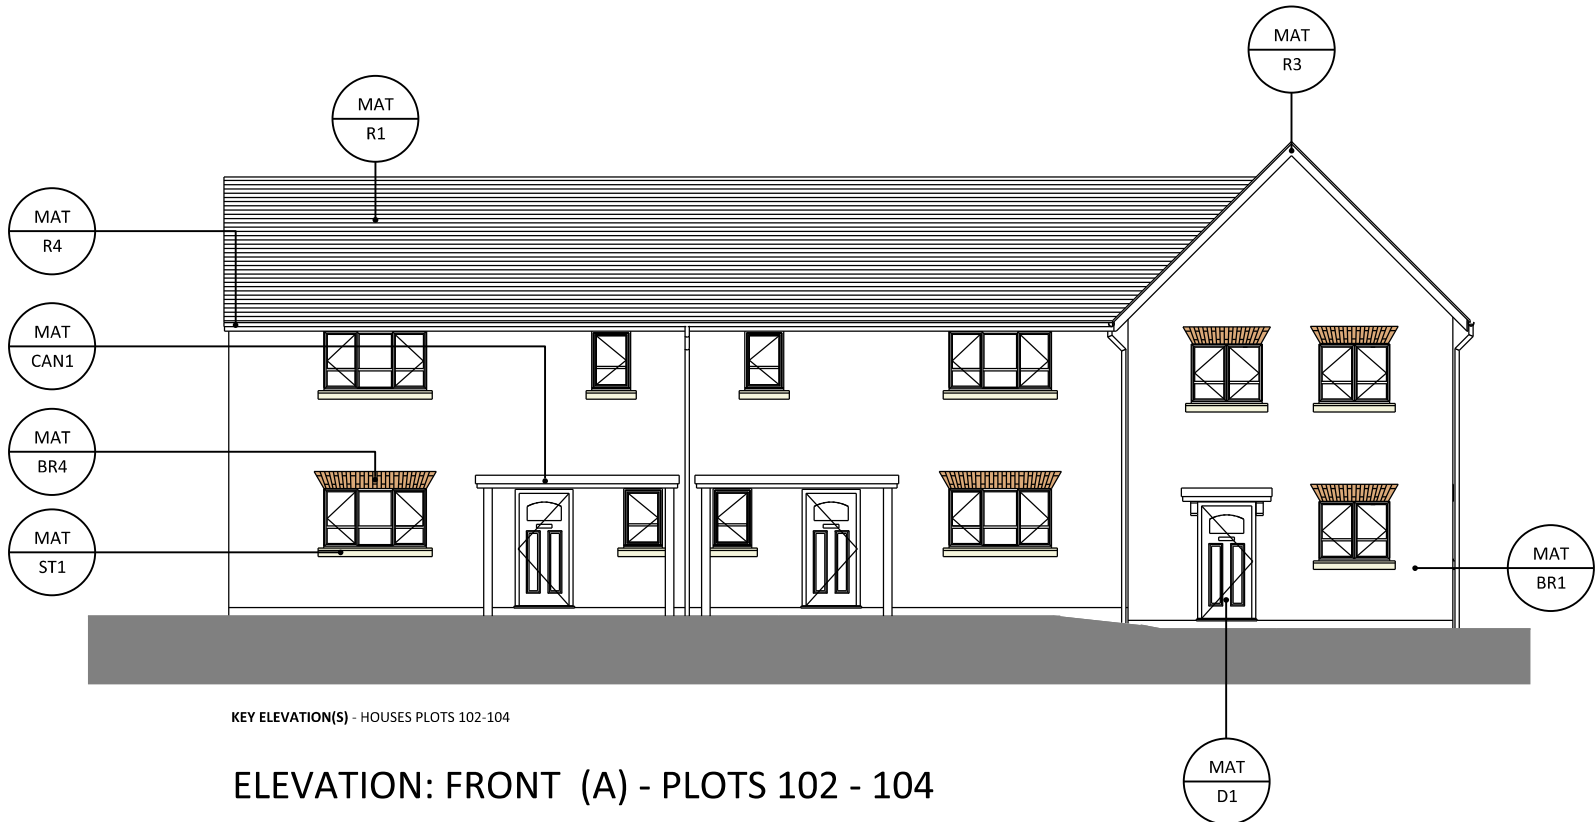

Gunhill - Houses