



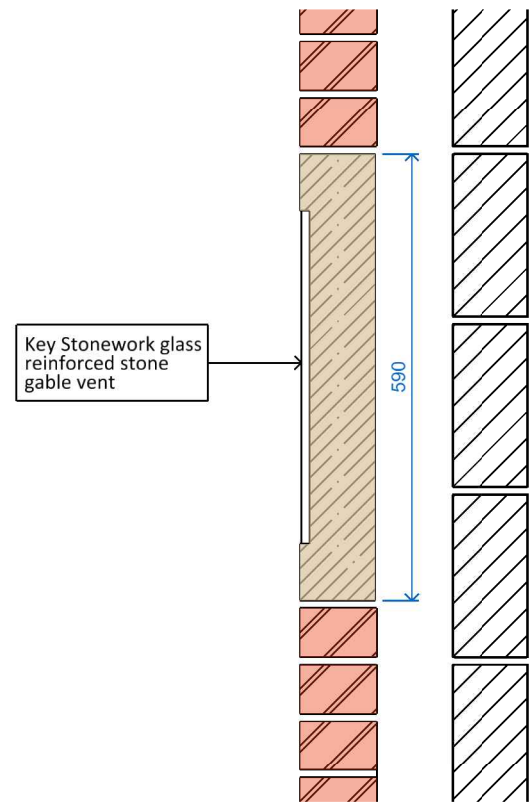


W07 Gable Vent Section
(Scale 1:10 @ A1)

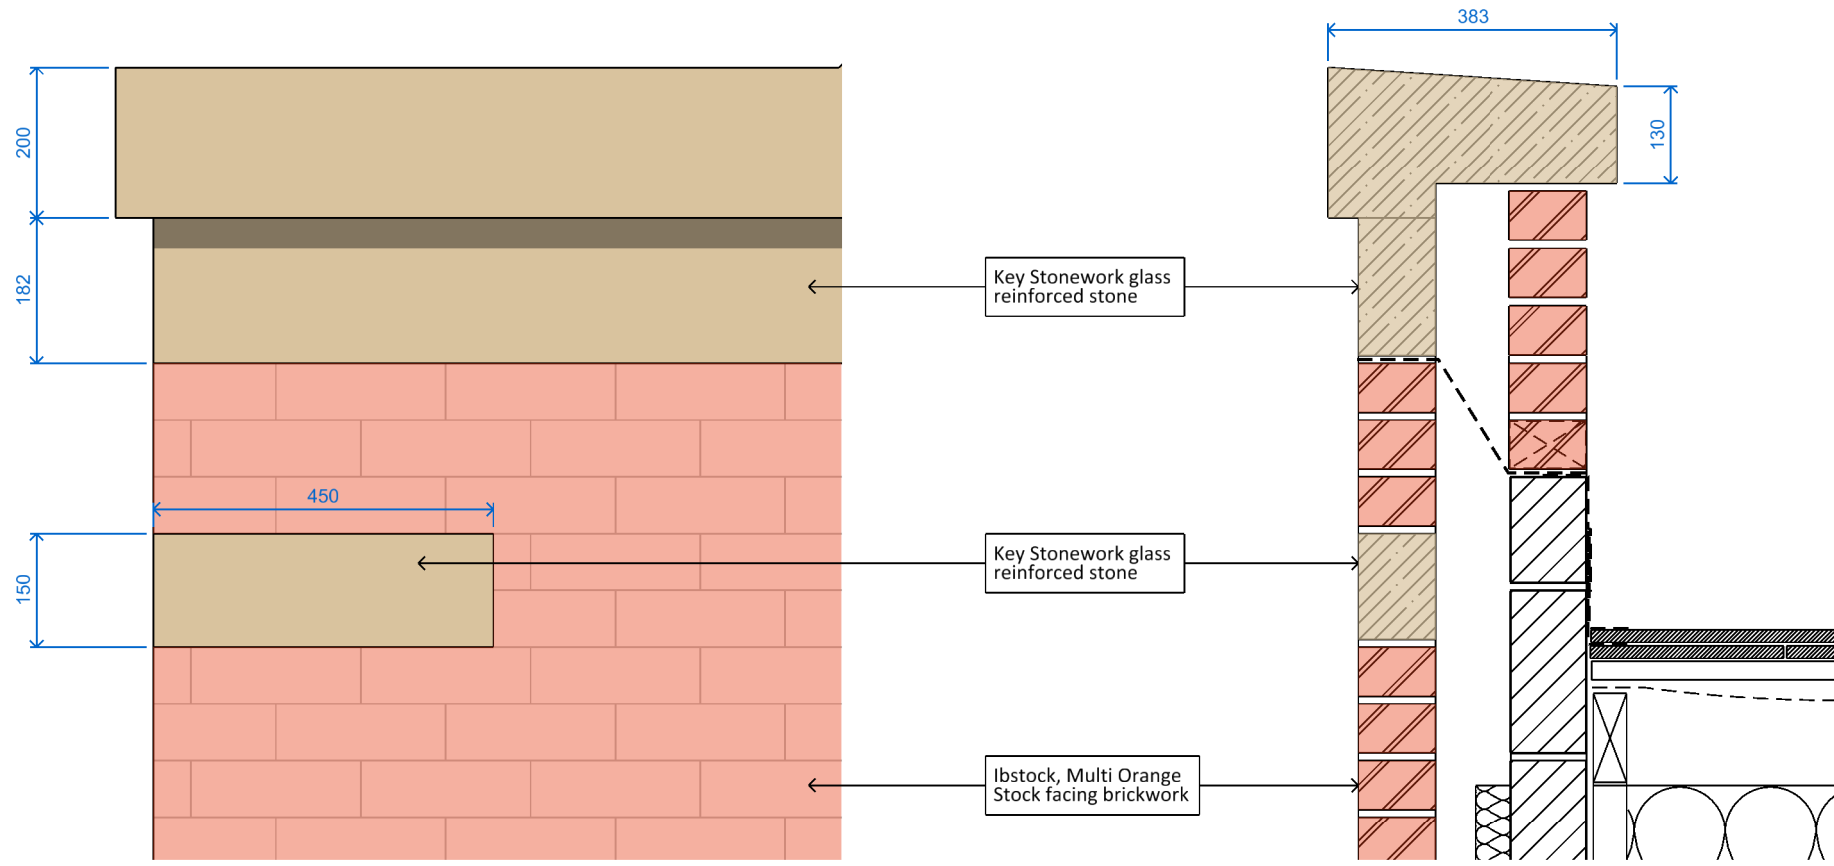


E05 Parapet Coping Elevation
(Scale 1:10 @ A1)

W05 Parapet Coping Section
(Scale 1:10 @ A1)

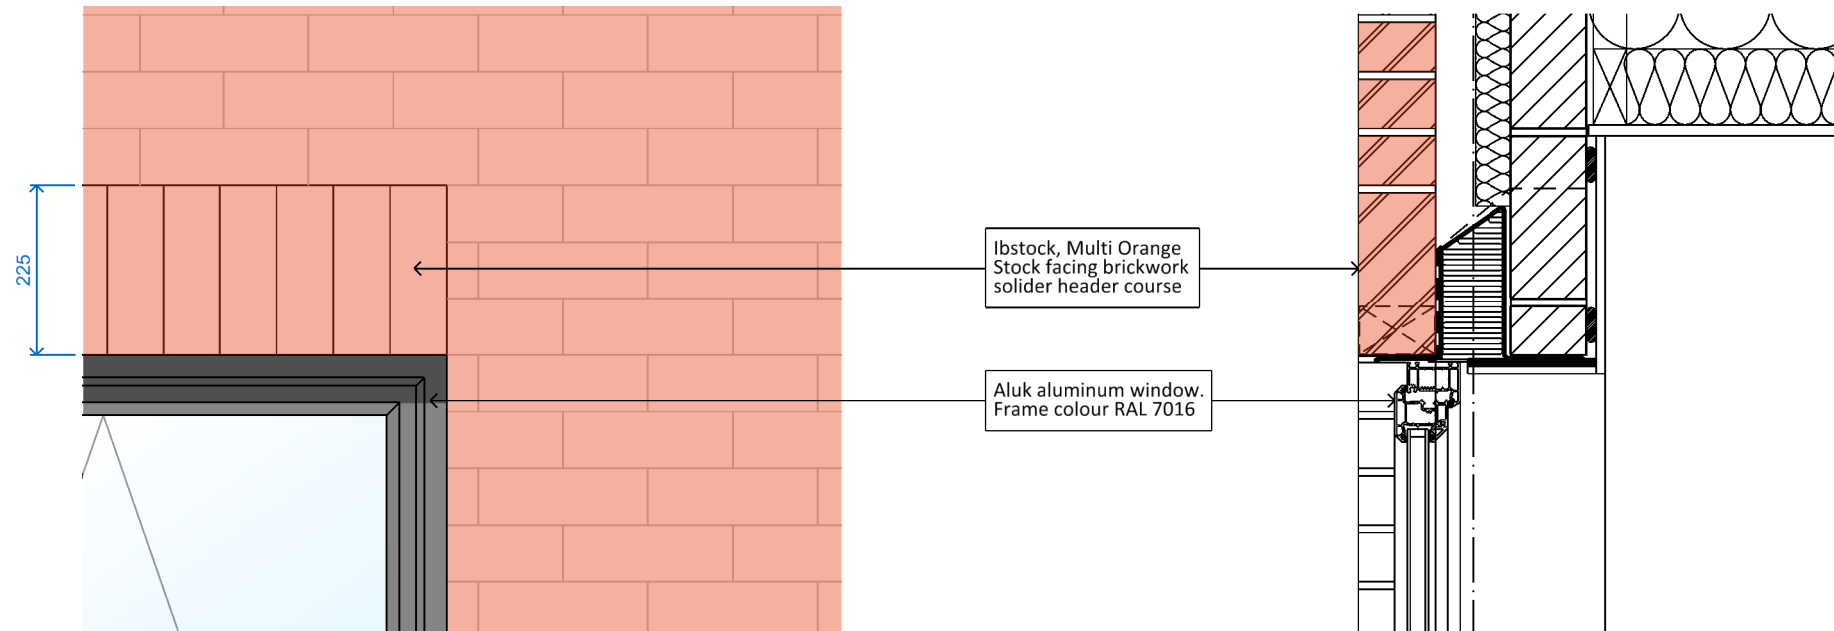


E04 Window Head Elevation
(Scale 1:10 @ A1)

W04 Window Head Section
(Scale 1:10 @ A1)

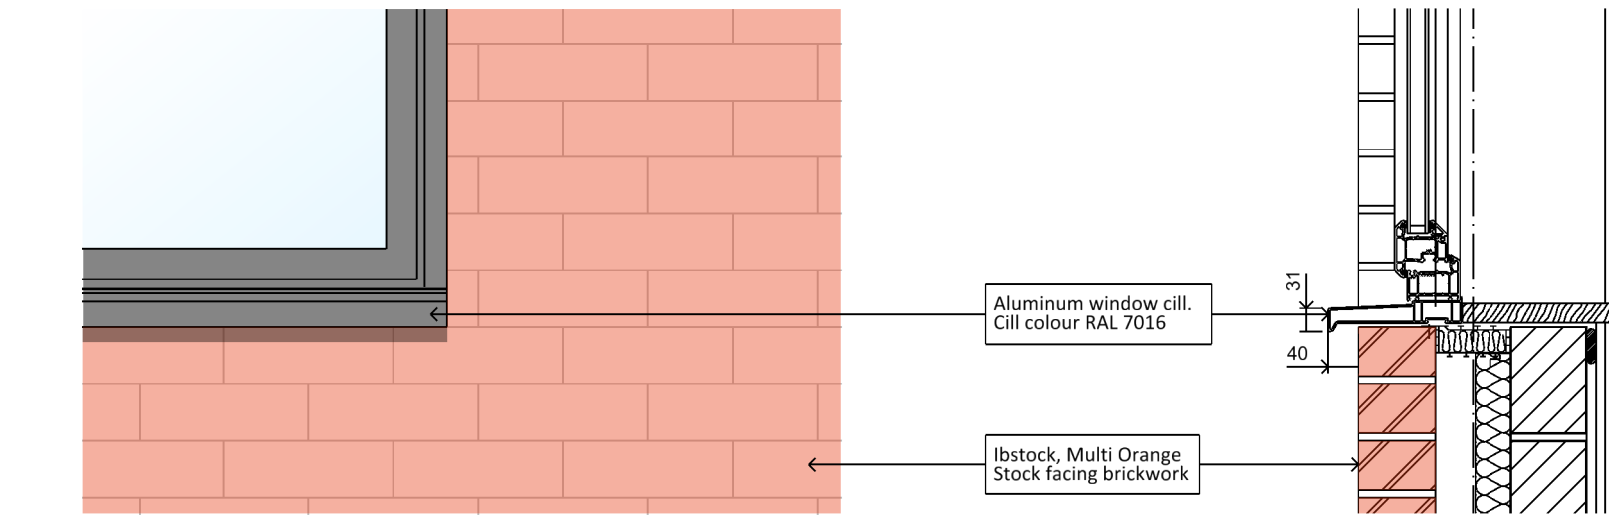


E03 Window Cill Elevation
(Scale 1:10 @ A1)

W03 Window Cill Section
(Scale 1:10 @ A1)

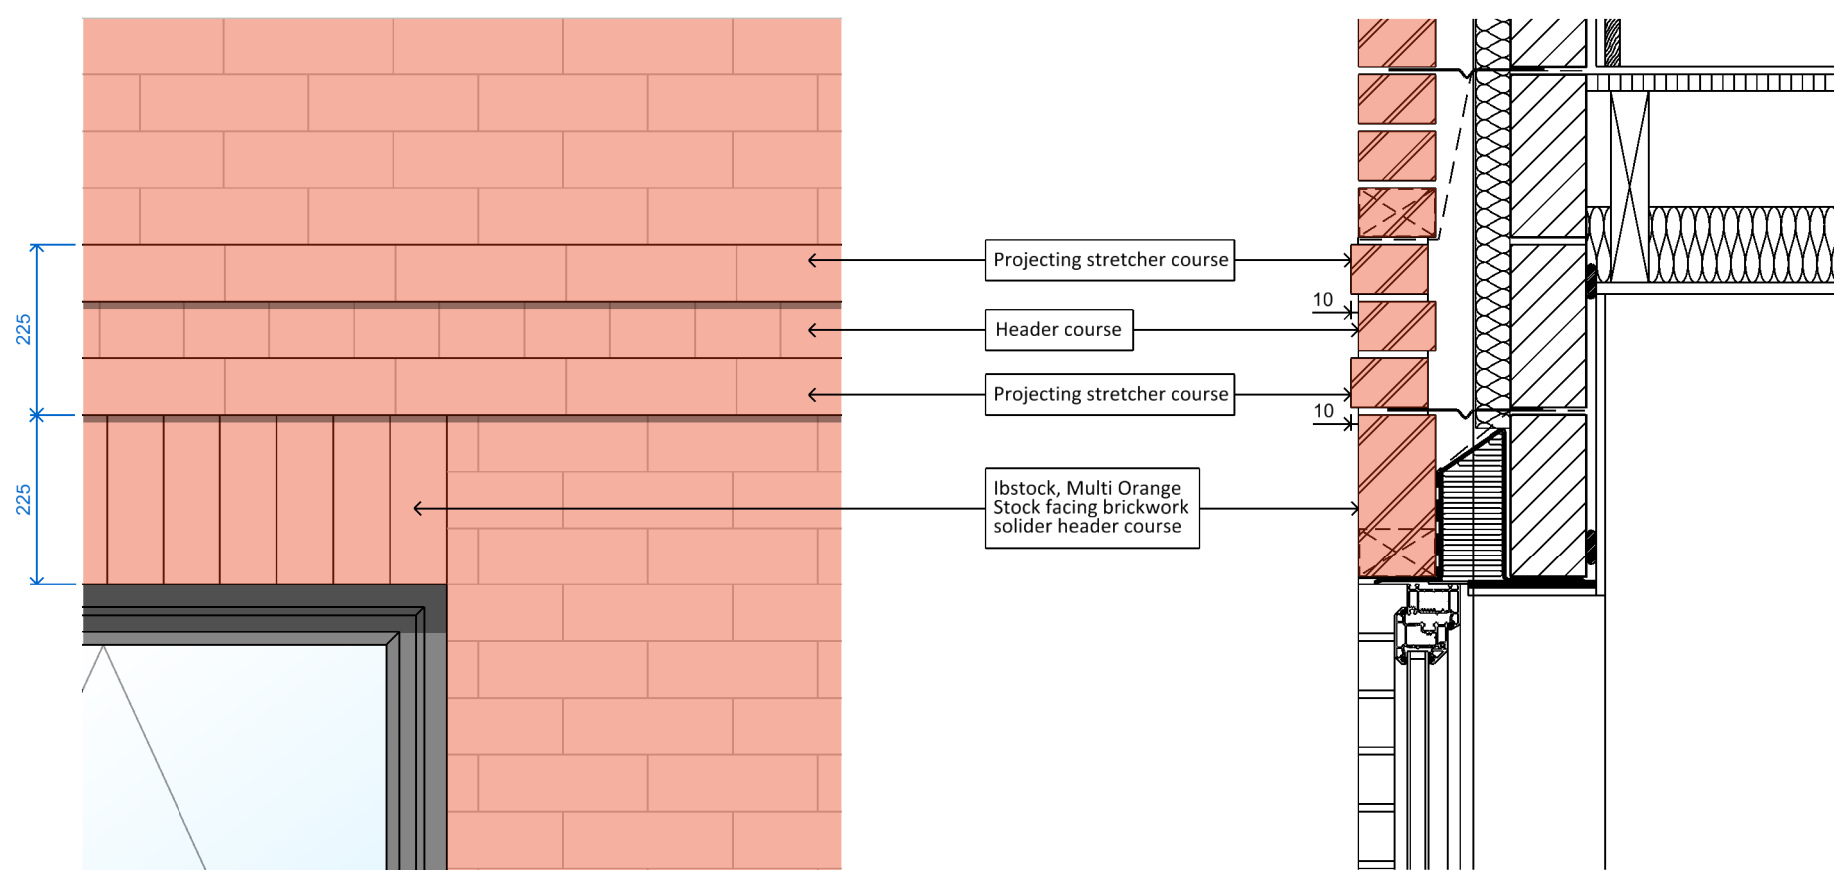


E02 Projecting Brick Band Elevation
(Scale 1:10 @ A1)

W02 Projecting Brick Band Section
(Scale 1:10 @ A1)

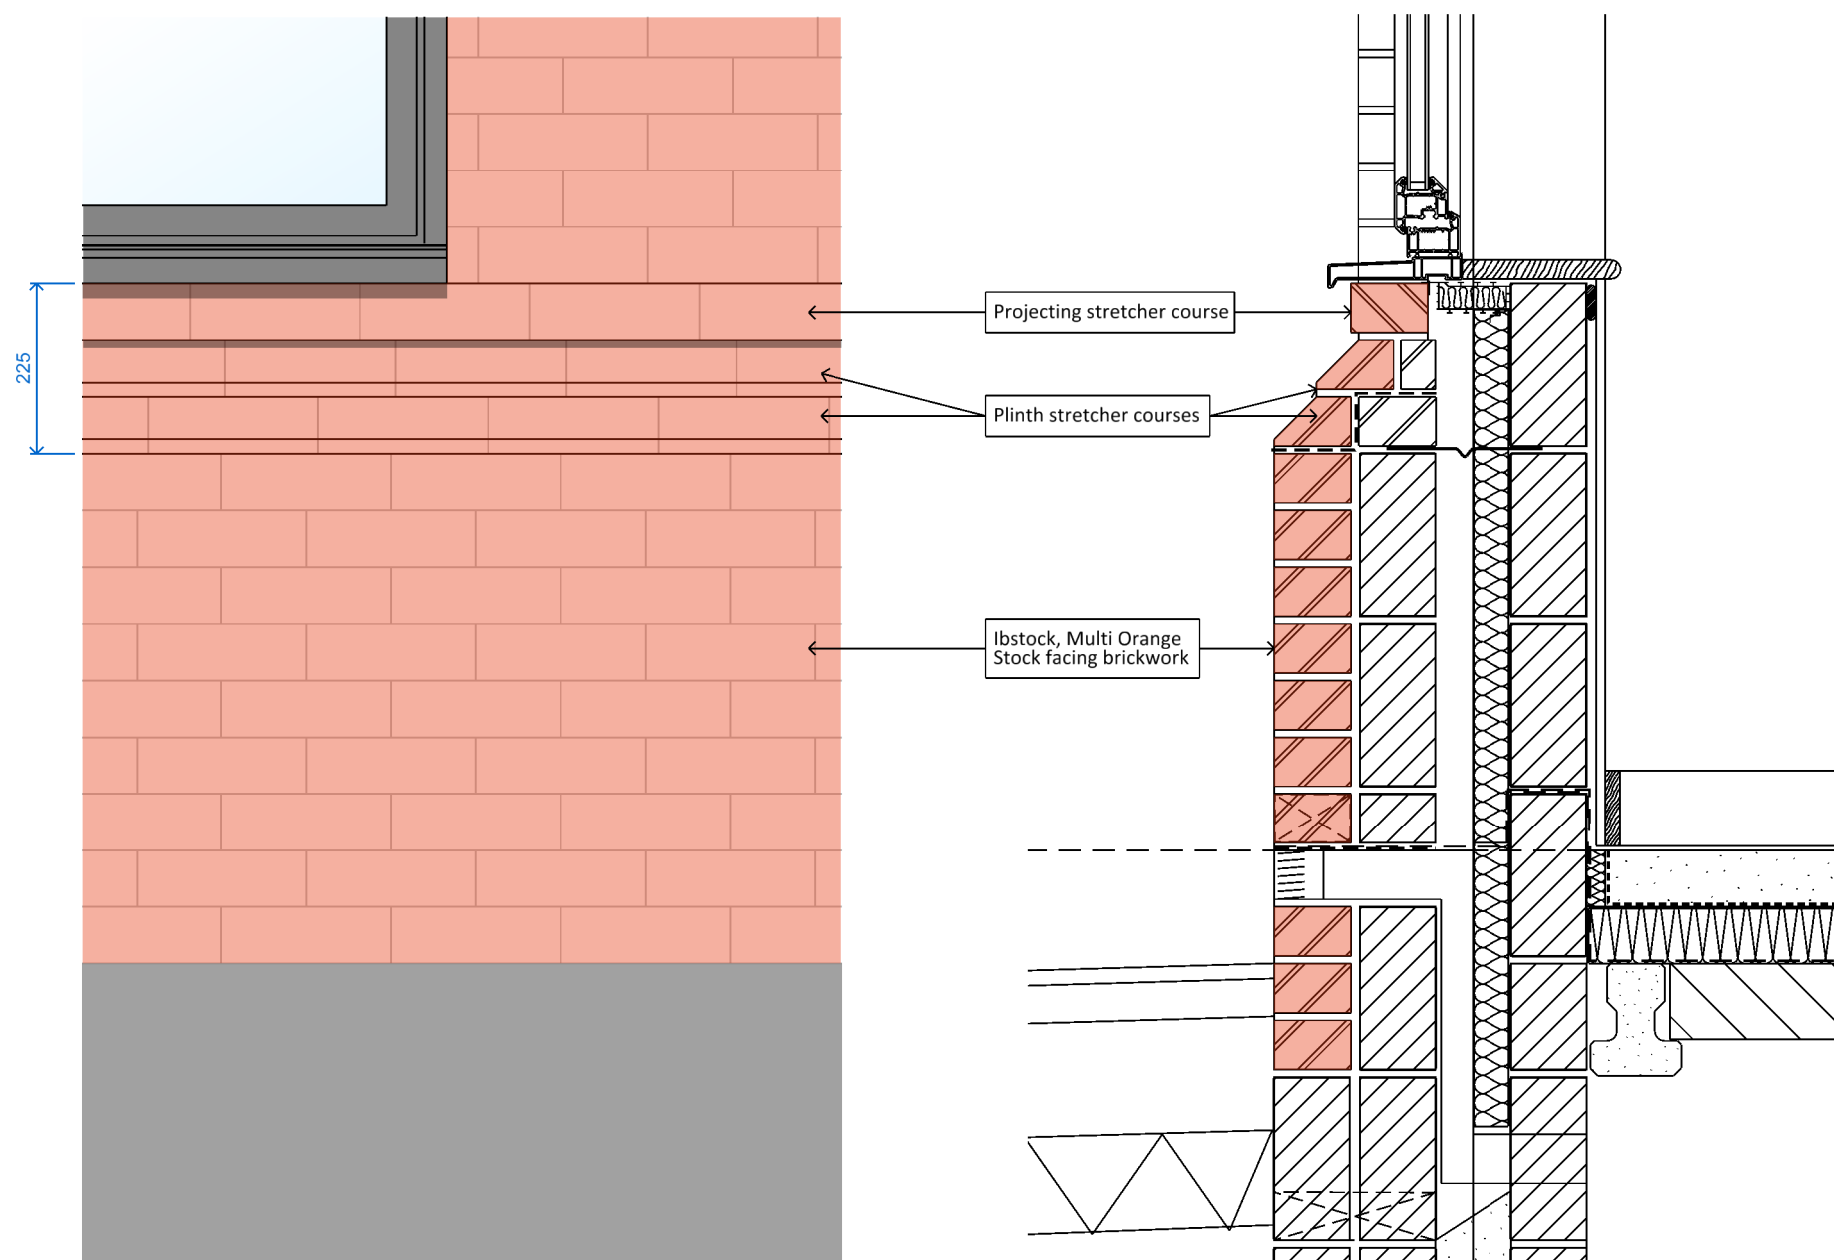

E01 Ground Floor Plinth Elevation
(Scale 1:10 @ A1)

W01 Ground Floor Plinth Section
(Scale 1:10 @ A1)

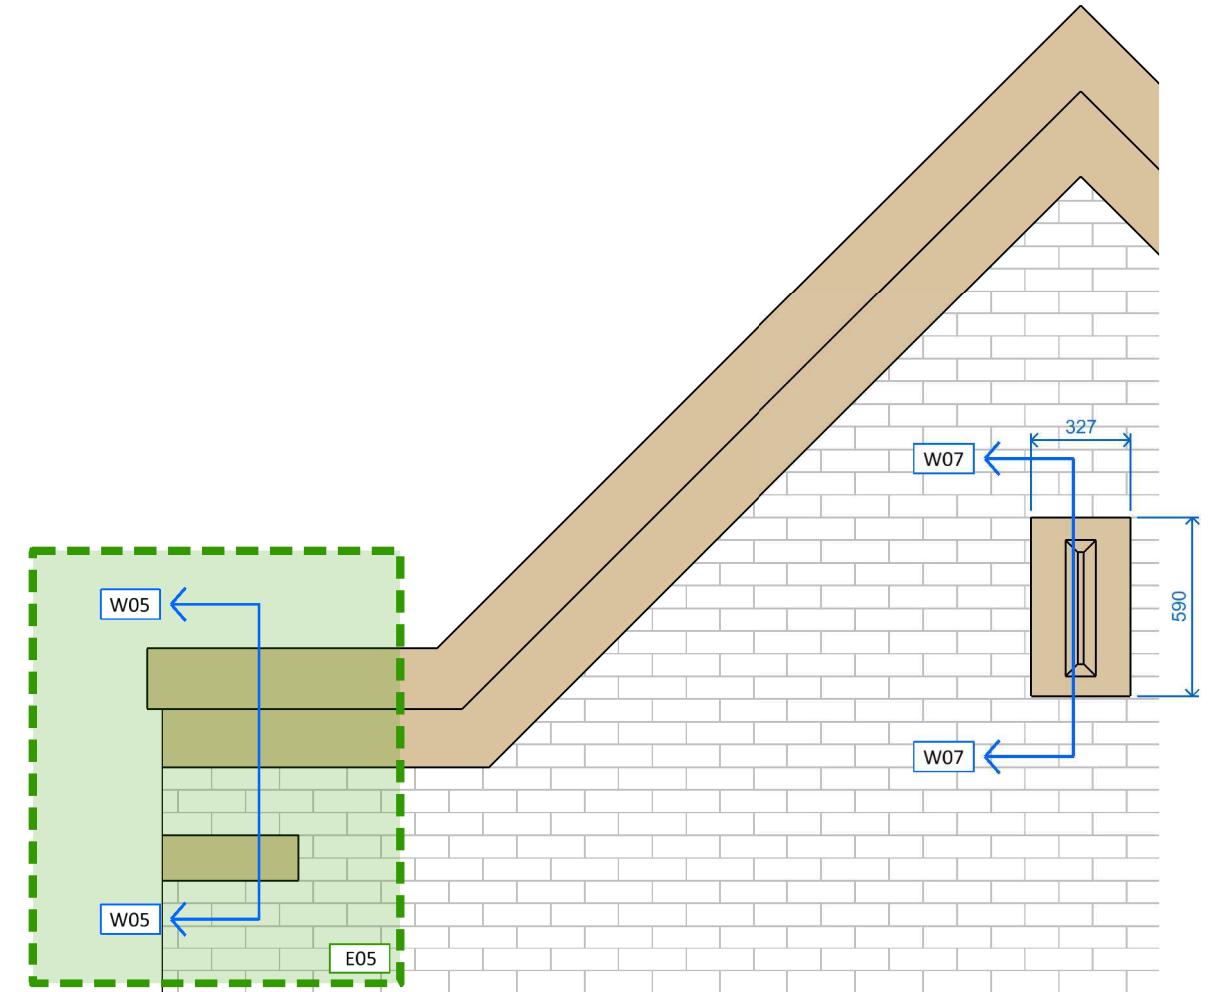

Front Elevation Part
(Scale 1:25 @ A1)



Front Elevation to House Plots:
79-80, 83-84, 87-88 & 90-91
(Scale 1:100 @ A1)

NOTES
Do not scale this drawing - use figured dimensions only. All dimensions are to be checked before implementation. Any discrepancies are to be advised immediately. All information is copyright of DLA Architects Practice and may not be used or reproduced without prior permission.

REVISIONS
P1 15/11/2017 Issued for approval.

Key:
All brickwork:
Ibstock, Multi Orange Stock 0772

Note:
Drawing to be read in conjunction with Materials Summary (1132-MAT-SUM) & Material Treatment Drawings (1132-20 - 1132-22)

CAREYS
GUN HILL, PRS, ALDERSHOT
MATERIAL DETAILS: SEMI HOUSES - SHEET 1
DATE NOV 2017
DRAWING NUMBER 1132-23
SCALE 1:10 & 1:25 @ A1
REVISION P1
STATUS PLANNING

DLA ARCHITECTS PRACTICE
INTEGRATED ARCHITECTURE
50 North Thirteenth Street
CENTRAL MILTON KEYNES, MK9 3BP
T: 01908 259719 F: 01908 605747
email: mail@dla-architects.com
© DLA ARCHITECTS PRACTICE LTD