

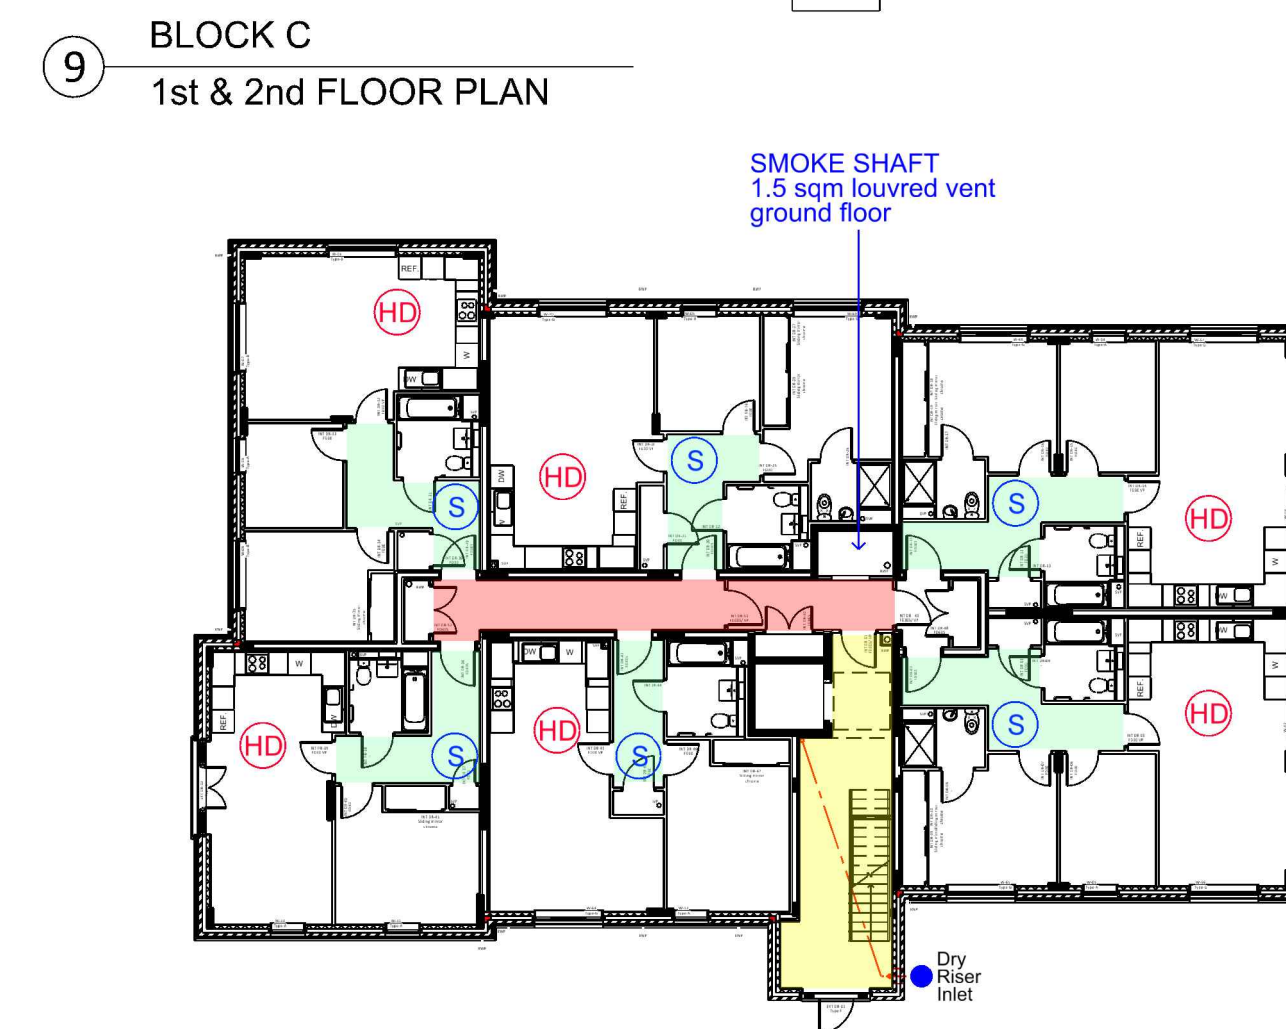
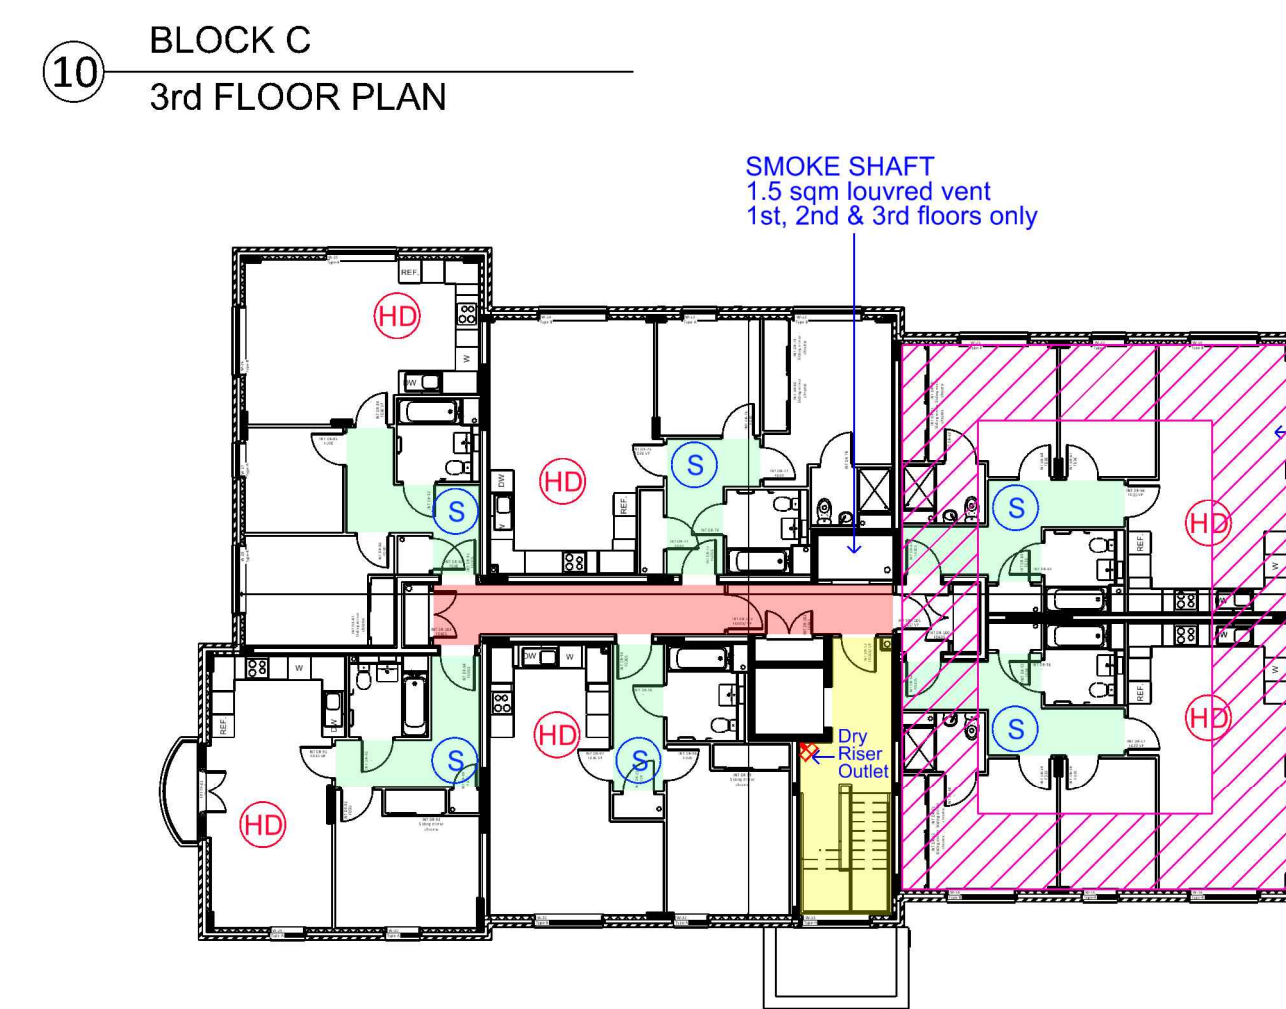
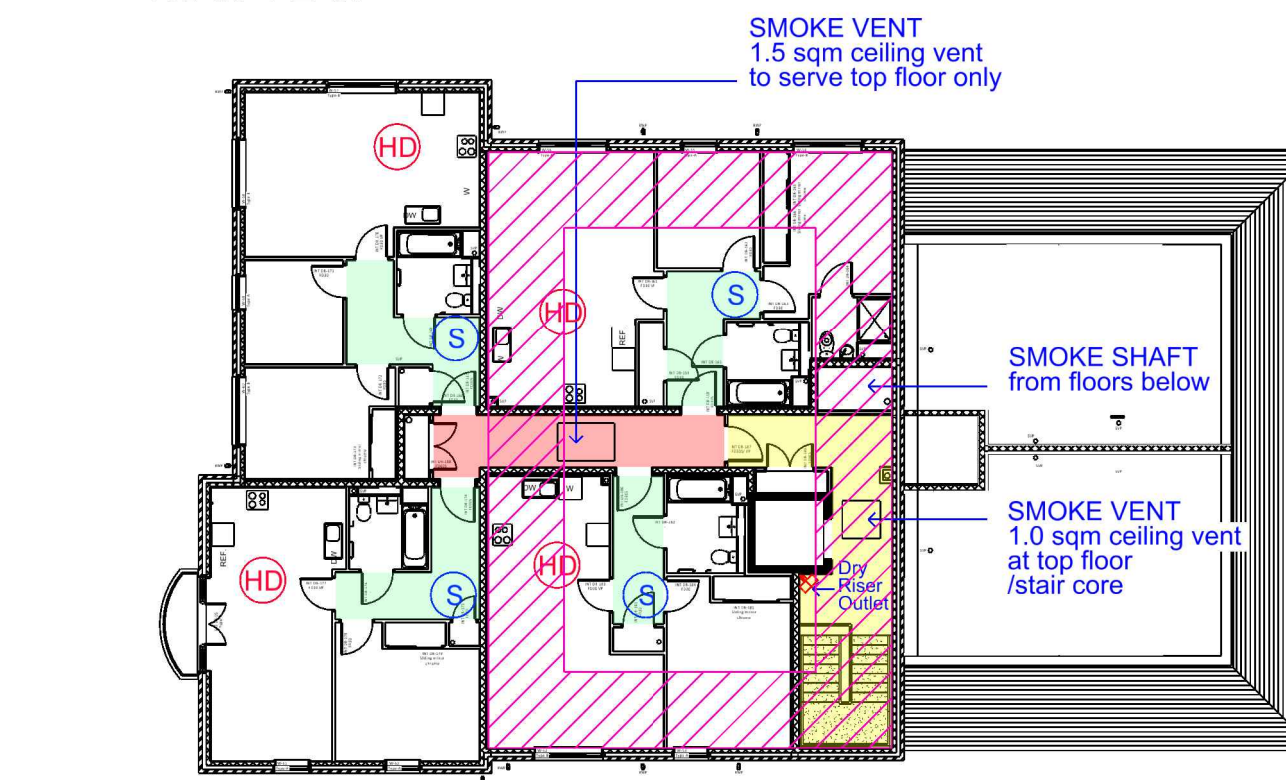
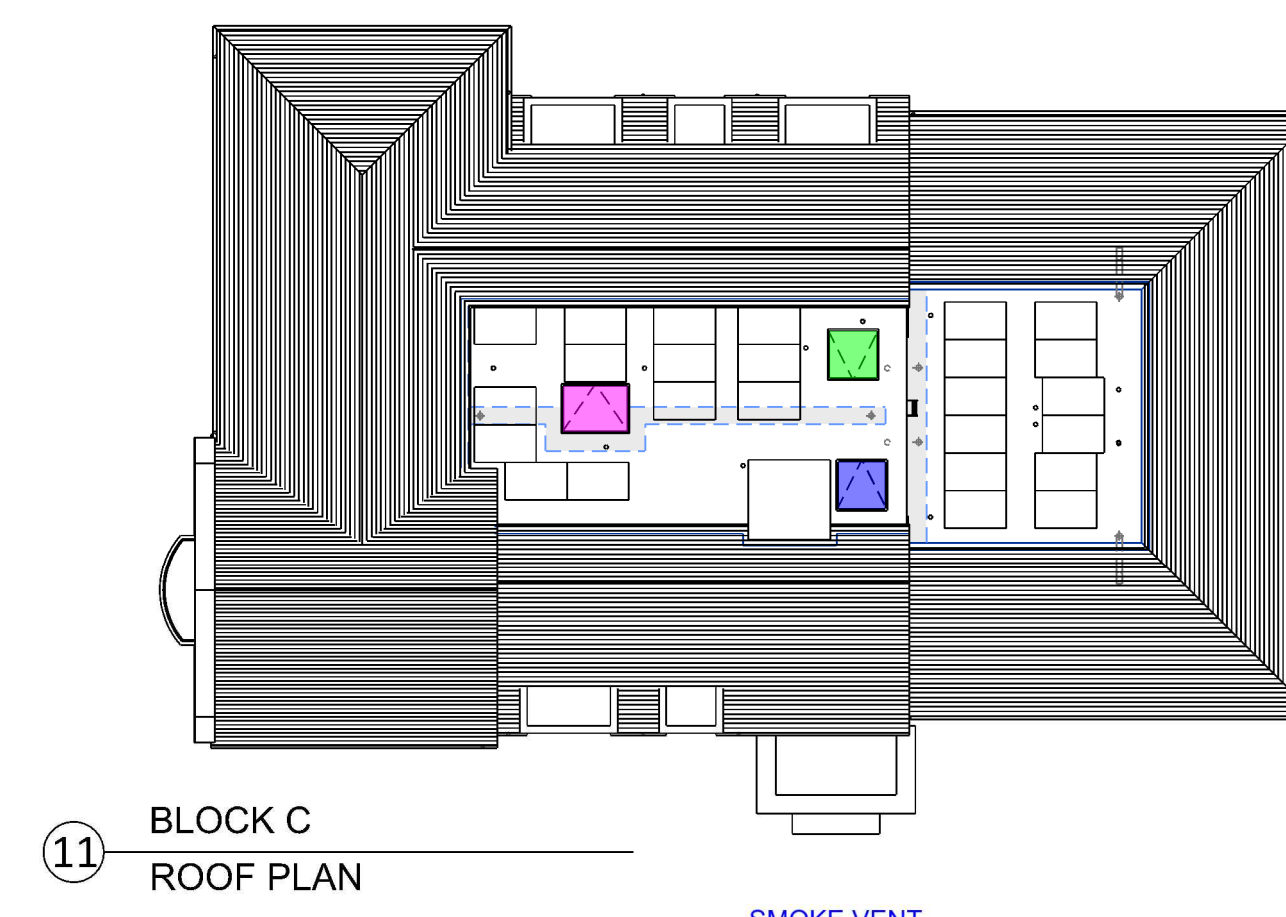
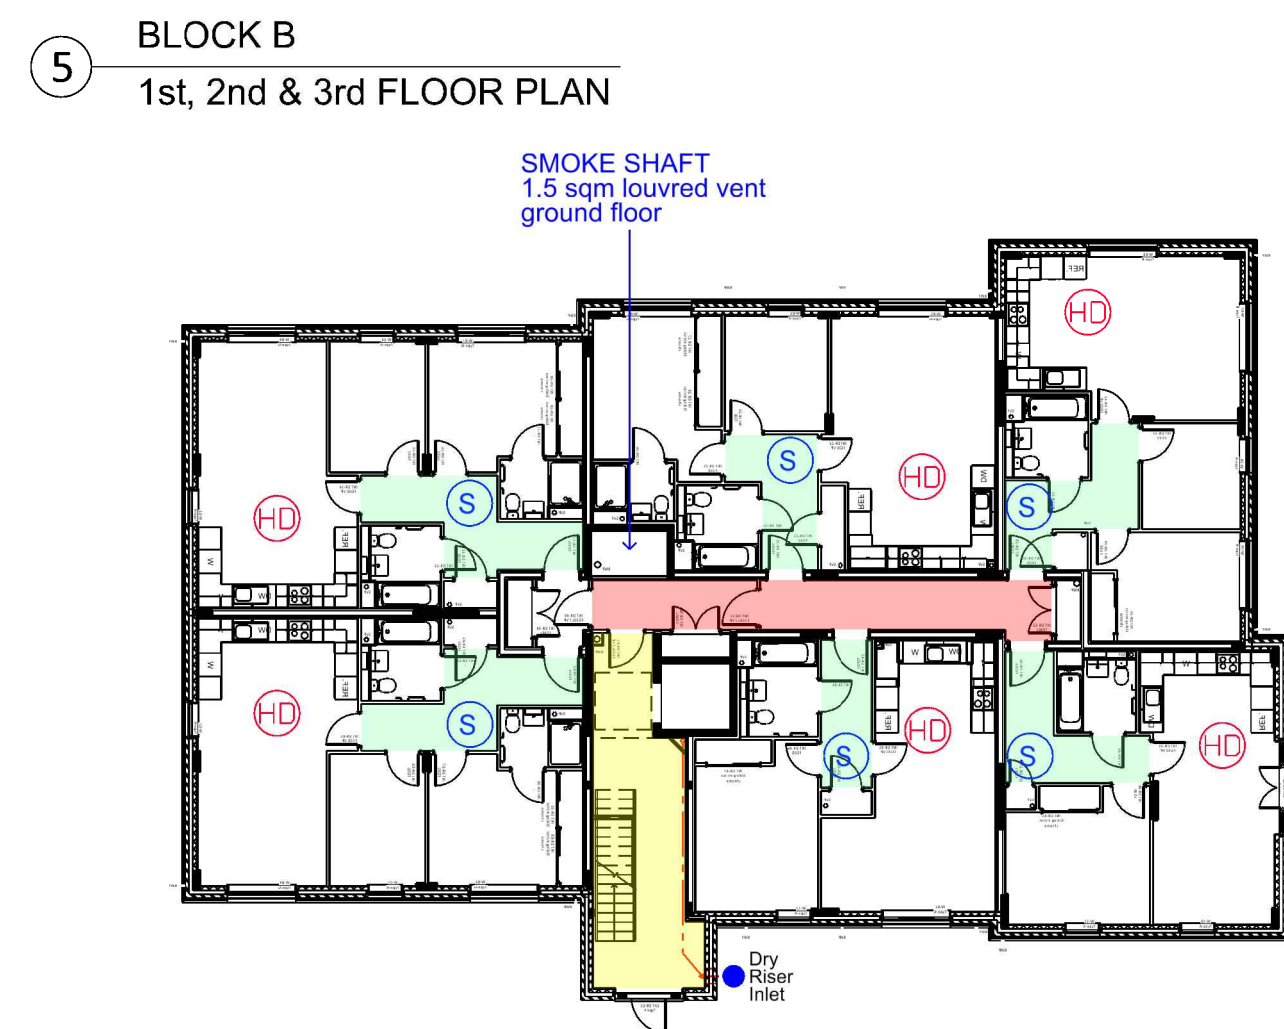
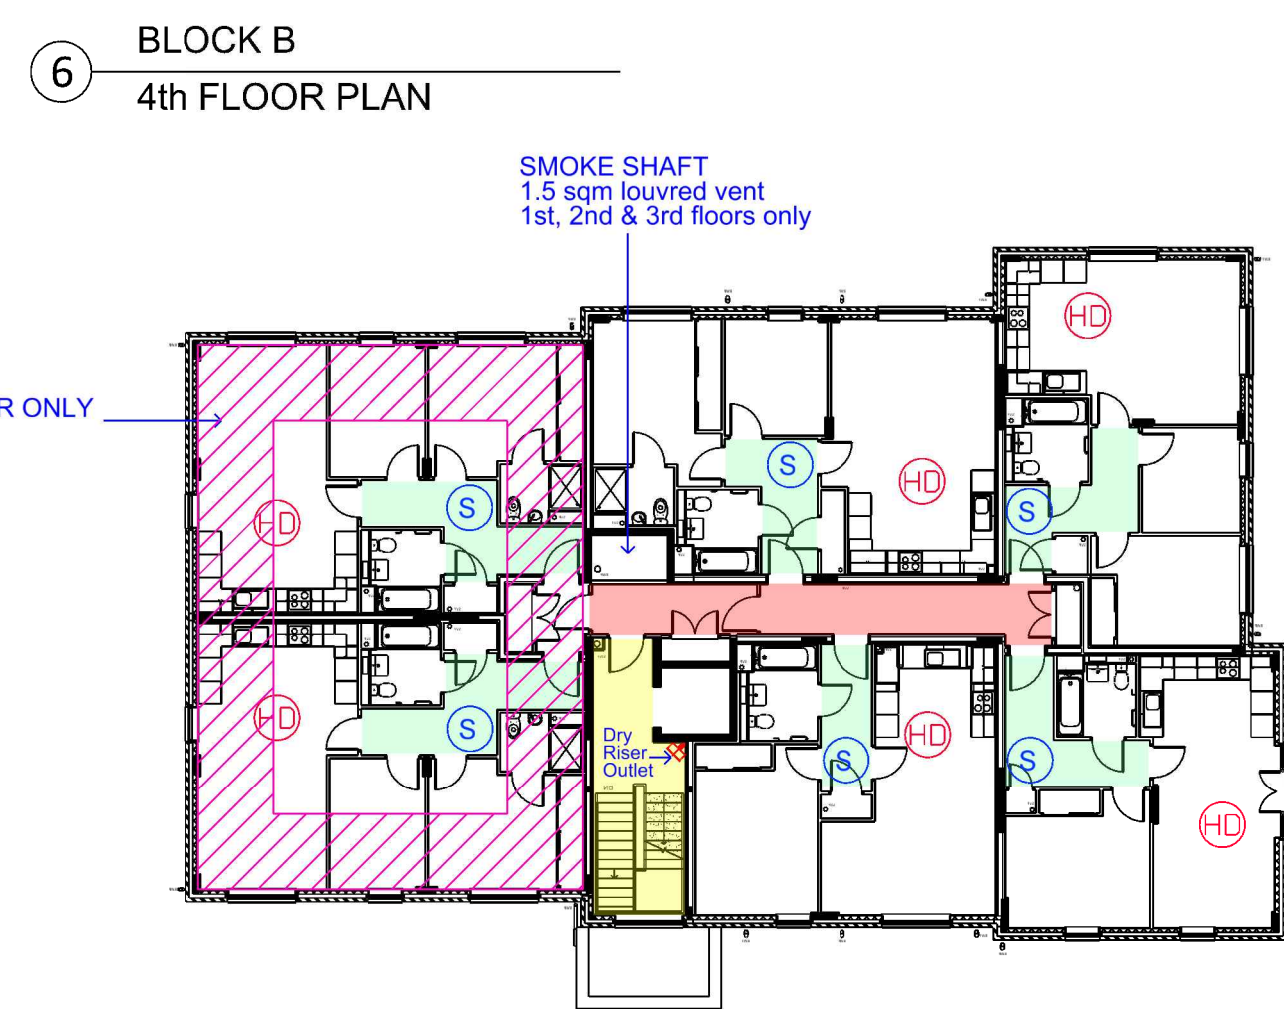
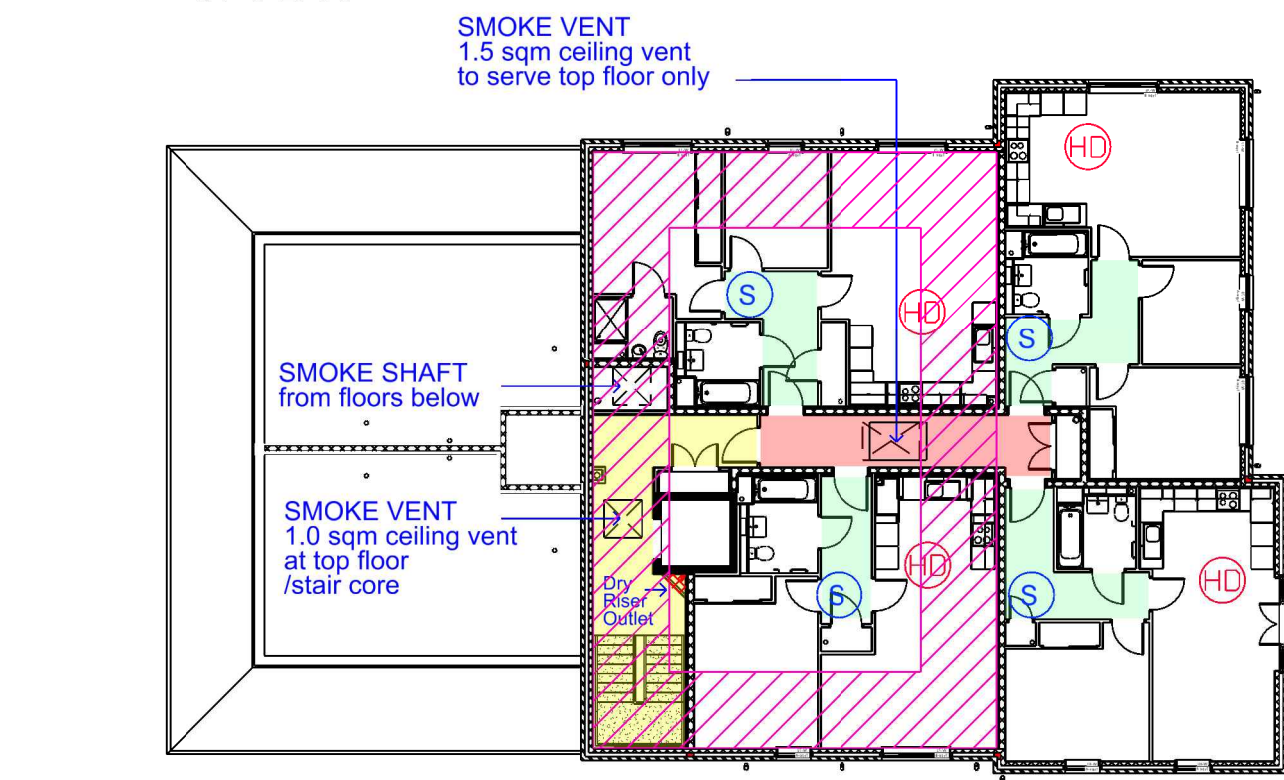
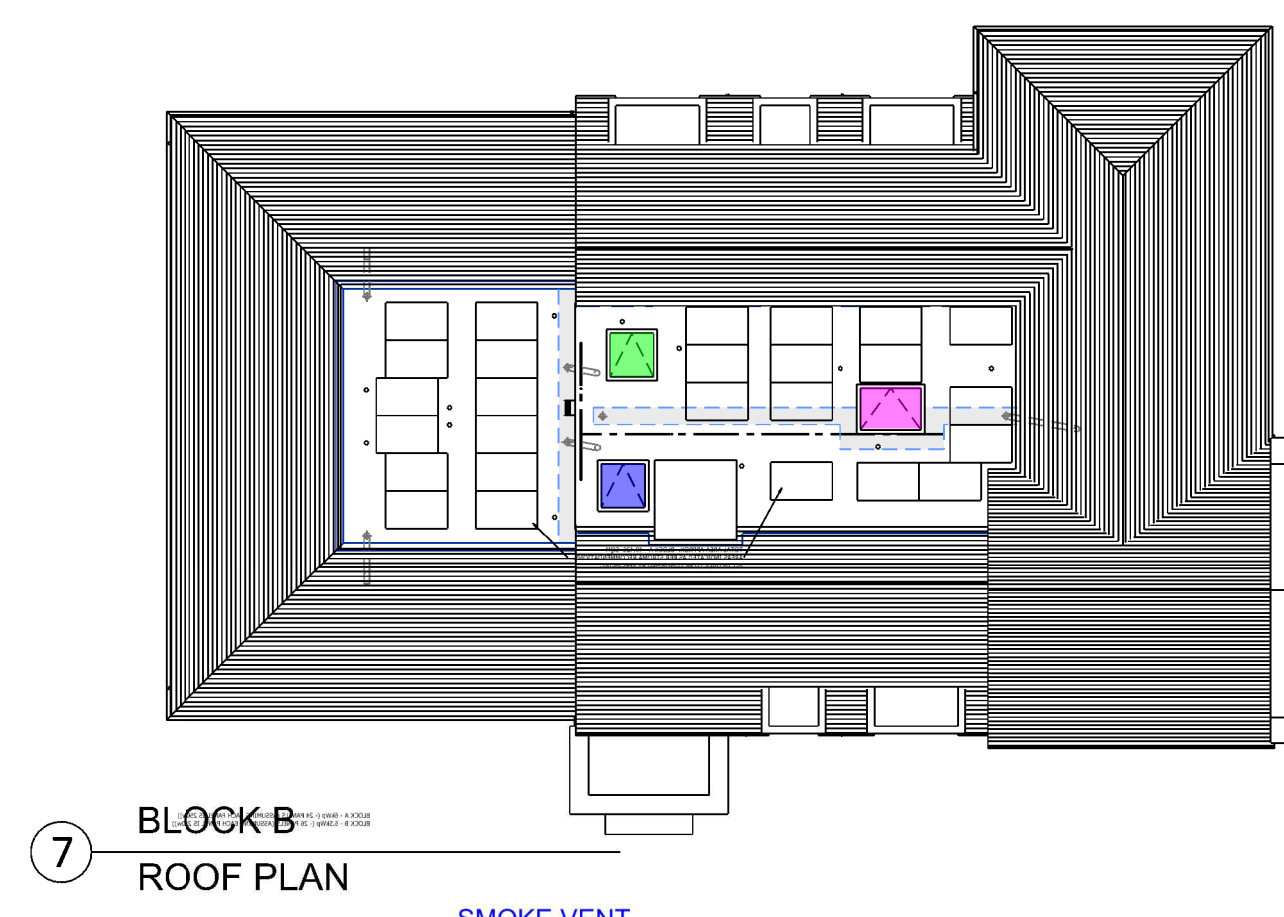
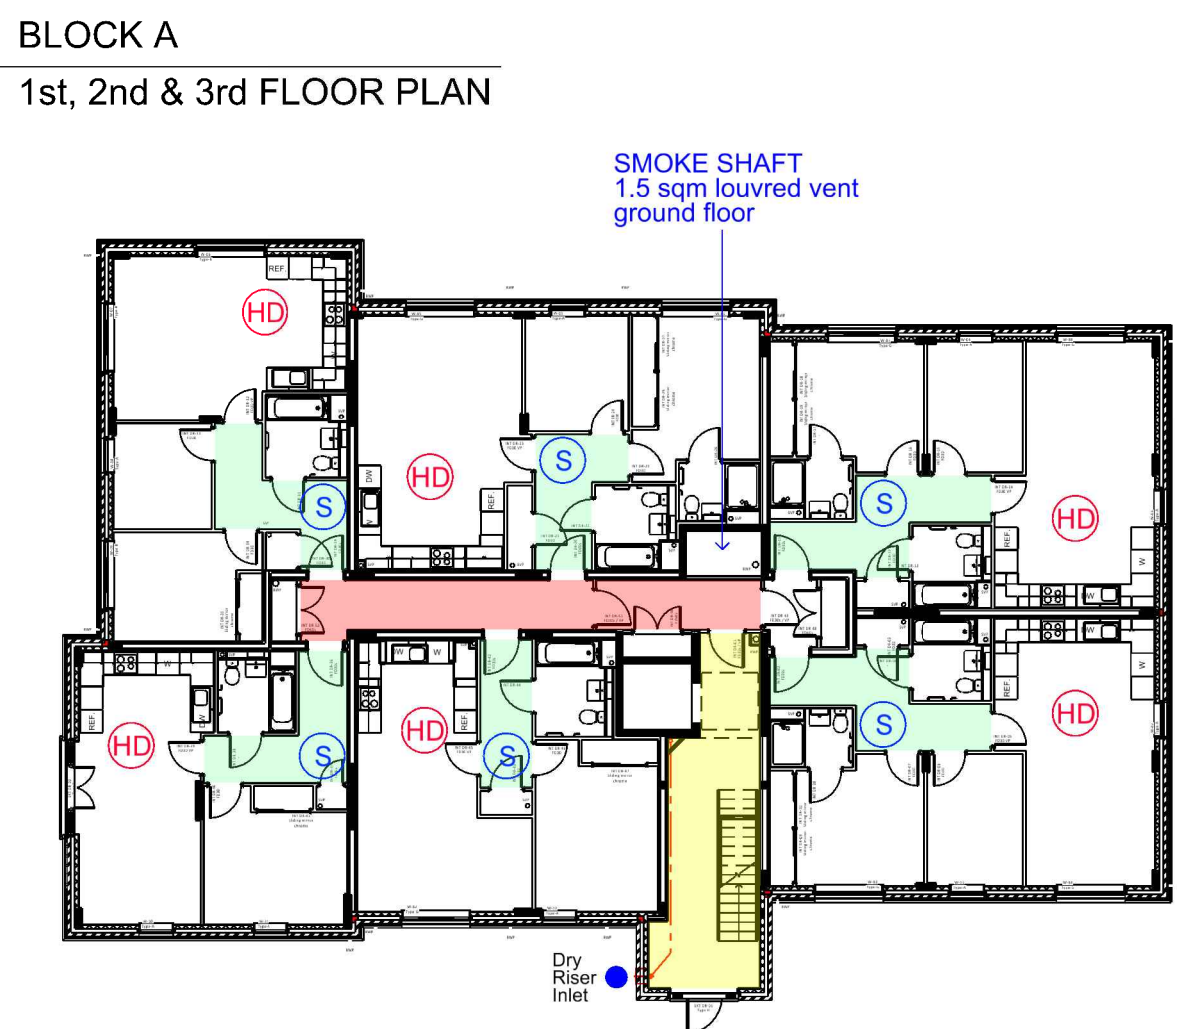
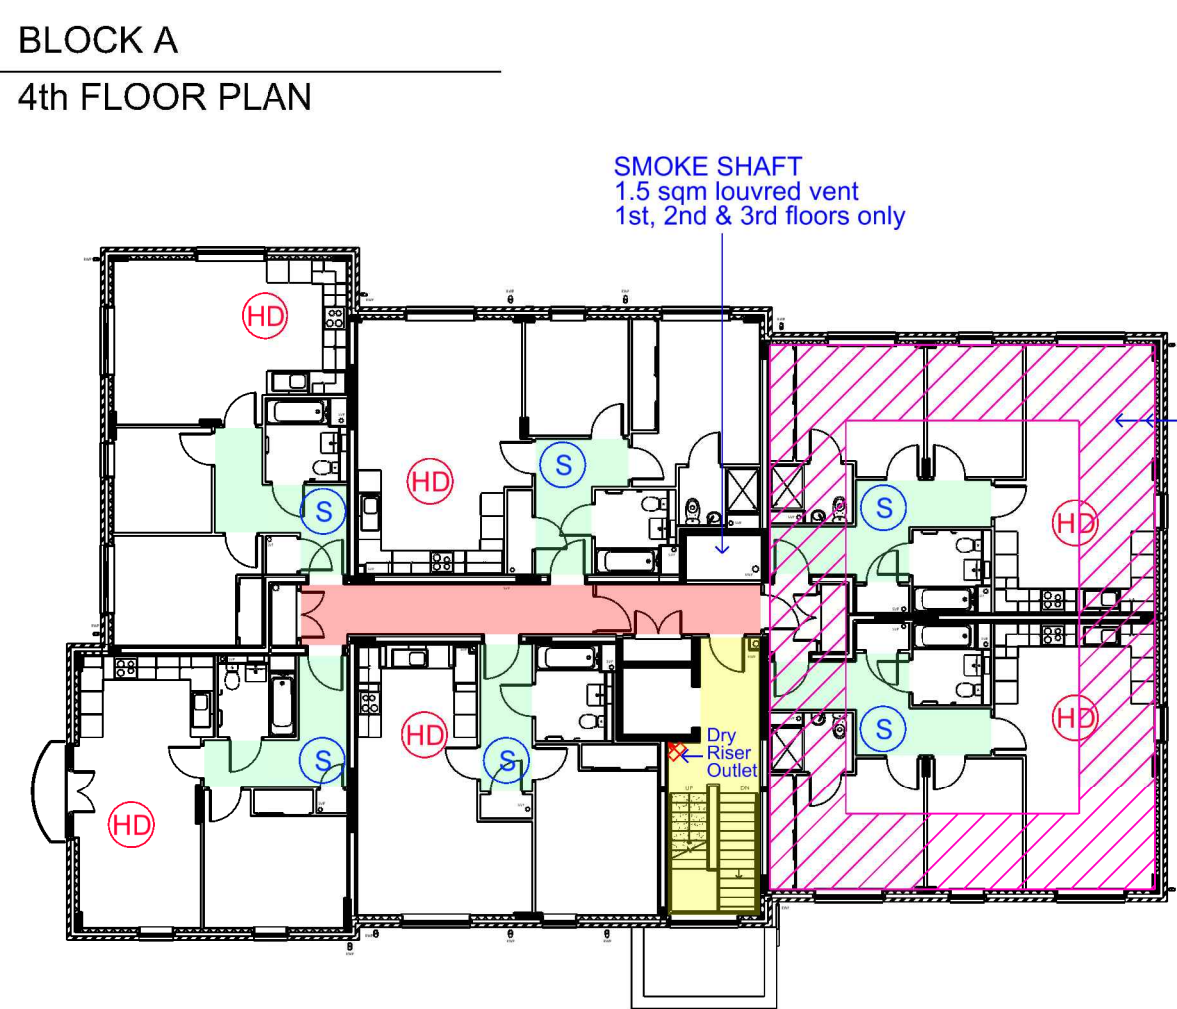
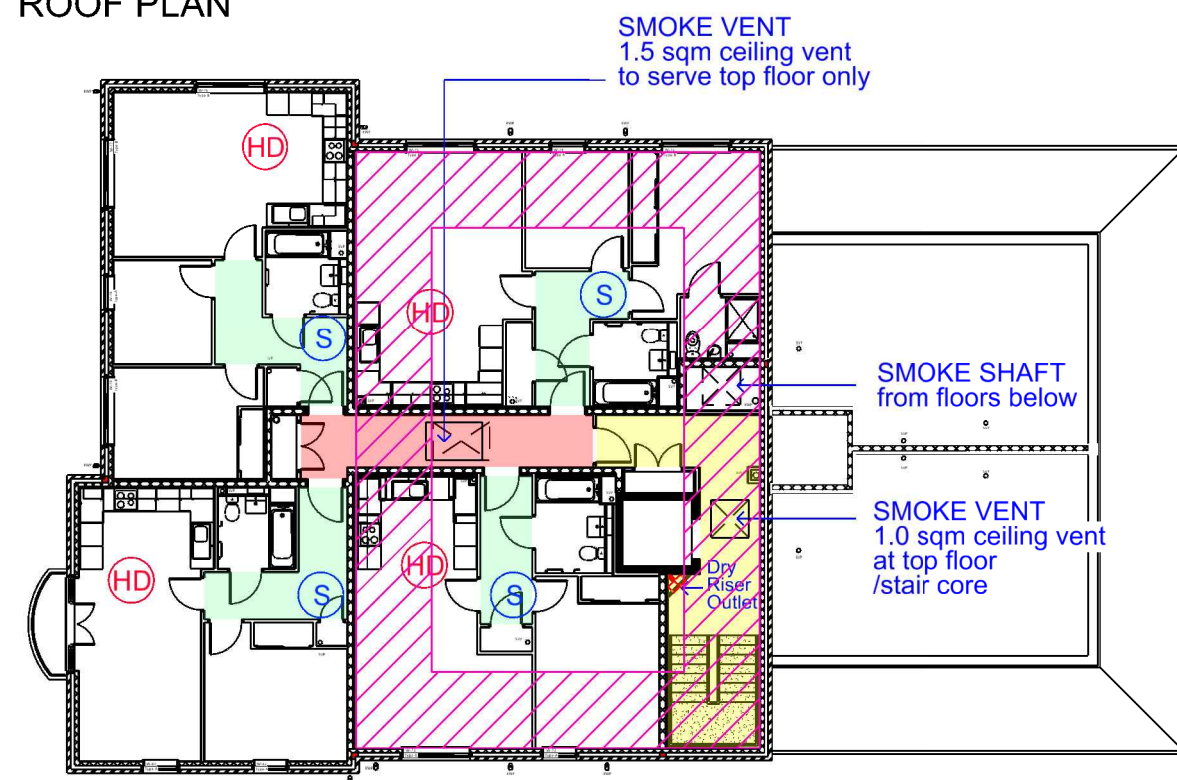
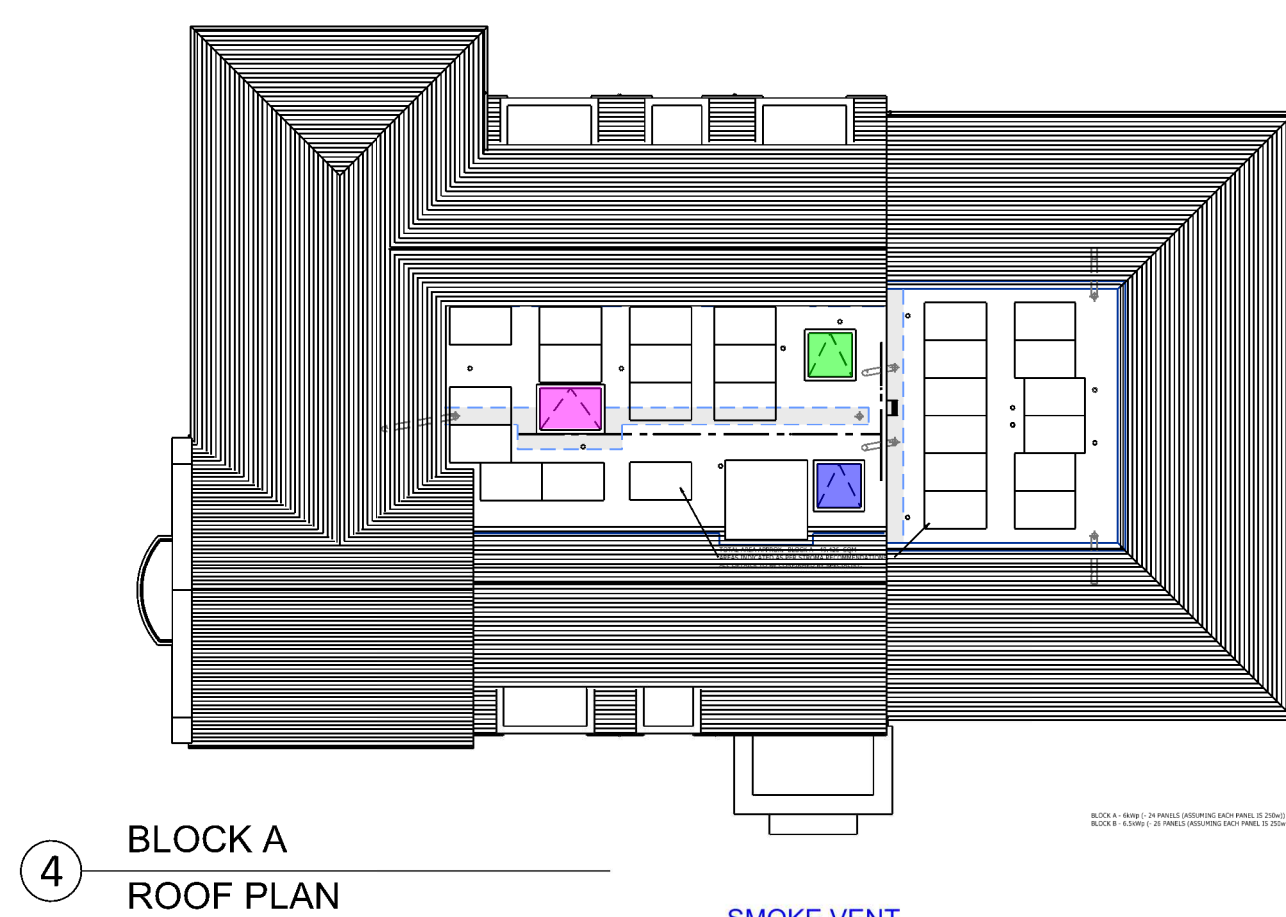
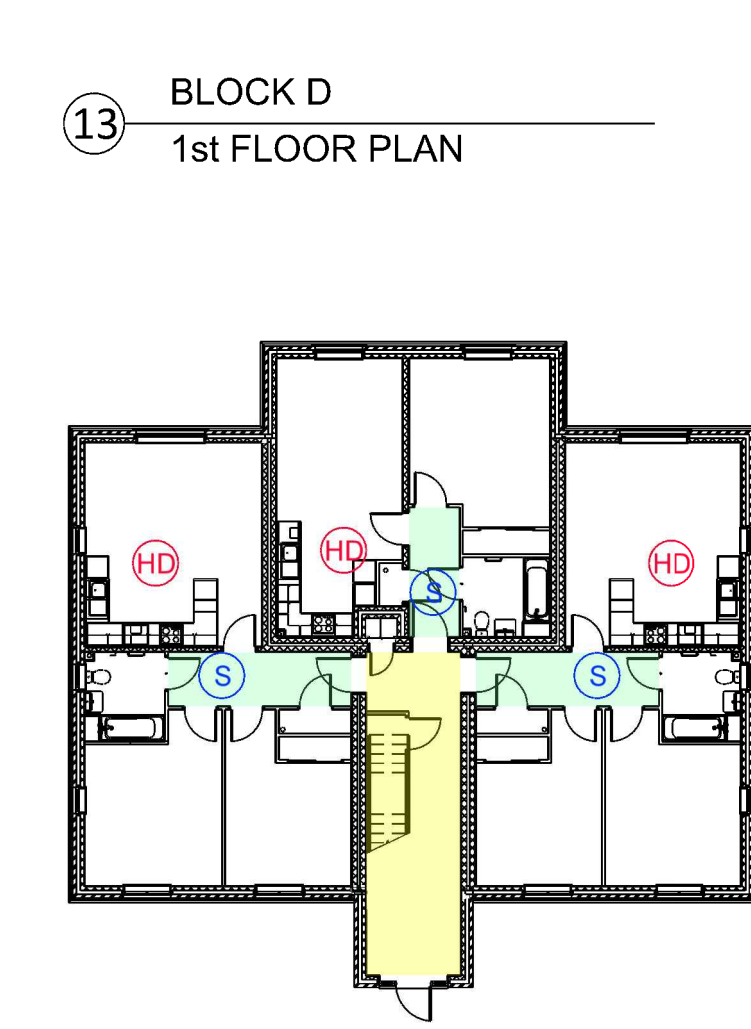
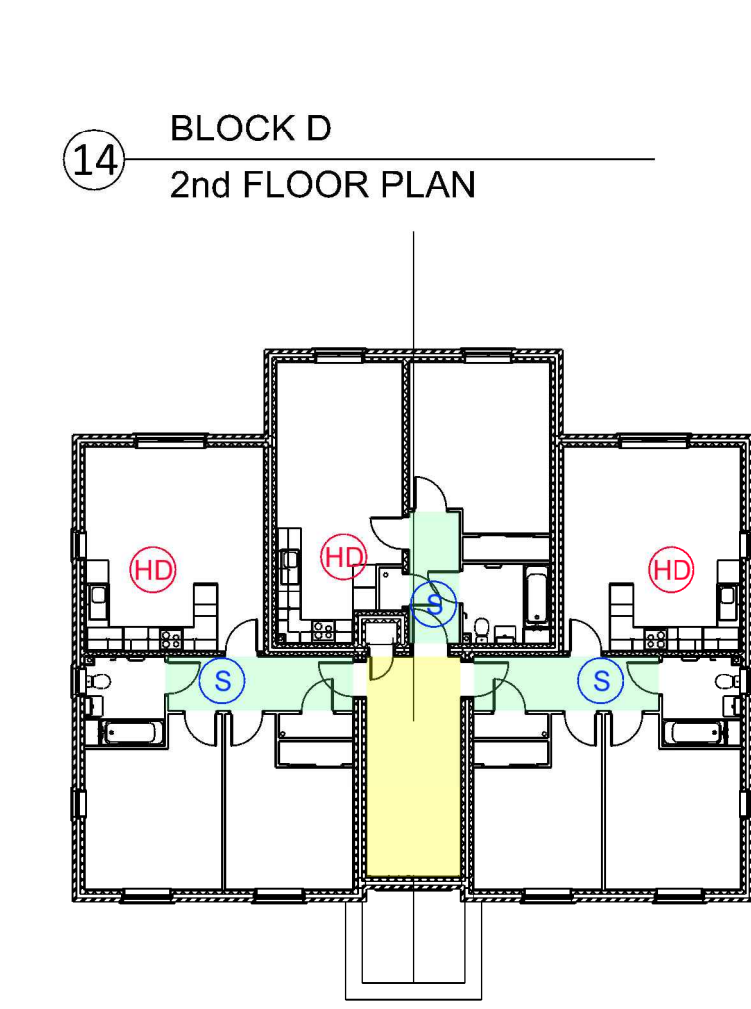


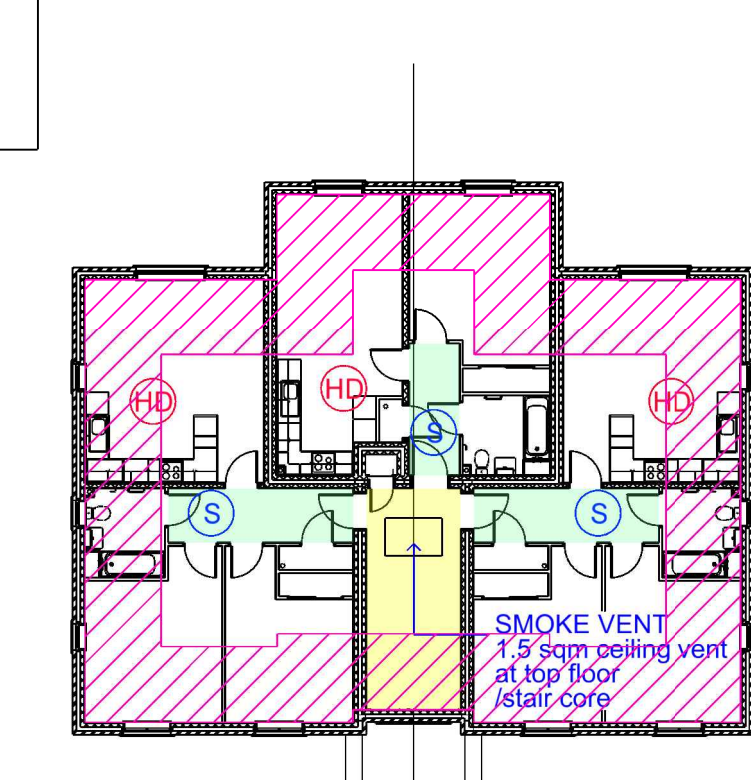

Legend


- Dry Riser
- Common Stair
60 minutes min fire resistance
FD30S Entrance Doors (self closing)
- Common Corridor
60 minutes min fire resistance
FD30S Entrance Doors (self closing)
- Multi Head - Heat & Smoke Detector
- Smoke Detector
- Protected Private Lobby
30 minutes min fire resistance
FD20 Doors
- AOV Smoke vent over shaft 1.0sqm
- AOV Smoke vent over upper floor lobby 1.5sqm
- Smoke vent over staircase 1.0sqm
(1.5sqm Block D)
activated by the fire service @
entry level
- *An automatic opening vent
with a geometric free area of at least 1.0m²
is required at the top of the stair, to be operated
on detection of smoke at any storey in the stair

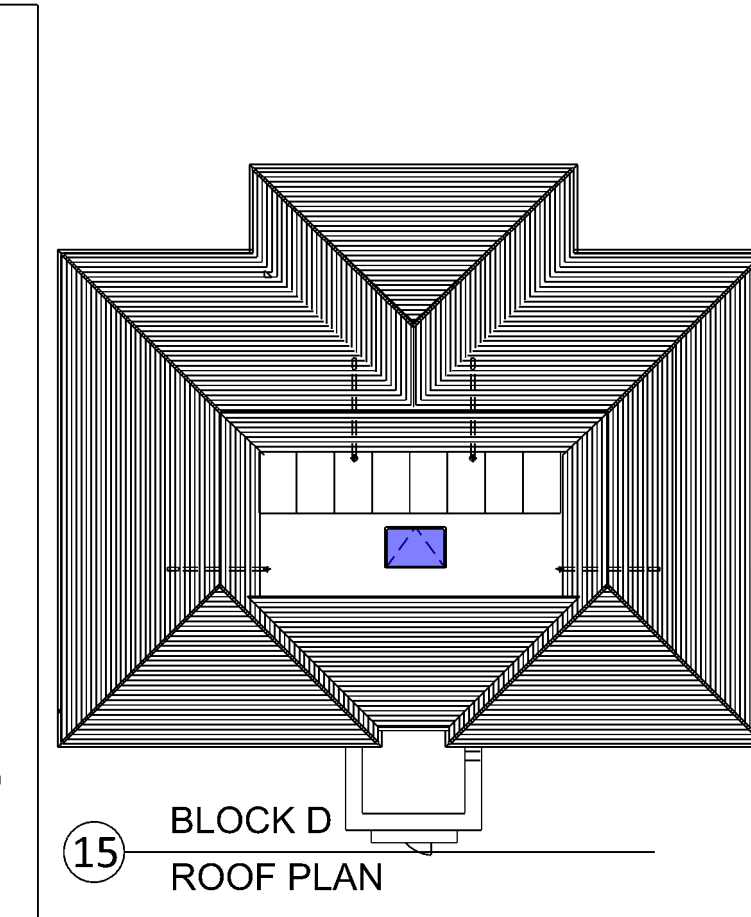


NOTES
Do not scale this drawing -
use figured dimensions only.
All dimensions are to be
checked before implementation.
Any discrepancies are to
be advised immediately.
All information is copyright of
DLA Architects Practice and
may not be used or reproduced
without prior permission.

REVISIONS
P1 09/11/2017 Fire plans updated and issued to Fire Consultant
P2 30/11/2017 Roof plans added with Smoke vents identified
P3 05/01/2018 Strategy adjusted to Fire Consultant comments
P4 15/05/2018 Ceiling protection added as agreed with BCO

PROTECTED ENTRANCE LOBBY
All apartments have travel distances to their entrance door greater than 9m,
therefore a protected hallway will be provided.

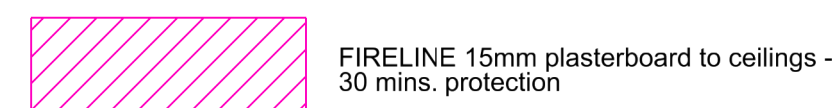

FIRE WARNING, Category LD2
A smoke alarm will be located within the entrance hallway and a multi sensor alarm in the
kitchen and principle habitable room (living room)

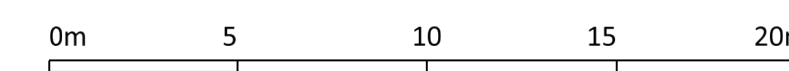

CAREYS
GUNHILL PRS, ALDERSHOT
FIRE STRATEGY PLANS
DATE: FEB 2017
DRAWING NUMBER: 1132-230

SCALE: 1:200@A1
REVISION: P4

STATUS
INFORMATION

DLA ARCHITECTS PRACTICE
INTEGRATED ARCHITECTURE
50 North Thirteenth Street
CENTRAL MILTON KEYNES, MK9 3BP
T: 01908 259719 F: 01908 605747
email: mail@dla-architects.com

© DLA ARCHITECTS PRACTICE LTD