



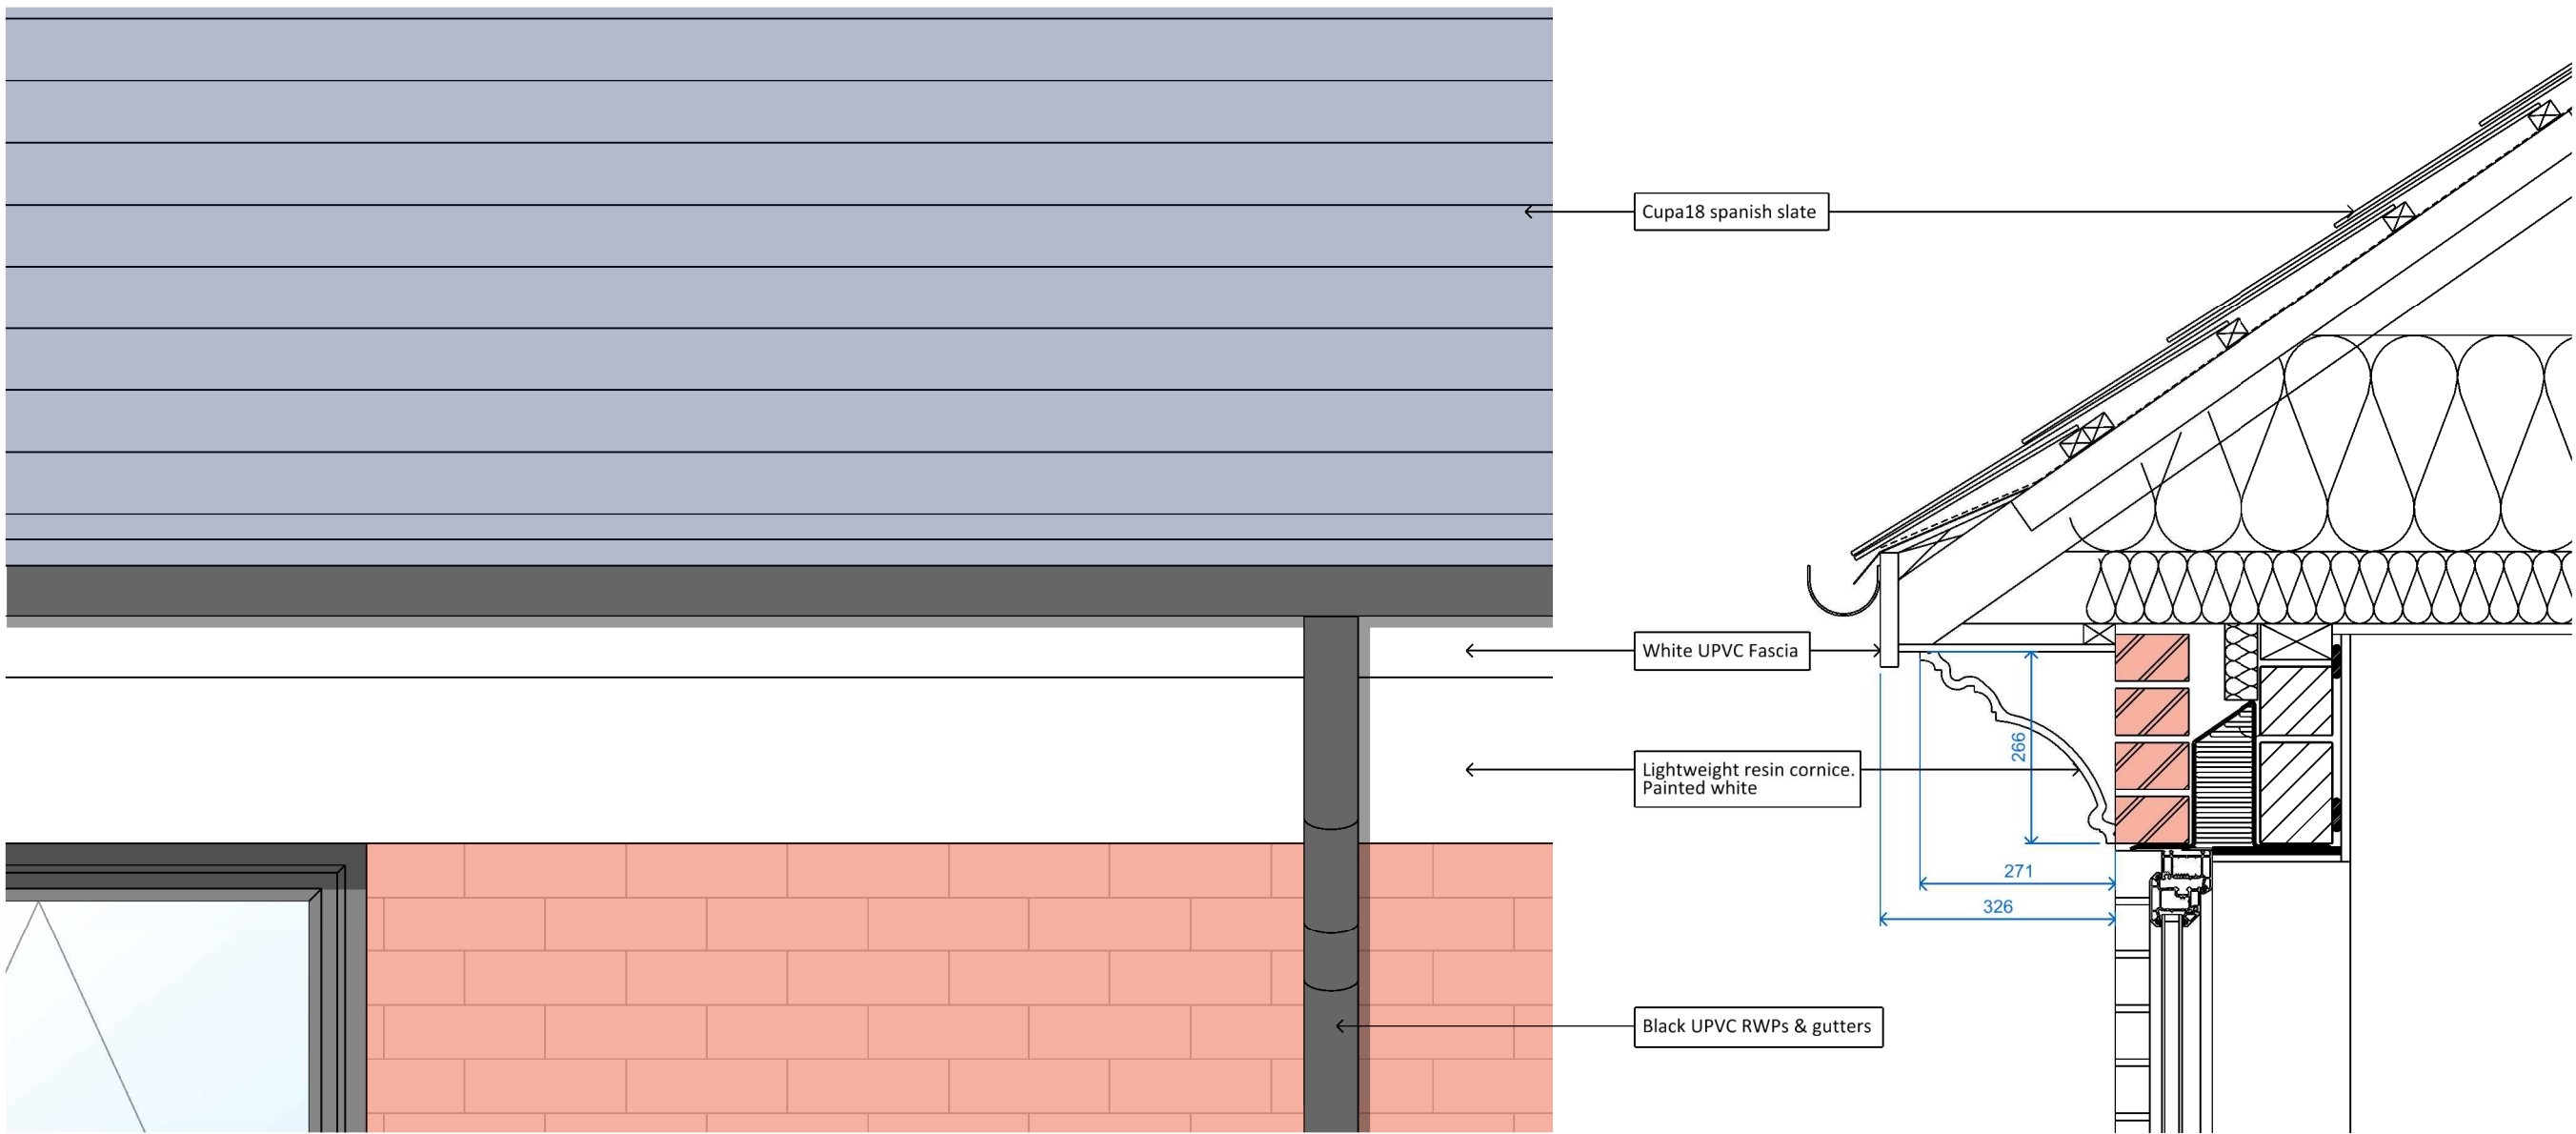


E07 Eaves, RWPs & Gutter Elevation
(Scale 1:10 @ A1)

W09 Eaves Section
(Scale 1:10 @ A1)

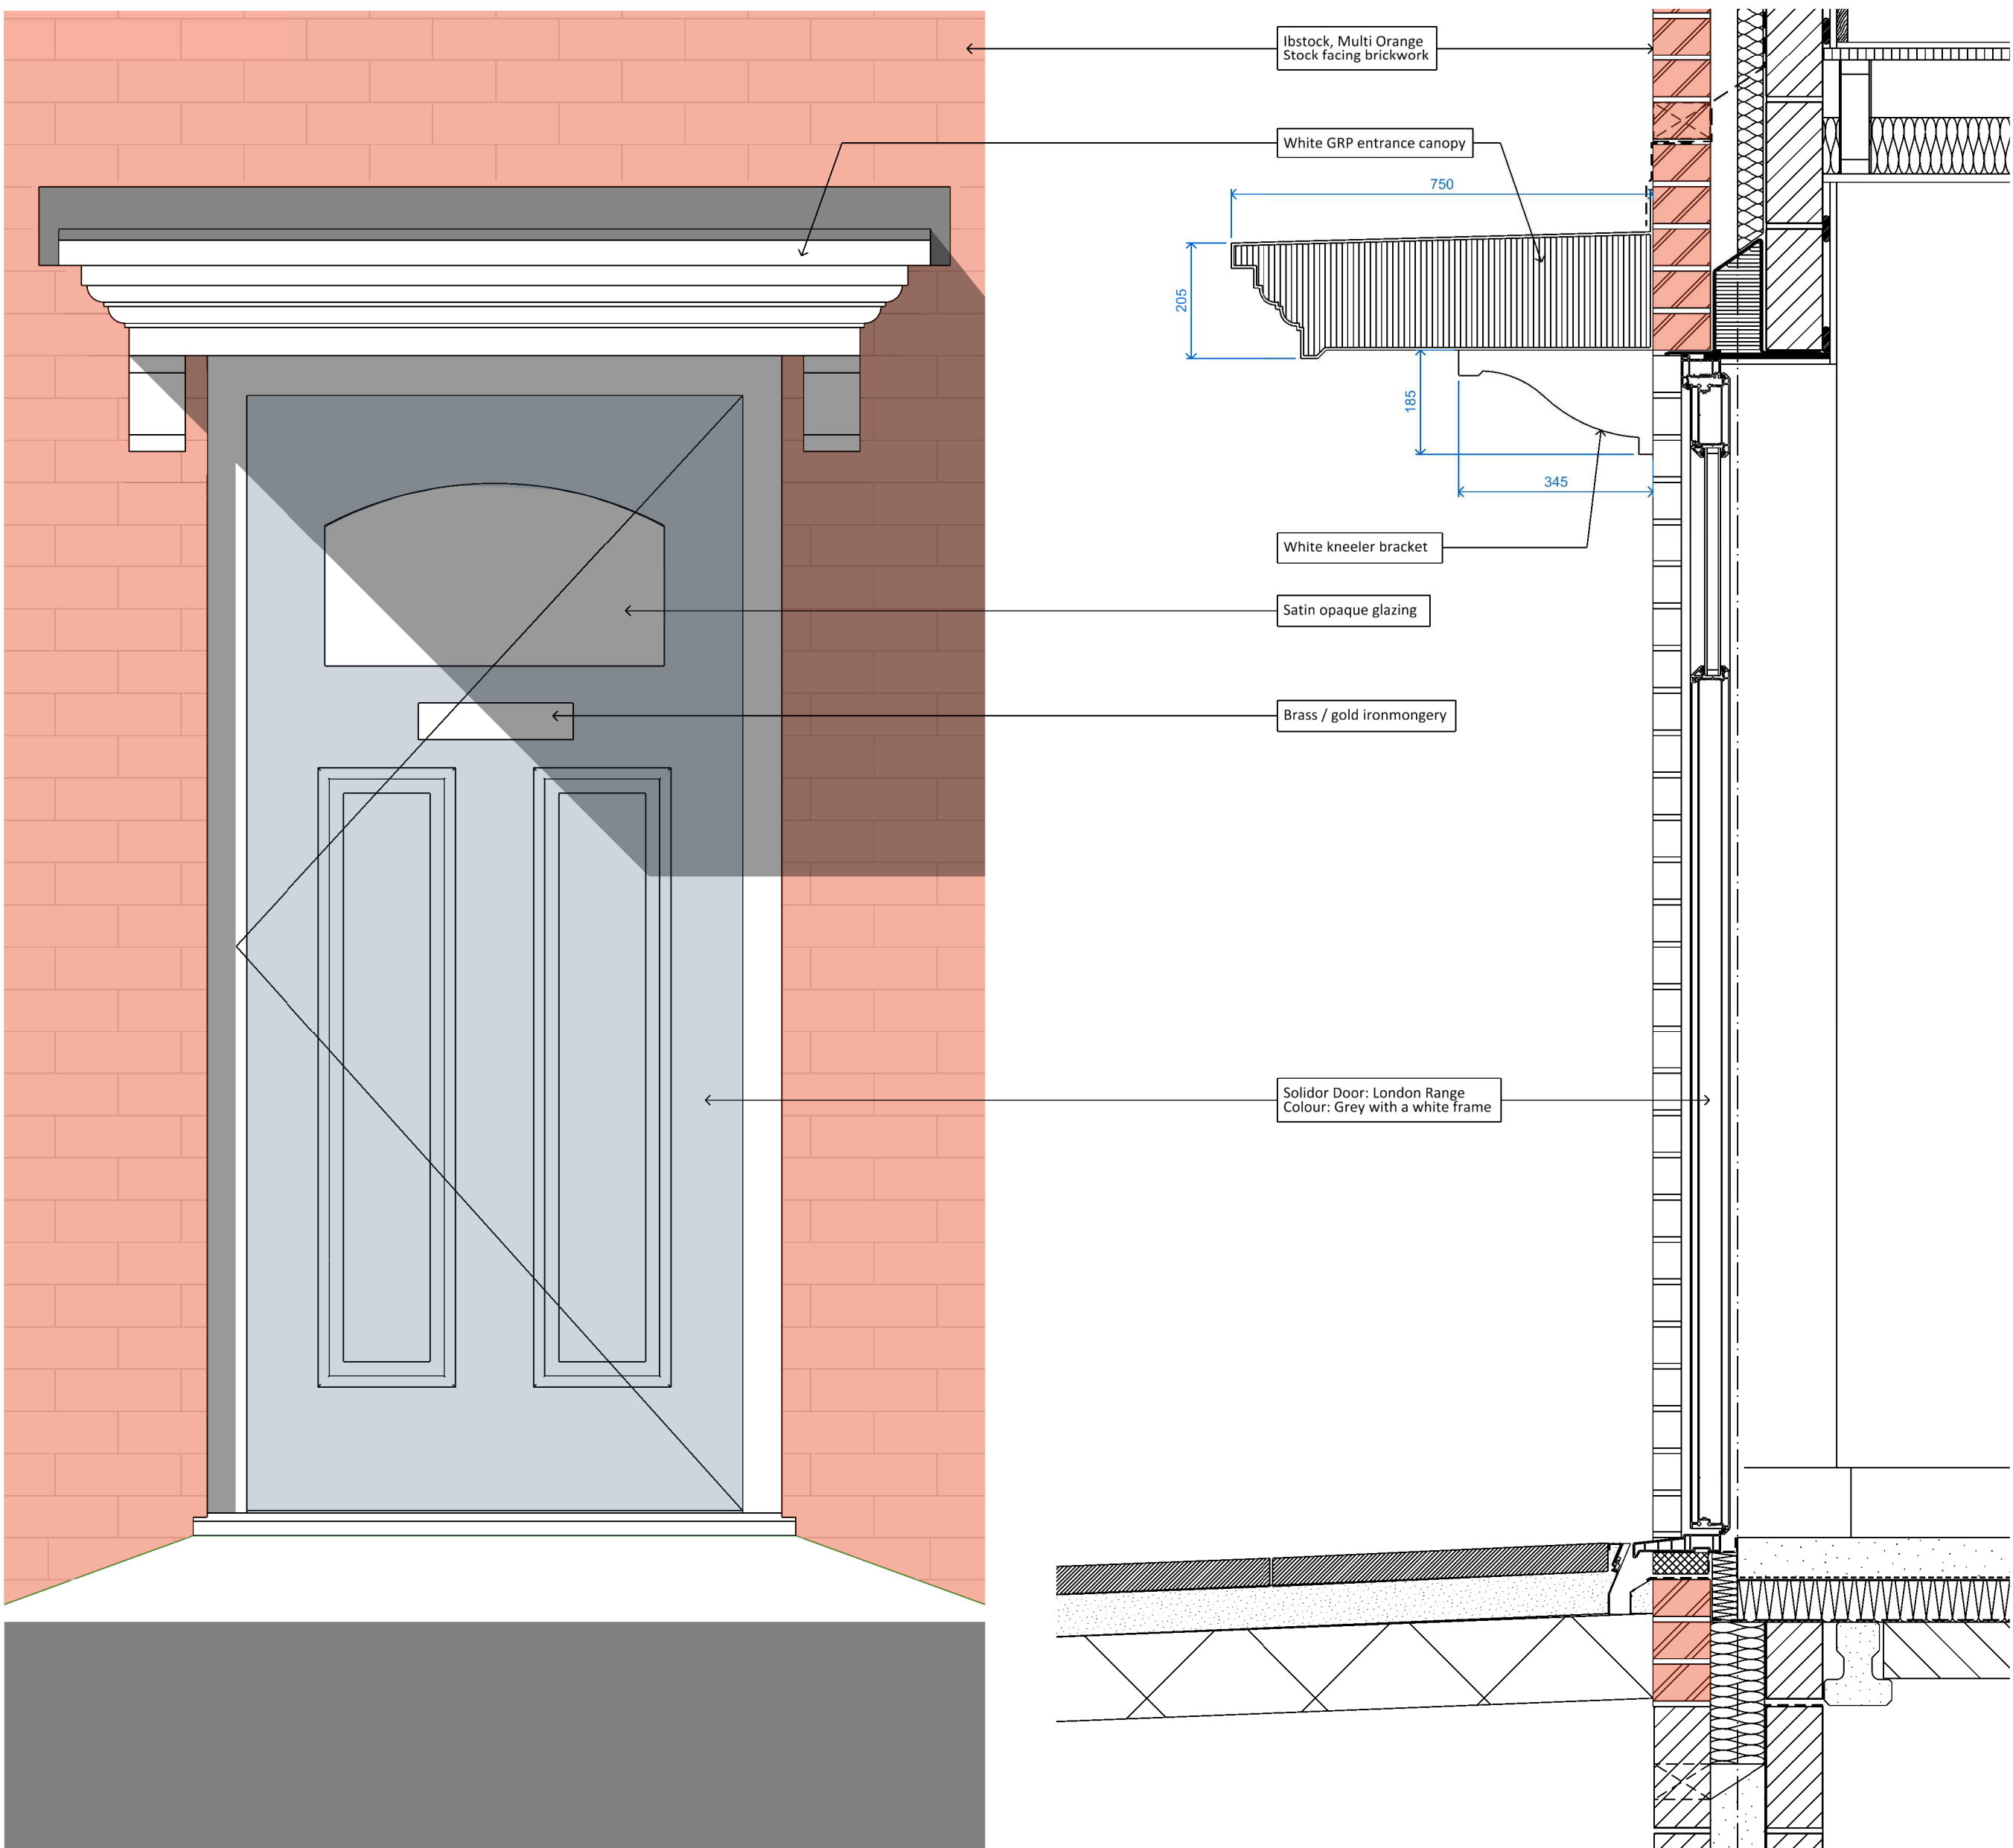

E06 Front Door & Canopy Elevation
(Scale 1:10 @ A1)

W08 Front Door & Canopy Section
(Scale 1:10 @ A1)

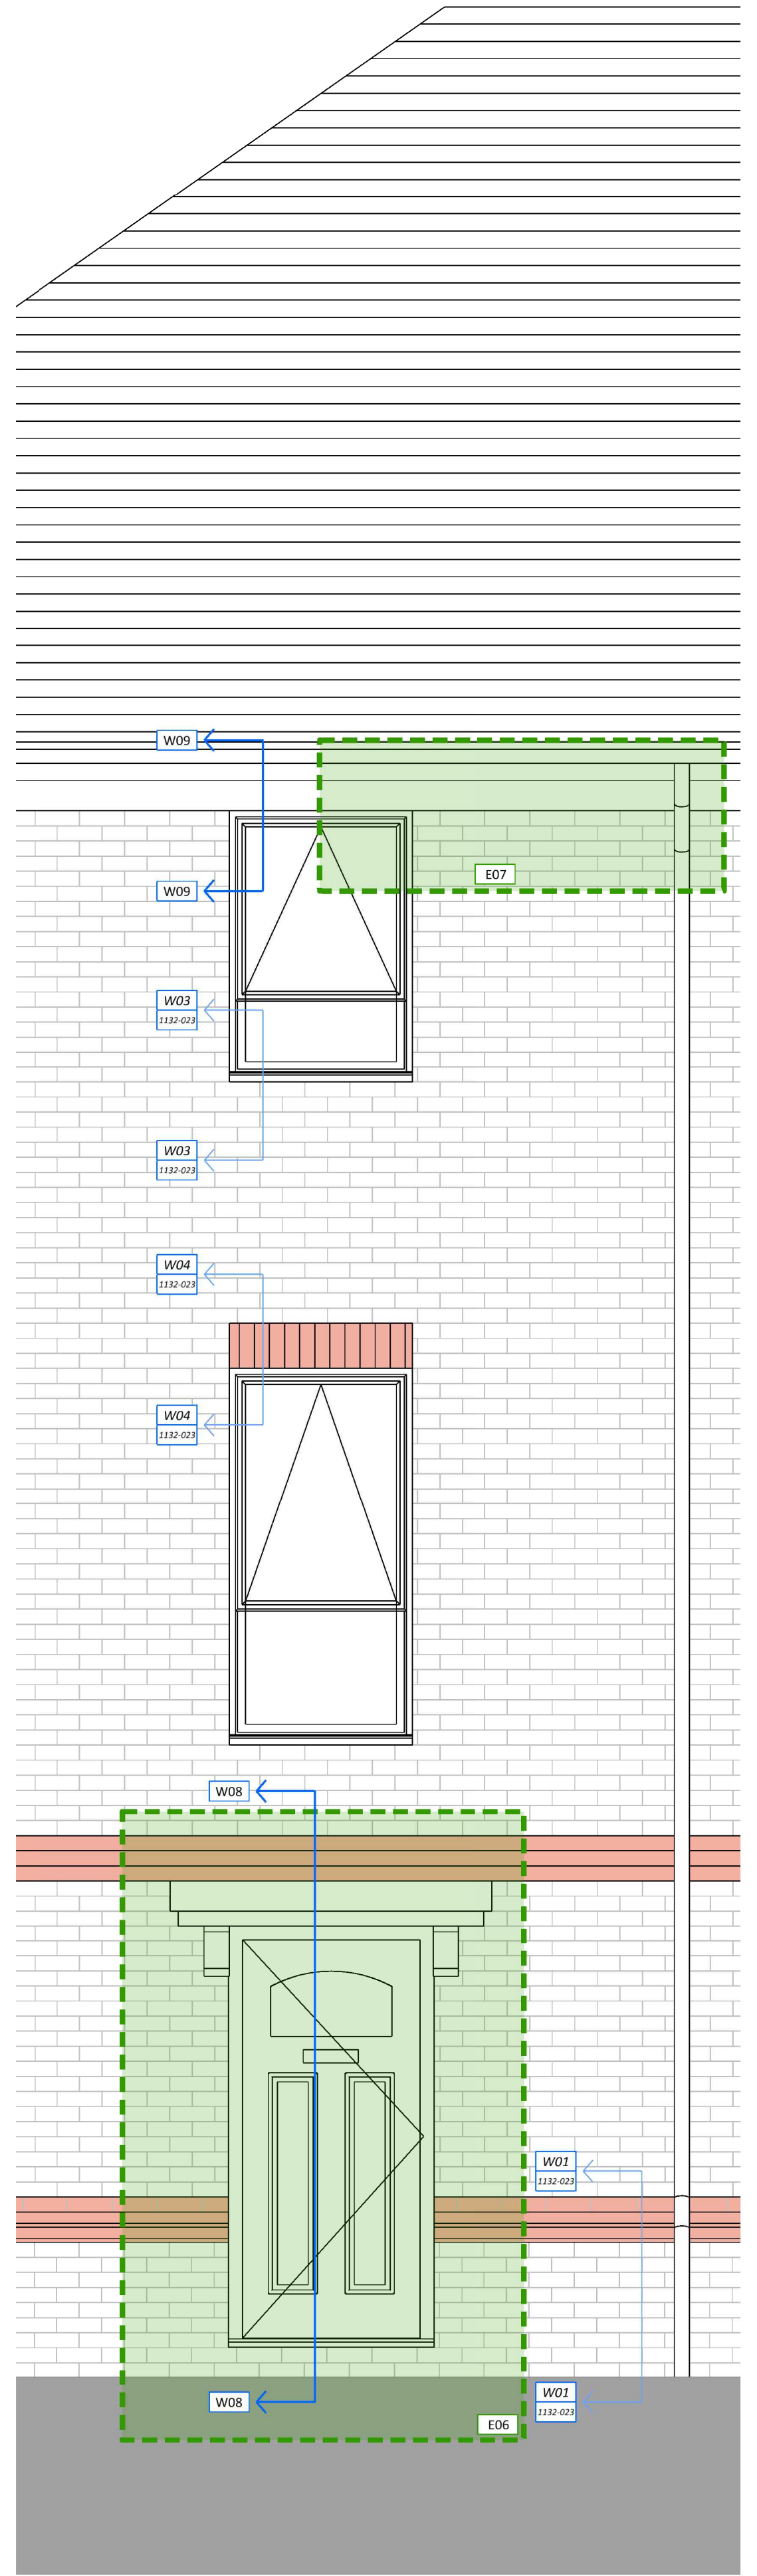

Front Elevation Part
(Scale 1:25 @ A1)

Front Elevation to House Plots:
81-82, 85-86 & 89-90
(Scale 1:100 @ A1)

NOTES
Do not scale this drawing - use figured dimensions only. All dimensions are to be checked before implementation. Any discrepancies are to be advised immediately. All information is copyright of DLA Architects Practice and may not be used or reproduced without prior permission.

REVISIONS
P1 15/11/2017 Issued for approval.
P2 19/12/2017 Slate adjusted

Key:
All brickwork:
Ibstock, Multi Orange Stock 0772

Note:
Drawing to be read in conjunction with Materials Summary (1132-MAT-SUM) & Material Treatment Drawings (1132-20 - 1132-22)

CAREYS
GUN HILL, PRS, ALDERSHOT
MATERIAL DETAILS: SEMI HOUSES - SHEET 2
DATE NOV 2017
DRAWING NUMBER 1132-24
SCALE 1:10 & 1:25 @ A1
REVISION P2
STATUS PLANNING

DLA ARCHITECTS PRACTICE
INTEGRATED ARCHITECTURE
50 North Thirteenth Street
CENTRAL MILTON KEYNES, MK9 3BP
T: 01908 259719 F: 01908 605747
email: mail@dla-architects.com
© DLA ARCHITECTS PRACTICE LTD