


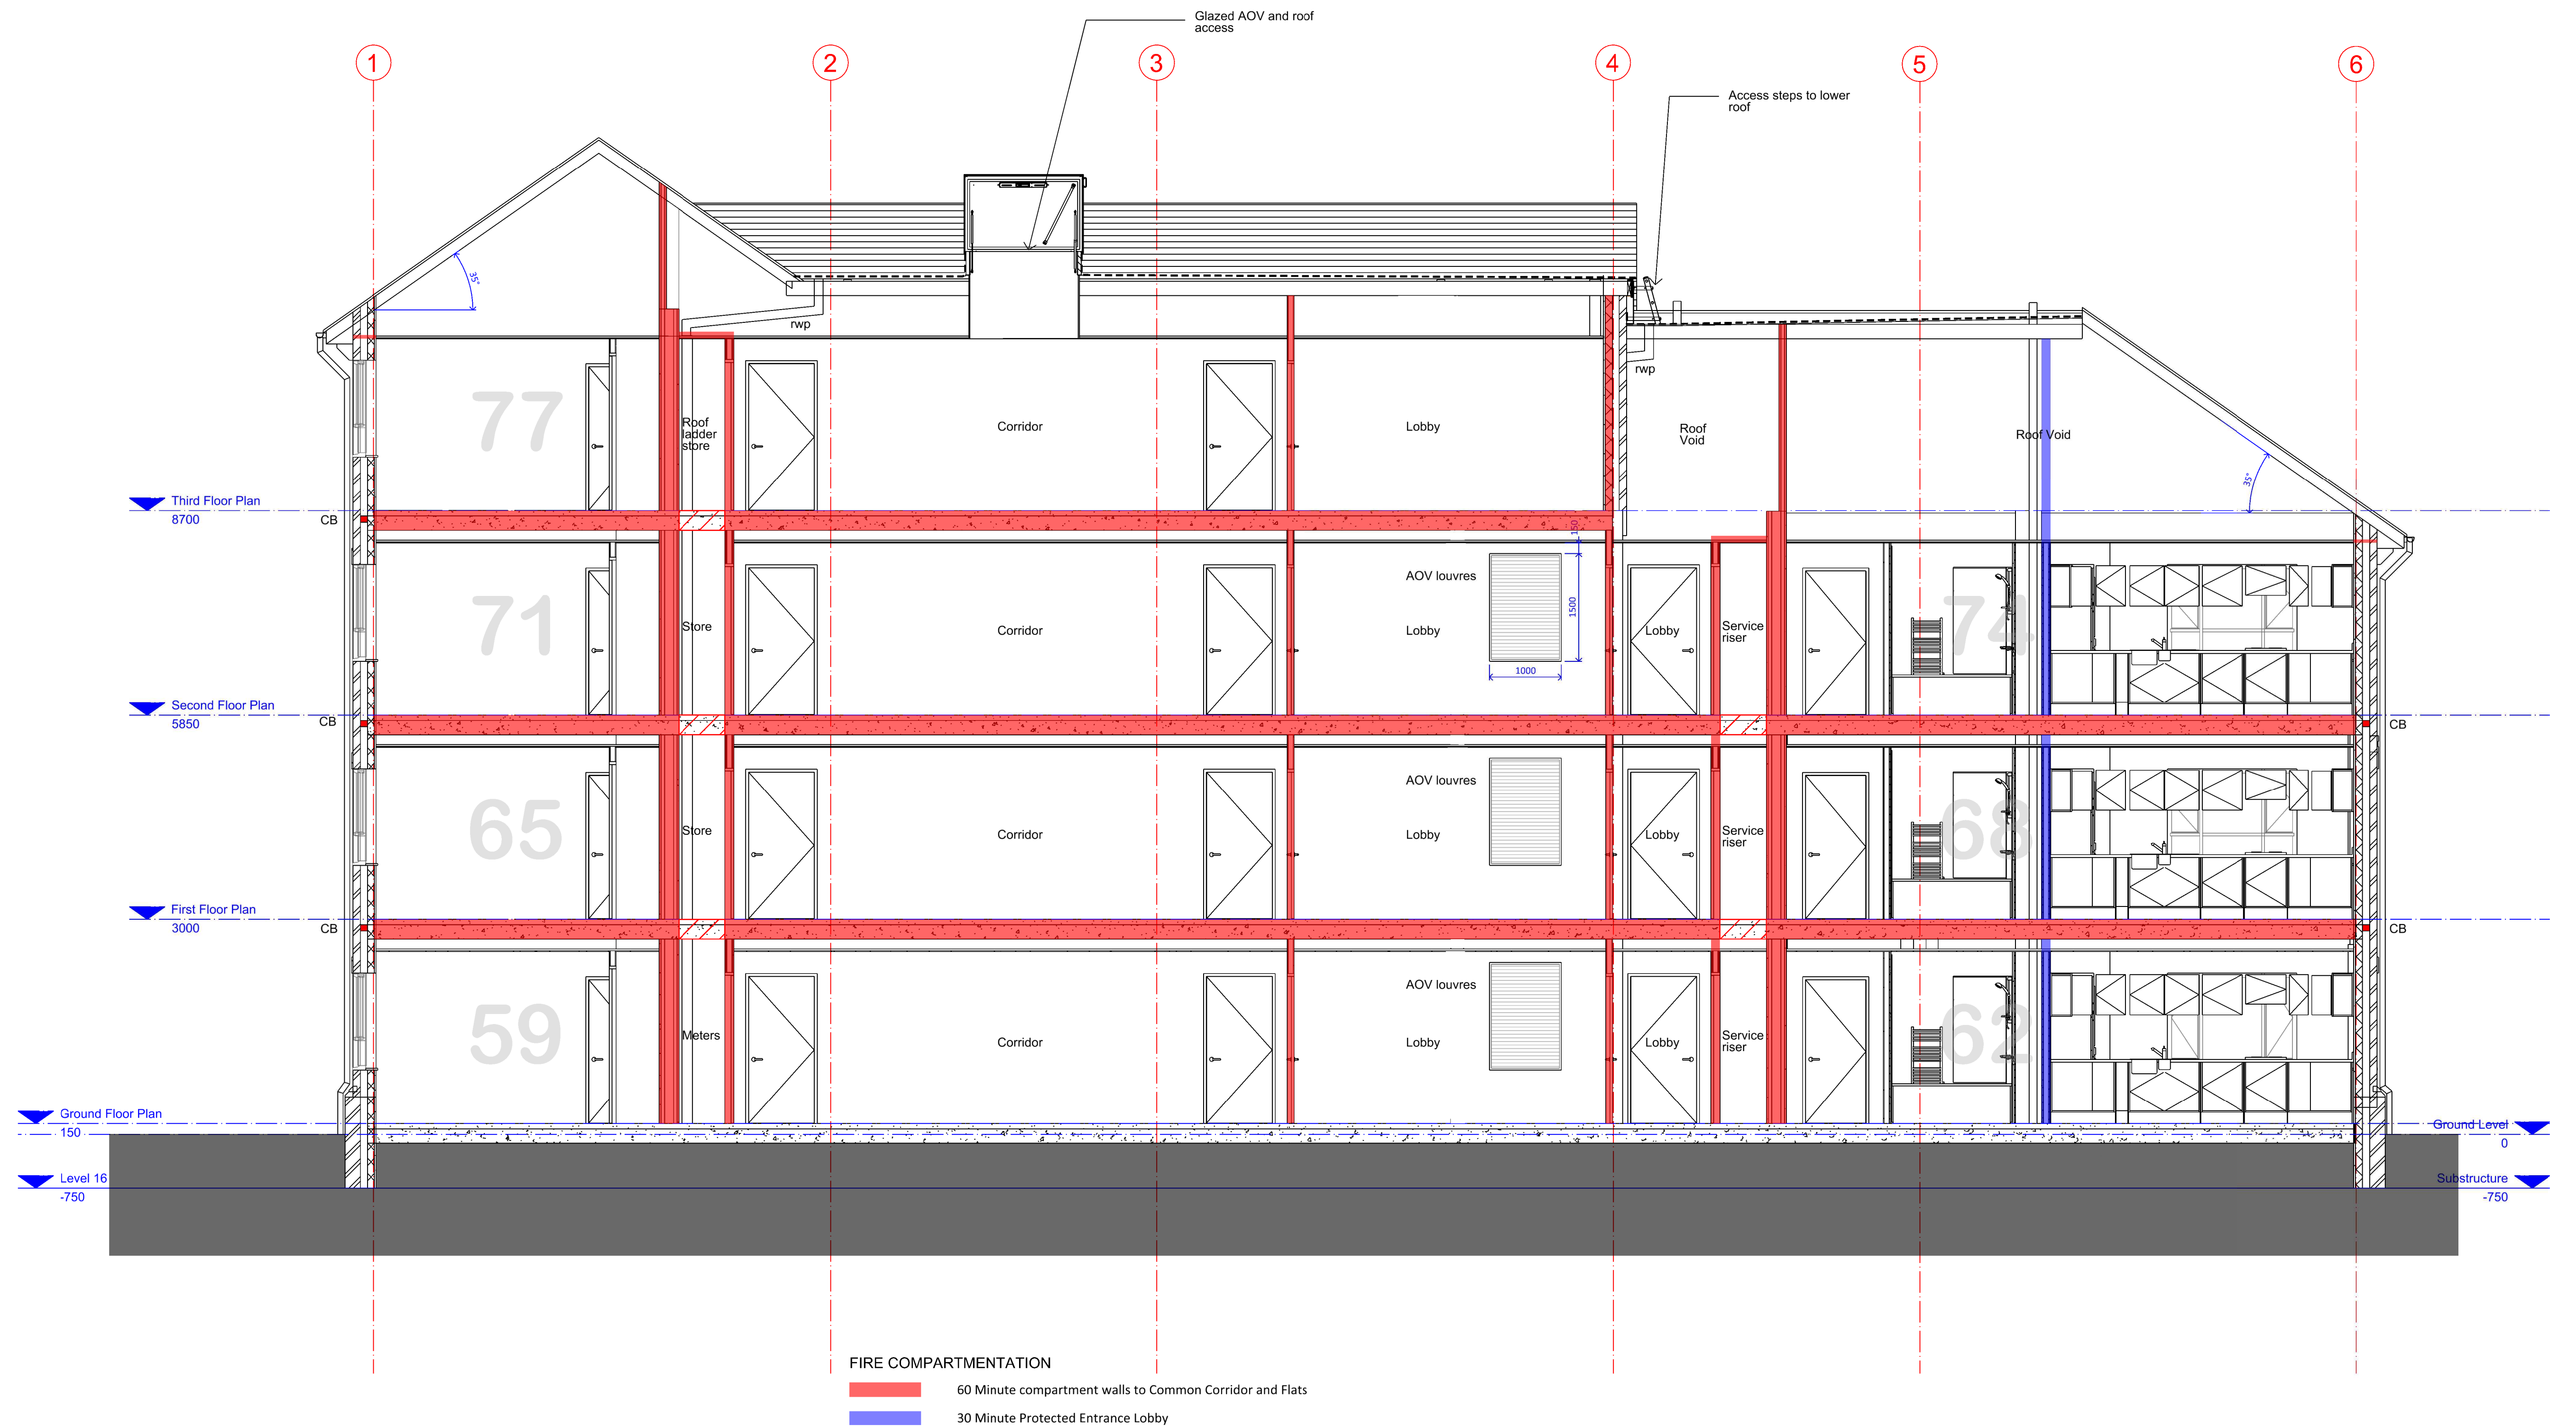

NOTES
Do not scale this drawing - use figured dimensions only. All dimensions are to be checked before implementation. Any discrepancies are to be advised immediately. All information is copyright of DLA Architects Practice and may not be used or reproduced without prior permission.

REVISIONS

PHASES OF WORK

1. Cavity Barriers / Fire Stopping installation
2. Compartment floor / walls
3. Service penetration - All penetrations to be confirmed once services & utilities contractor information is available

NOTES

- Cavity barriers (30 minute) in external wall - Vertical @ every party wall, Horizontal @ every party floor to be installed in accordance with ABD Section 9
 - Services SVP/RWP's to be fire sealed with collars in accordance with ADB Section 10 Table 14
 - ☒ Service Risers @ floor slab are not required to be fire stopped on the basis that the partition and doors installed are FD60S rated unless advised otherwise by Building Control
- Allow for fire stopping all services penetration through party walls and floors

CAREYS
GUN HILL, PRS, ALDERSHOT
BLOCK C - FIRE STOPPING+CAVITY BARRIER SECTION BB
DATE FEB 2018
DRAWING NUMBER 1132-245
SCALE 1:50 @ A1
REVISION P1
STATUS INFORMATION

DLA ARCHITECTS PRACTICE
INTEGRATED ARCHITECTURE
50 North Thirteenth Street
CENTRAL MILTON KEYNES, MK9 3BP
T: 01908 259719 F: 01908 605747
email: mail@dl-a-architects.com
© DLA ARCHITECTS PRACTICE LTD