

construct new rear dormer and side
cheek in 100x50 C16 timber studs
@ 400 cns with 100mm Celotex
between, provide 50mm Celotex
to inner face of studs and p/board
finish, externally provide vapour
membrane, 18mm WBP ply fixed @
400 cns with tile and batten finish

No beams are supported on Chimney breast brickwork.

CU	electrical consumer unit, to be positioned as shown, provide a minimum of 4 double power outputs per room and an additional 4 double outputs for each kitchen, provide all required spurs for appliances, allow for LED downlighters to habitable rooms, hallways and kitchens, allow for 2 wall lights to Lounge, provide TV, telephone points and internet connections to all rooms
----	---


D

new
syp

C

build up section of
party wall in reclaimed stock
brickwork and insulate as detail

MARCH 2019

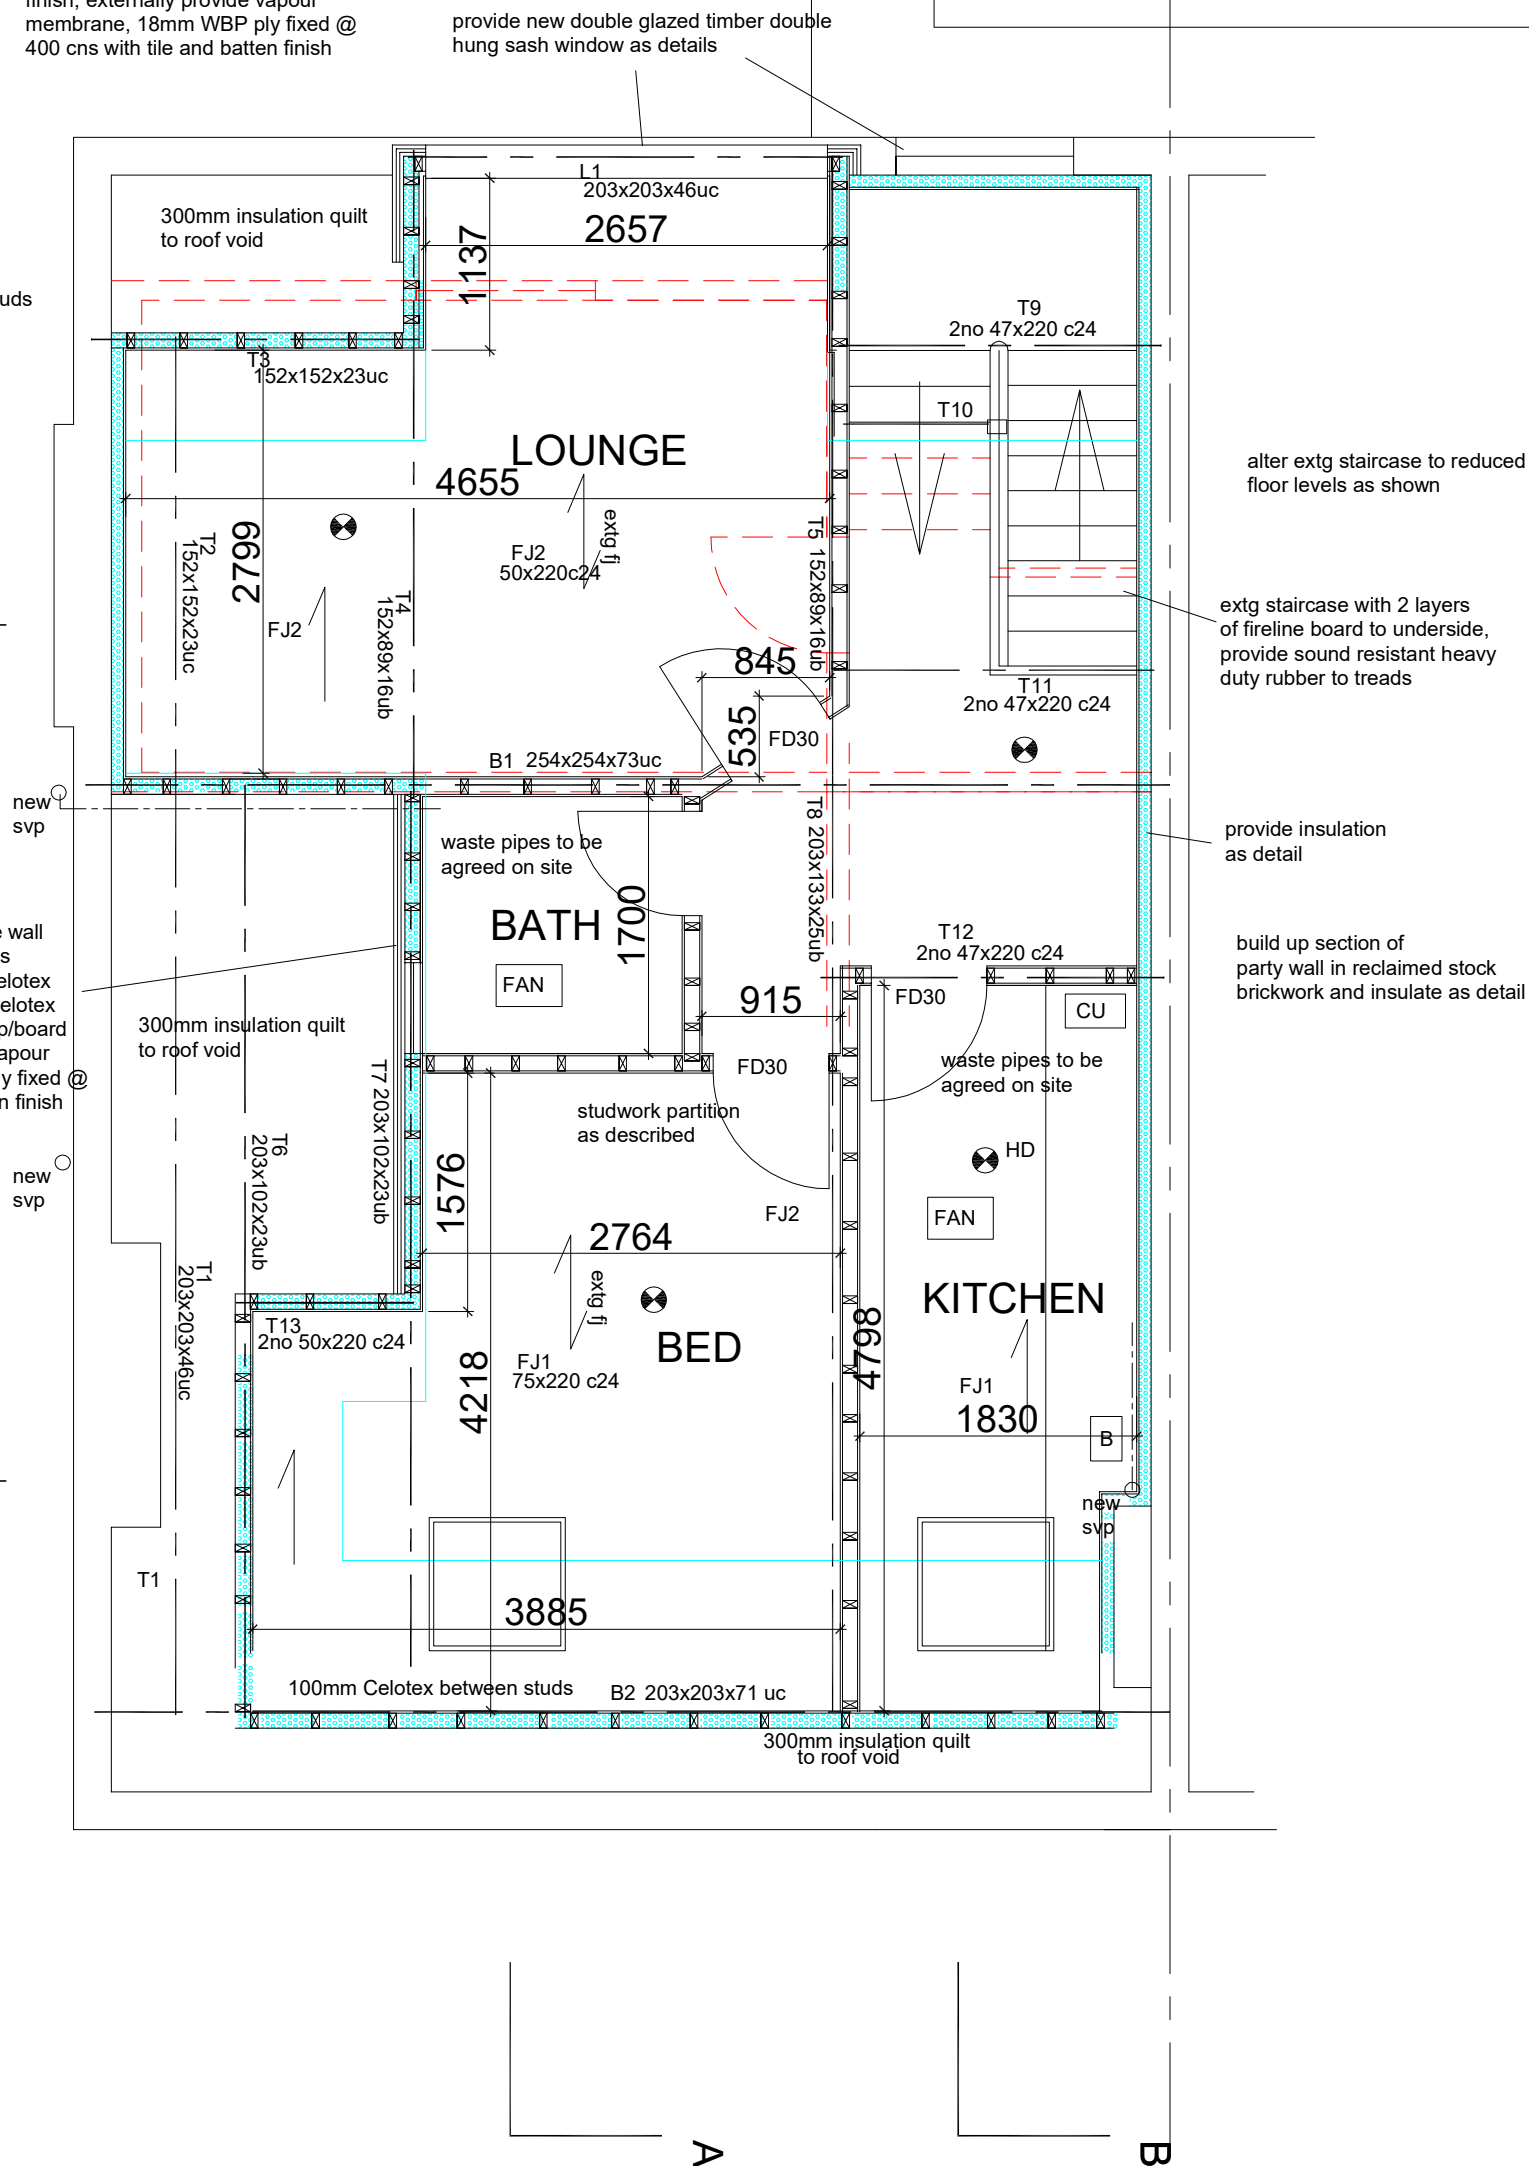

SECOND FLOOR PLAN