


DETAIL A

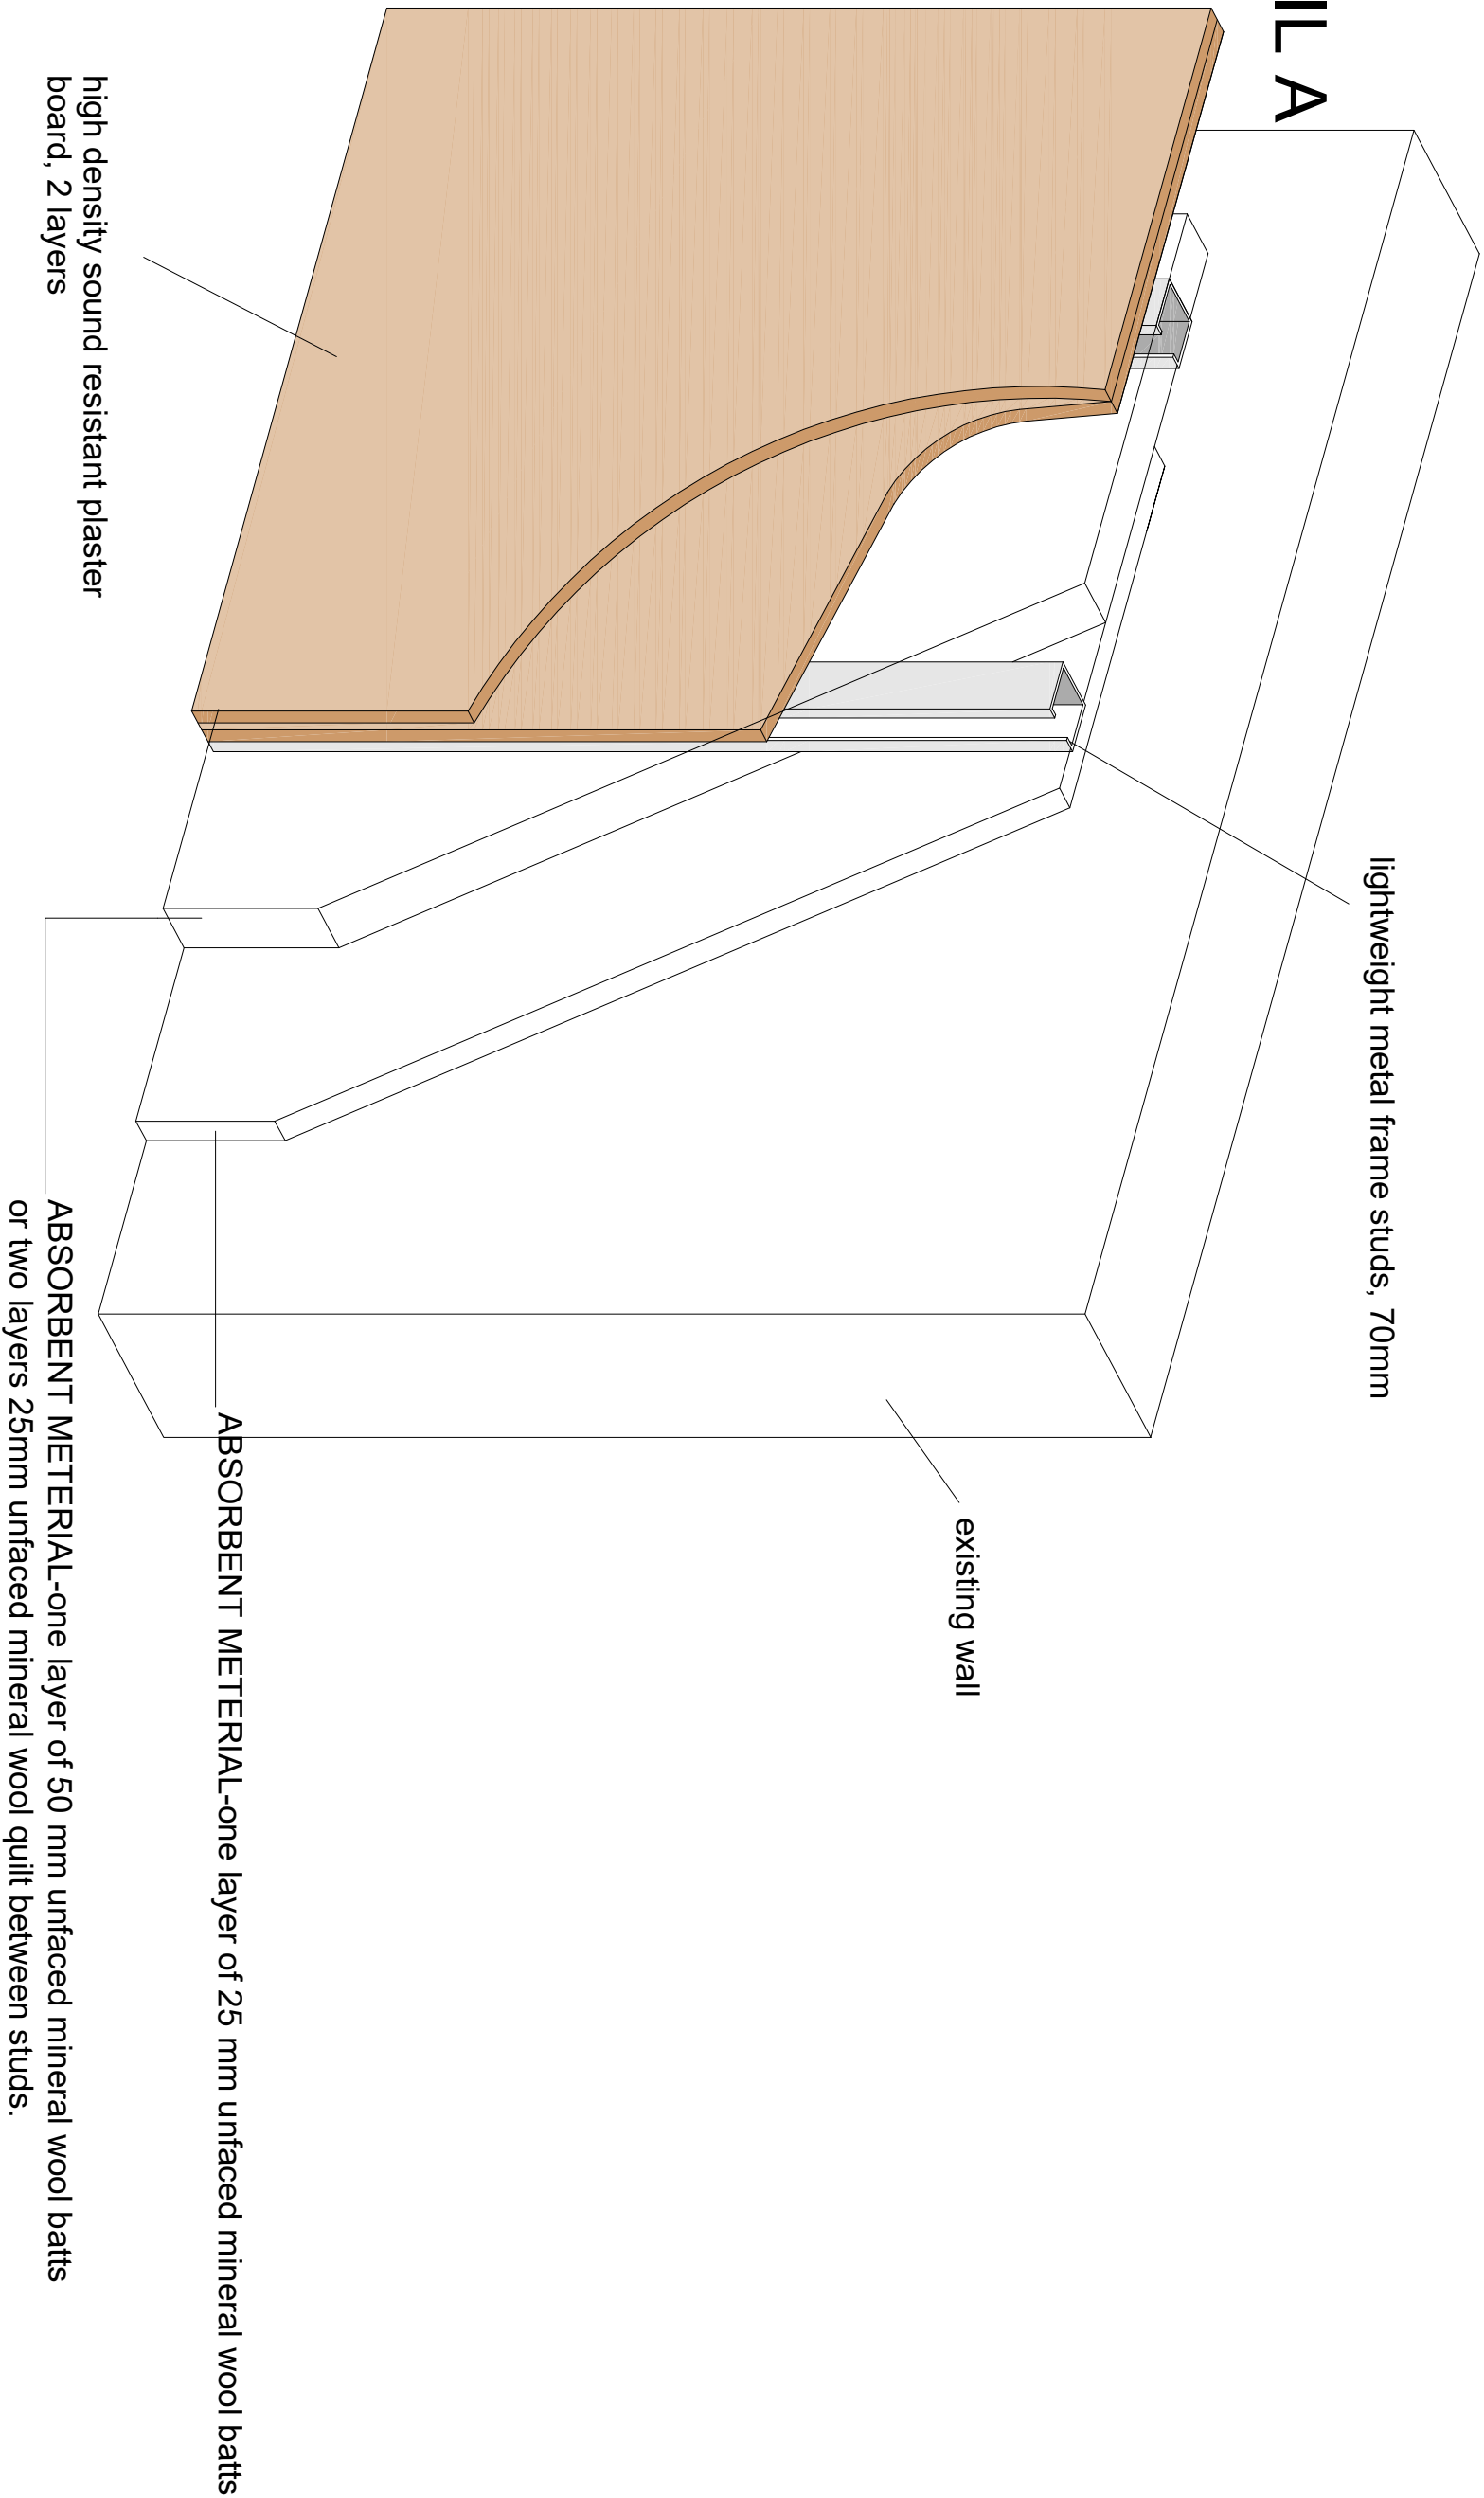

high density sound resistant plaster board, 2 layers

lightweight metal frame studs, 70mm

existing wall

ABSORBENT METERIAL-one layer of 25 mm unfaced mineral wool batts

ABSORBENT METERIAL-one layer of 50 mm unfaced mineral wool batts or two layers 25mm unfaced mineral wool quilt between studs.



URBAN REGEN LONDON Ltd.

TITLE		ADDRESS	
PROPOSED DRAWINGS		95 MALVERN ROAD LONDON. NW6	
CLIENT		SCALE	DATE
Mr. C. NORMAN		1:50 @ A3	MARCH 2019
DRAWING NO.		REV.	
190328/21			

Tel: 07970 647 449 Fax: 020 8963 9991 Email: urfordon@aol.com