



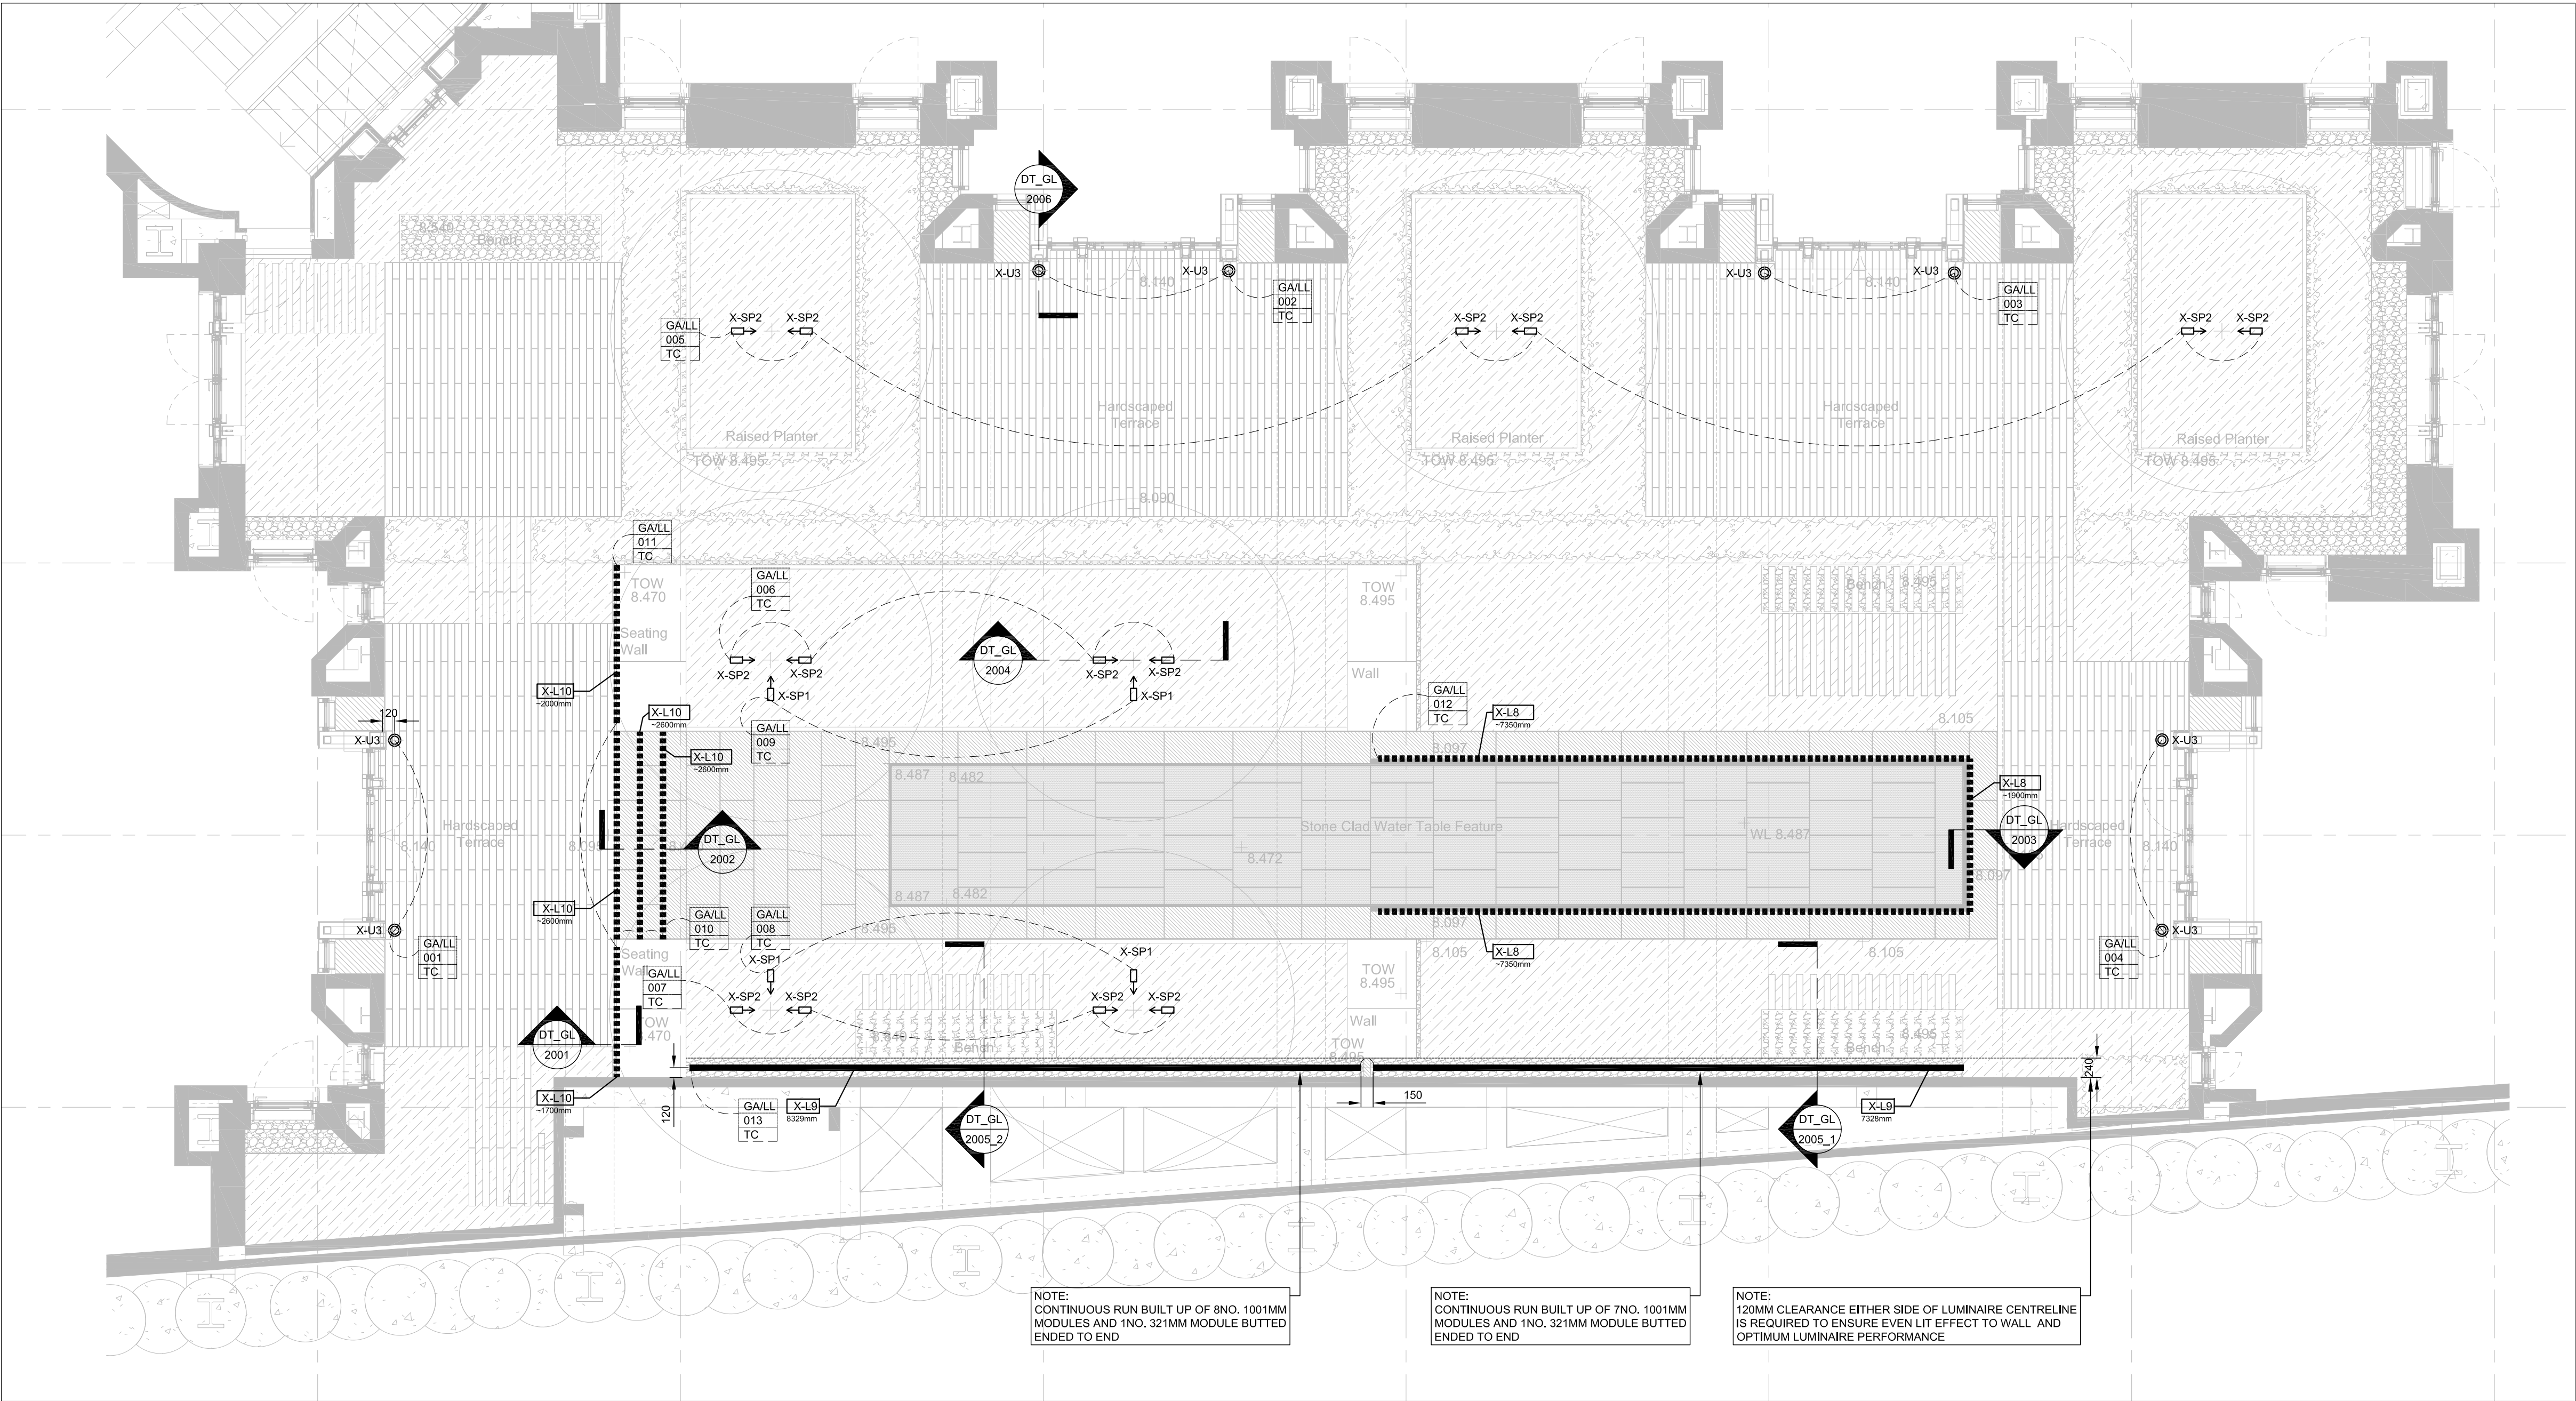

1 - GARDEN LEVEL - GA - SCALE 1:50

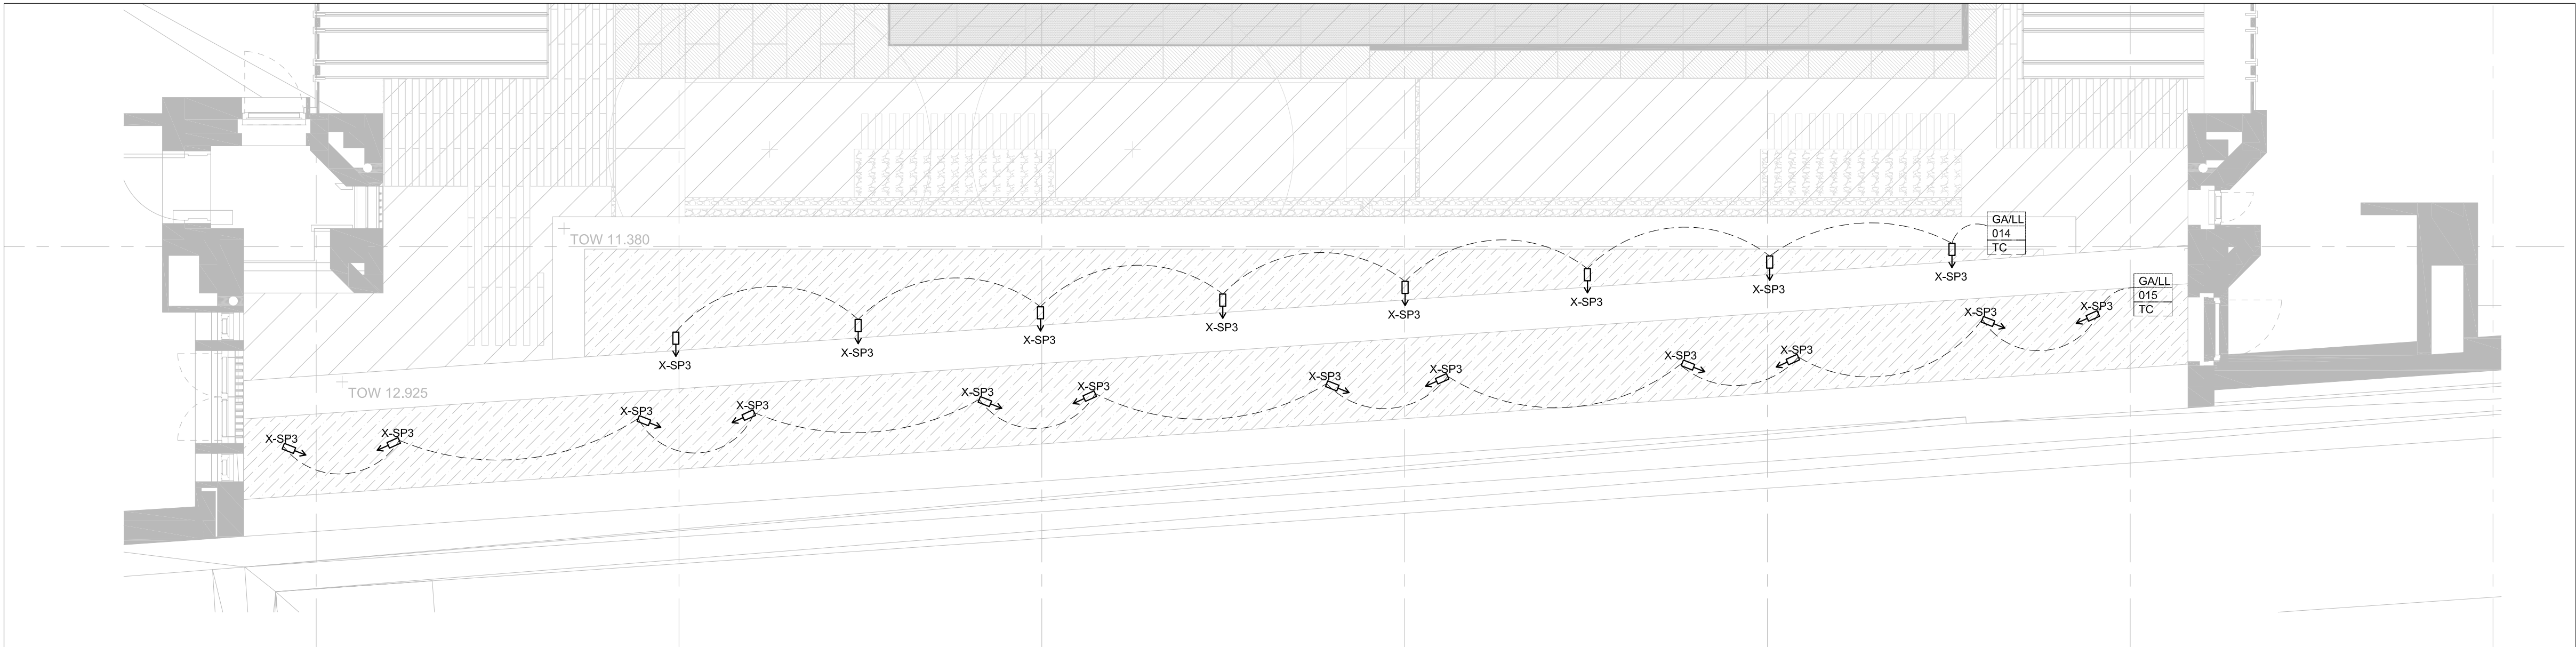

2 - RAISED GARDEN - GA - FEATURE WALL SCALE 1:50

LIGHTING KEY (SYMBOLS NOT TO SCALE)	
Floor mounted 5 Amp socket	Wall mounted 5 Amp socket
Recessed downlight	Surface-mounted downlight
Wallwash (critical dimensions as indicated)	Gimbal
Surface-mounted spotlight	Track-mounted spotlight
Pendant	Table/floor luminaire
Lighting track	Fluorescent batten
Linear light source (direct view)	Linear light source (concealed)
Recessed modular luminaire	Linear tag - approximate dimension in mm
Recessed wall light	Surface-mounted wall light
Ground-recessed uplight	Bollard
Lighting column	Street luminaire
Lighting control group	Lighting control panel
Sensor	Centre Line - for alignment

The drawing is based on dwgs ref:
GPB-312-P-1000 received on 07.03.19
GPB-312-P-1001 received on 07.03.19

P5	Stage 4 Issue revision	26.03.19	AM/VM
P4	Stage 4 Issue	12.12.18	BB/VM
P3	Stage 4 Issue	27.07.18	AM/VM
P2	Stage 4 Issue	16.07.18	AM/VM
P1	Stage 4 Issue	04.07.18	AM/VM
REV	DESCRIPTION	DATE	BY

NOTE: Drawing to be read in conjunction with the latest revision of GIA Equation's equipment specification schedule:
2503_SPEC Shell and Core (Latest Issue)

All dimensions to be verified by the contractor on site. Do not scale from this drawing.

This is not a construction drawing. Where critical to lighting design, specific setting out dimensions for the particular luminaires are indicated on this drawing and are to be adhered to. Proposed lighting construction drawing including all final setting out dimensions and details to be issued by the contractor for GIA Equation review and comment in good time before the lighting installation on site.

All electrical works associated with this drawing to be in accordance with the latest edition of IEE wiring regulations and electrical engineer's specification. For emergency and exit lighting please refer to engineer's design documentation.

THIS DRAWING IS PROPERTY OF GIA EQUATION

All copyright is reserved and the drawing is issued on the condition that it is not copied, reproduced, retained or disclosed to any unauthorised person, either wholly or in part without the consent of GIA Equation.

Client:
Brockton Capital

Project:
**Project TT
60 Curzon Street**

Area:
**Landscape
Garden and Raised Garden**

Drawing Title:
**Garden Landscape
Low Level Lighting Layout**

Filename:
2503_GA_Landscape

Scale:	Job No:	Created on:
1:50 @A1	2503	29.05.2018
Rev. No:	Drawn By:	Checked By:
P5	AM	VM

GIA Equation
17 Ribborough Street, London SE1 0HG
T 020 3772 2760
info@giaeuation.co.uk

**gIA
EQUATION**