



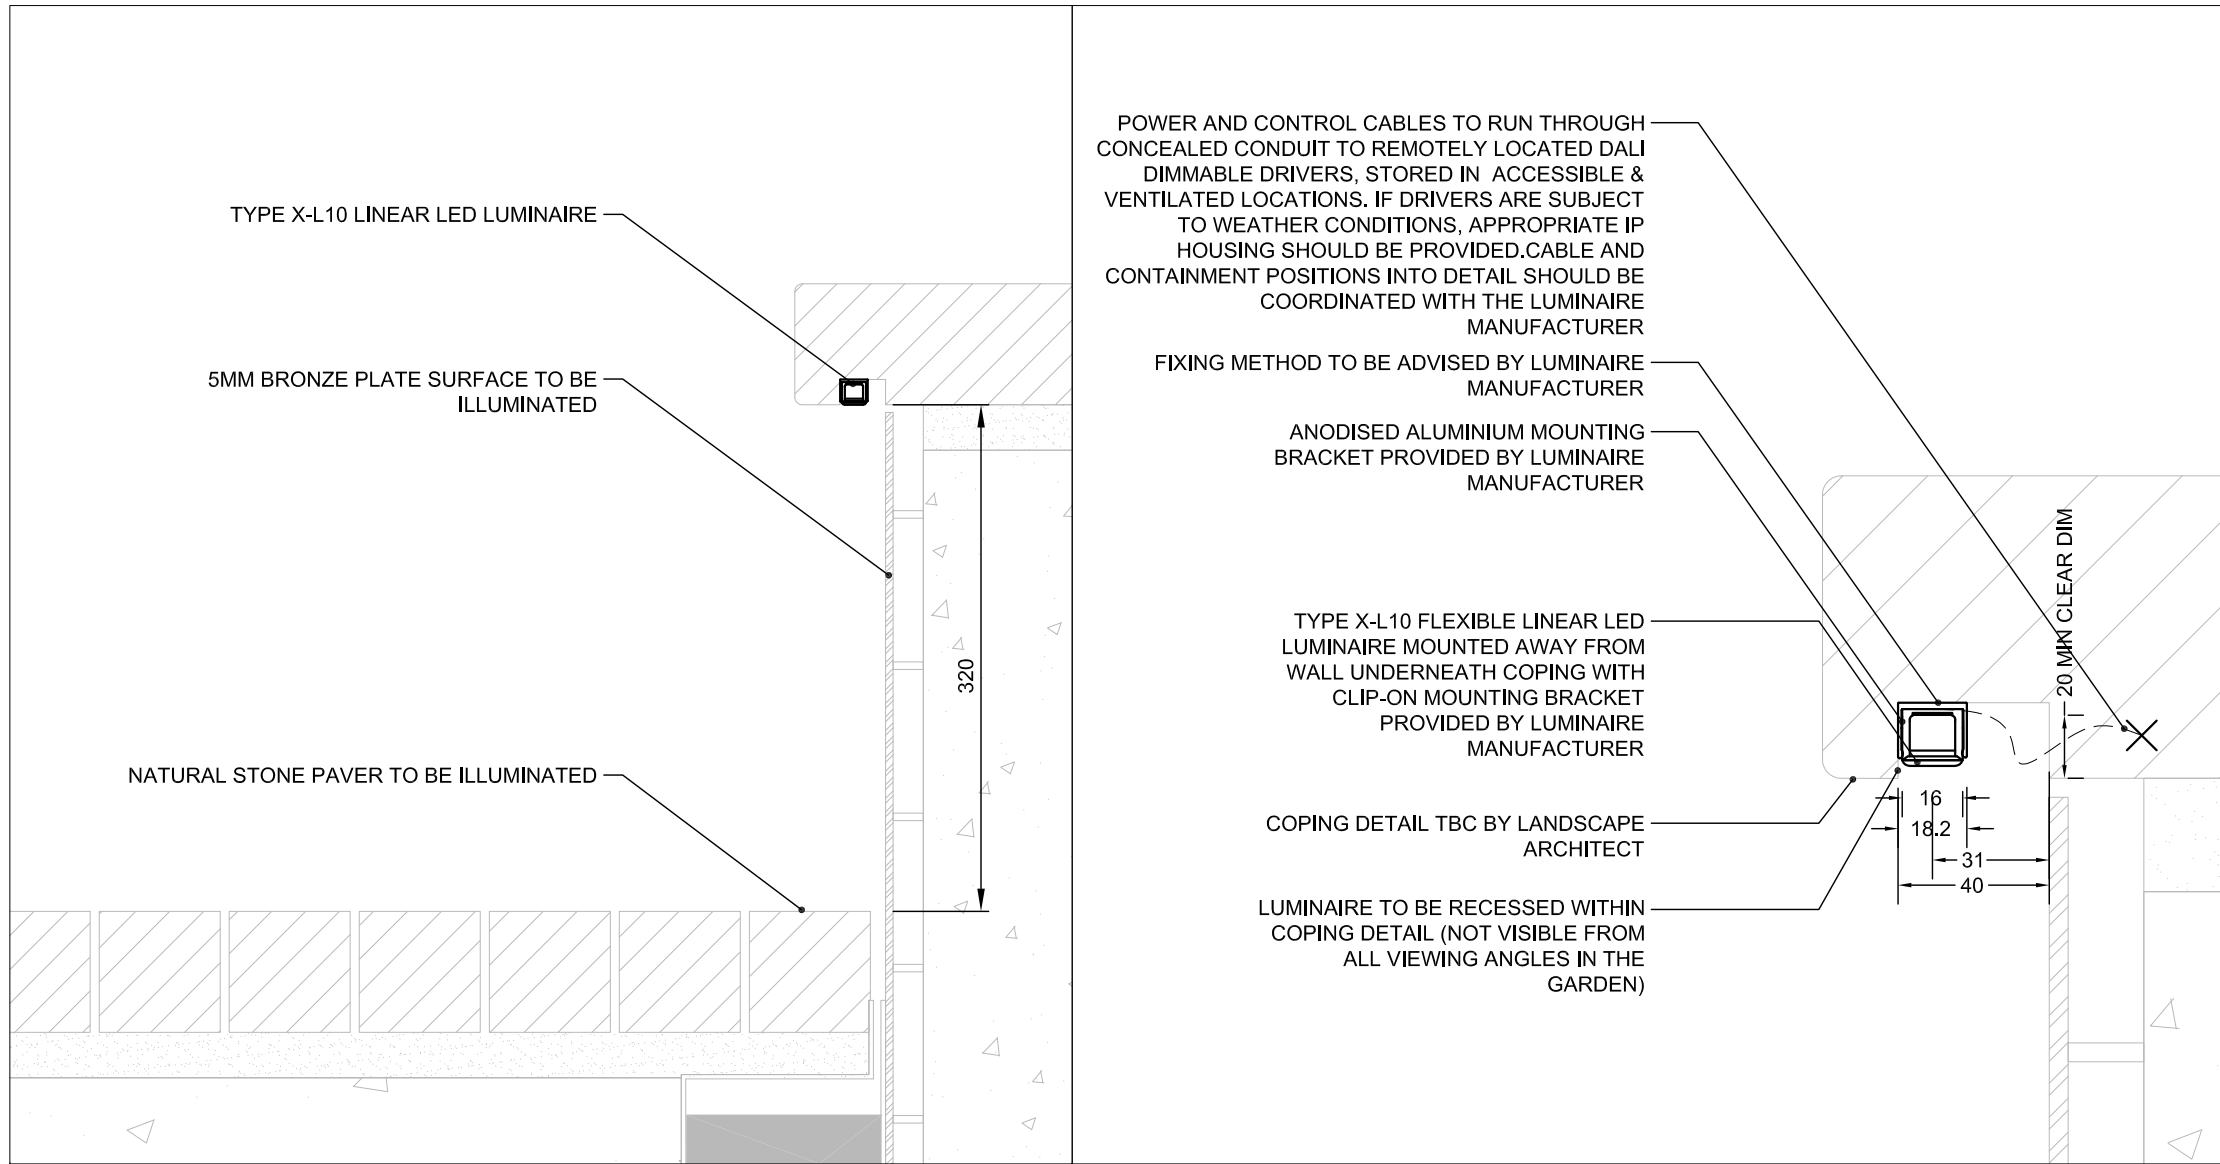

2001 - 1 - SEATING WALL - SCALE 1:5


2001 - 2 - SEATING WALL - SCALE 1:2

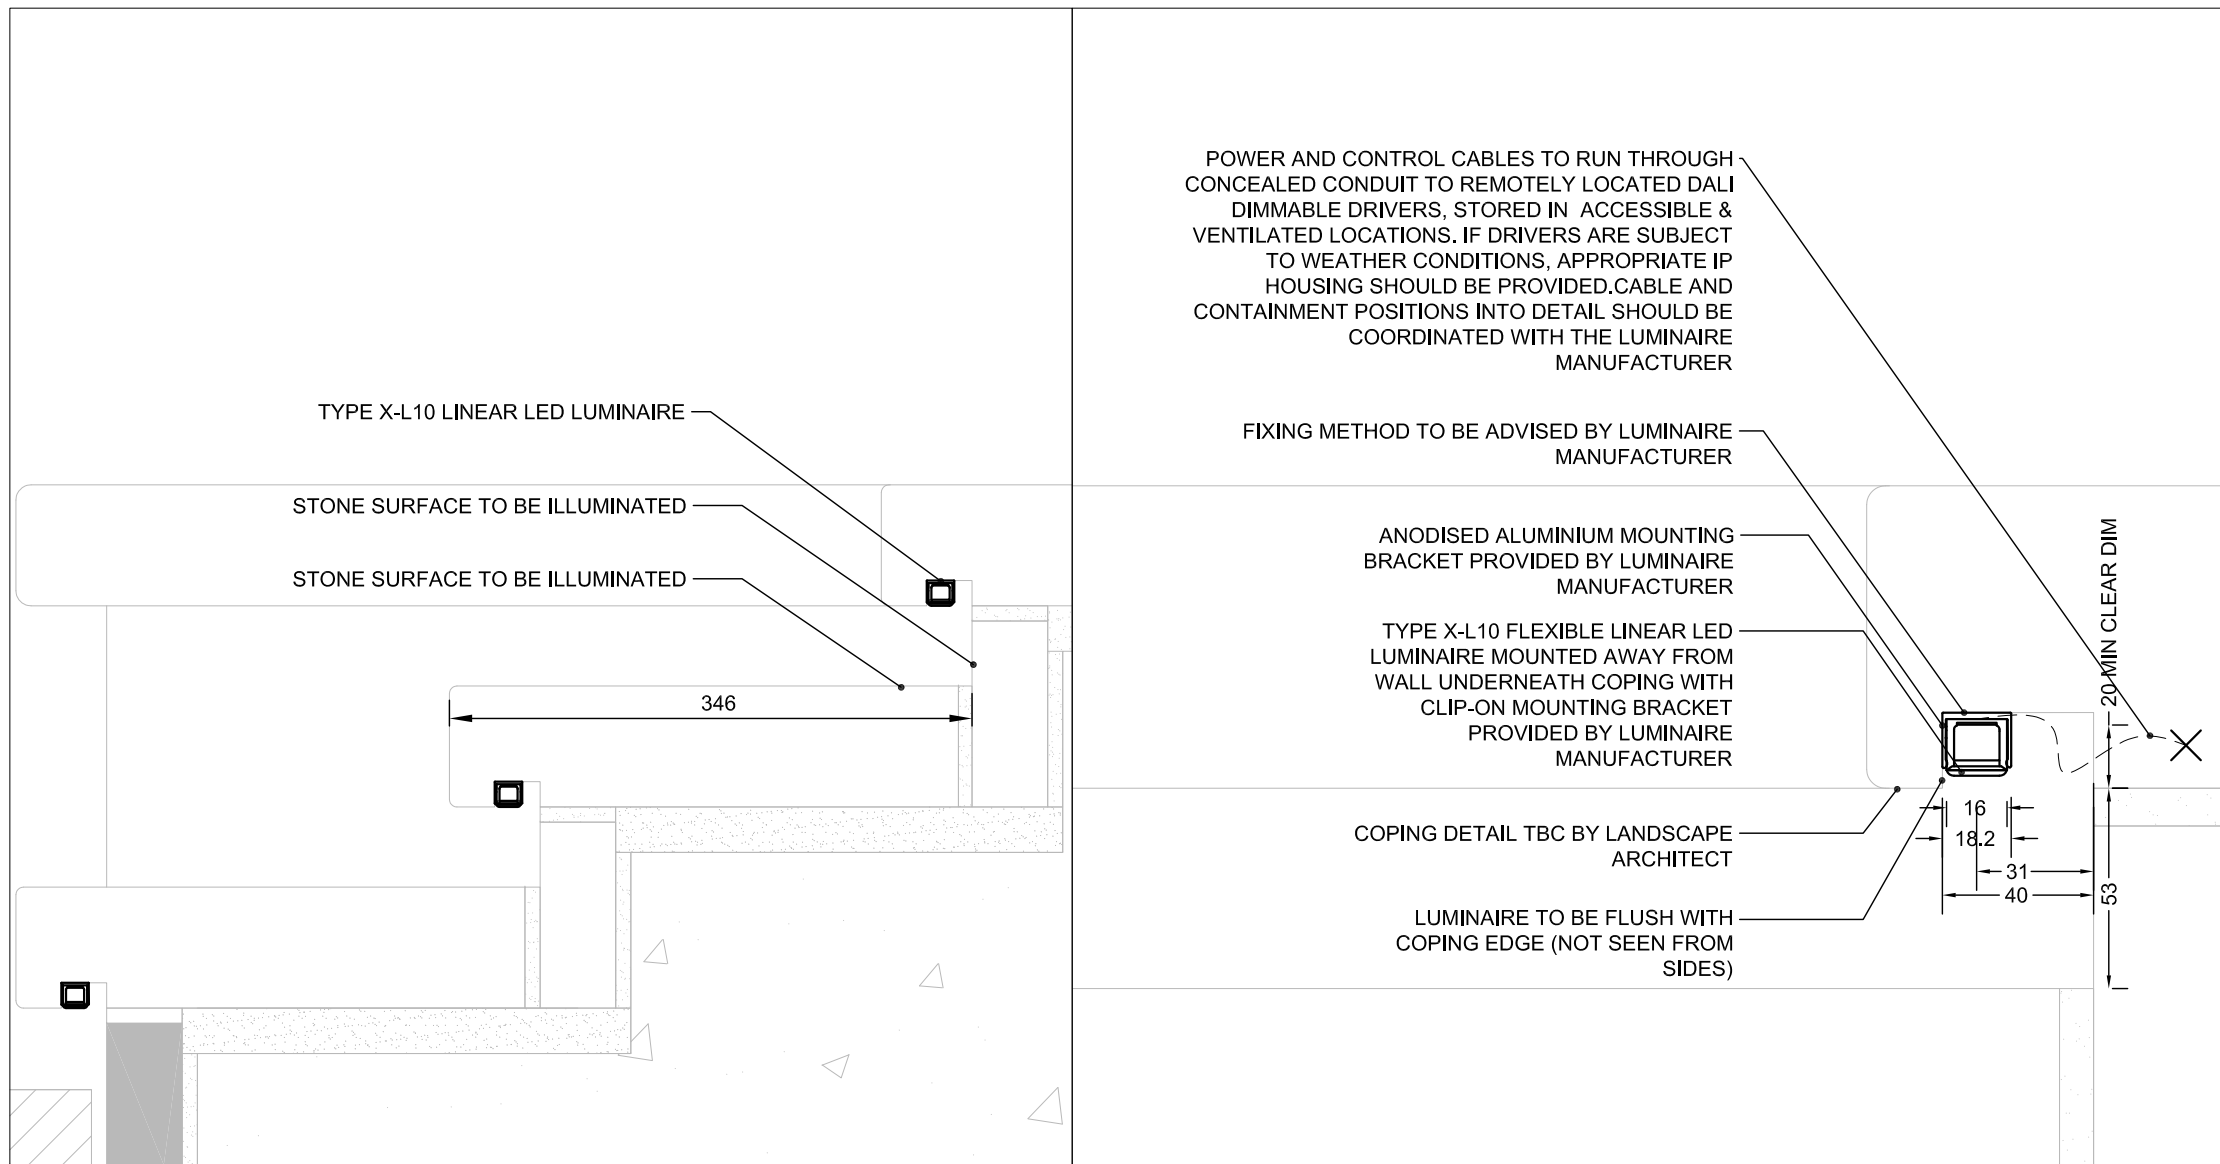

2002 - 1 - STEPS - SCALE 1:5

NOTE: FINAL DETAILED DESIGN TO BE CONFIRMED AFTER MOCK-UP POST STAGE 4 ISSUE


2002 - 2 - STEPS - SCALE 1:5

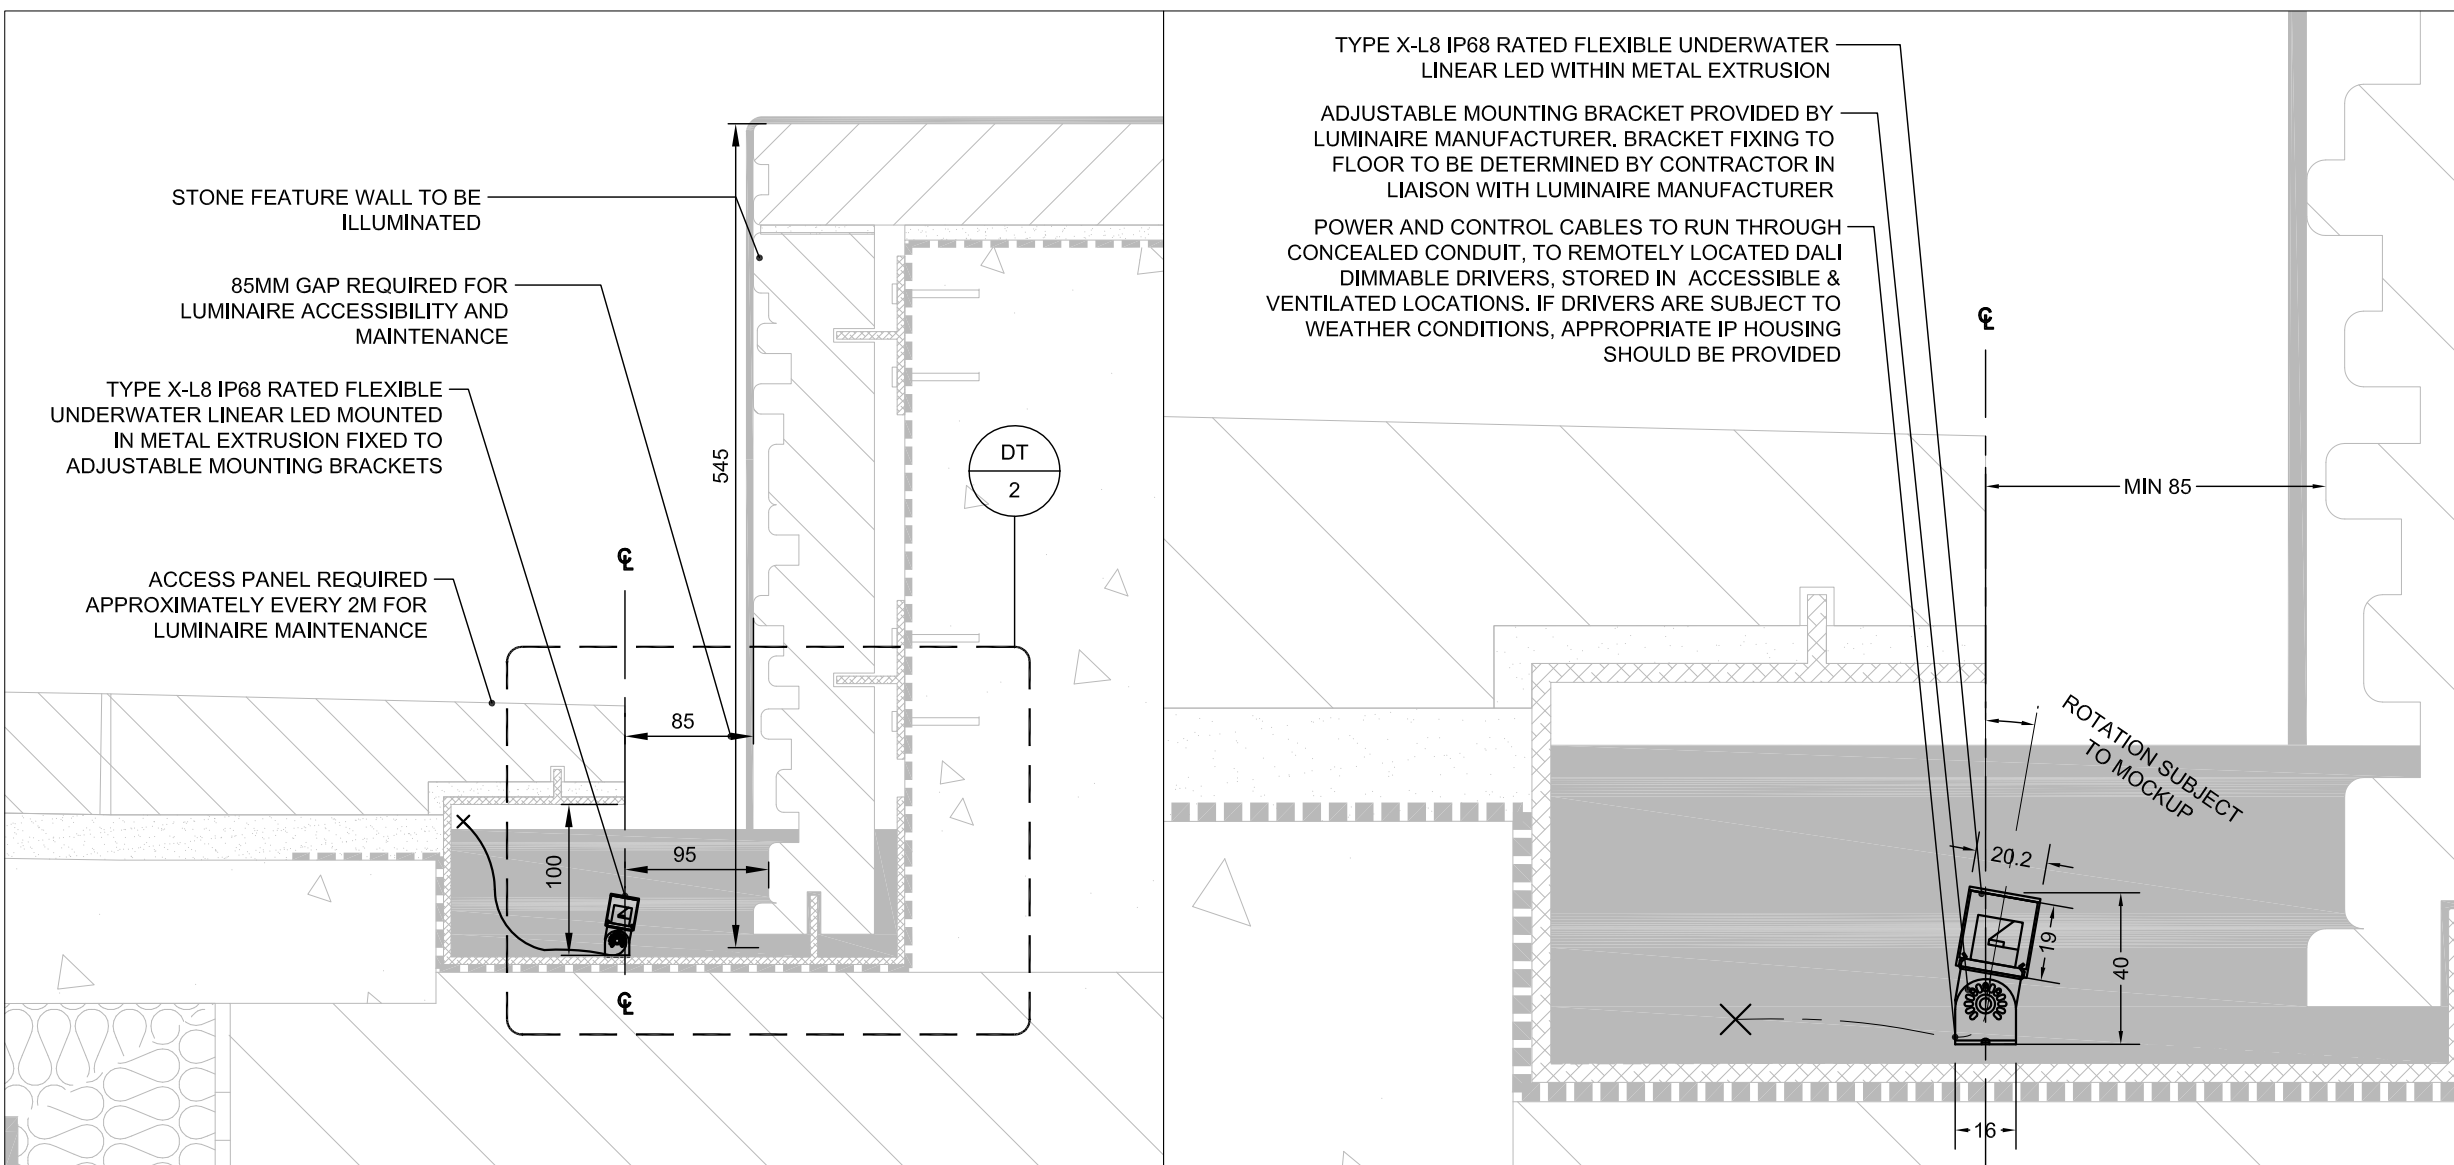


2003 - 1 - WATER FEATURE - SCALE 1:5

NOTE: FINAL DETAILED DESIGN TO BE CONFIRMED AFTER MOCK-UP OF CORNER (1M X 1M) POST STAGE 4 ISSUE


2003 - 2 - WATER FEATURE - SCALE 1:2

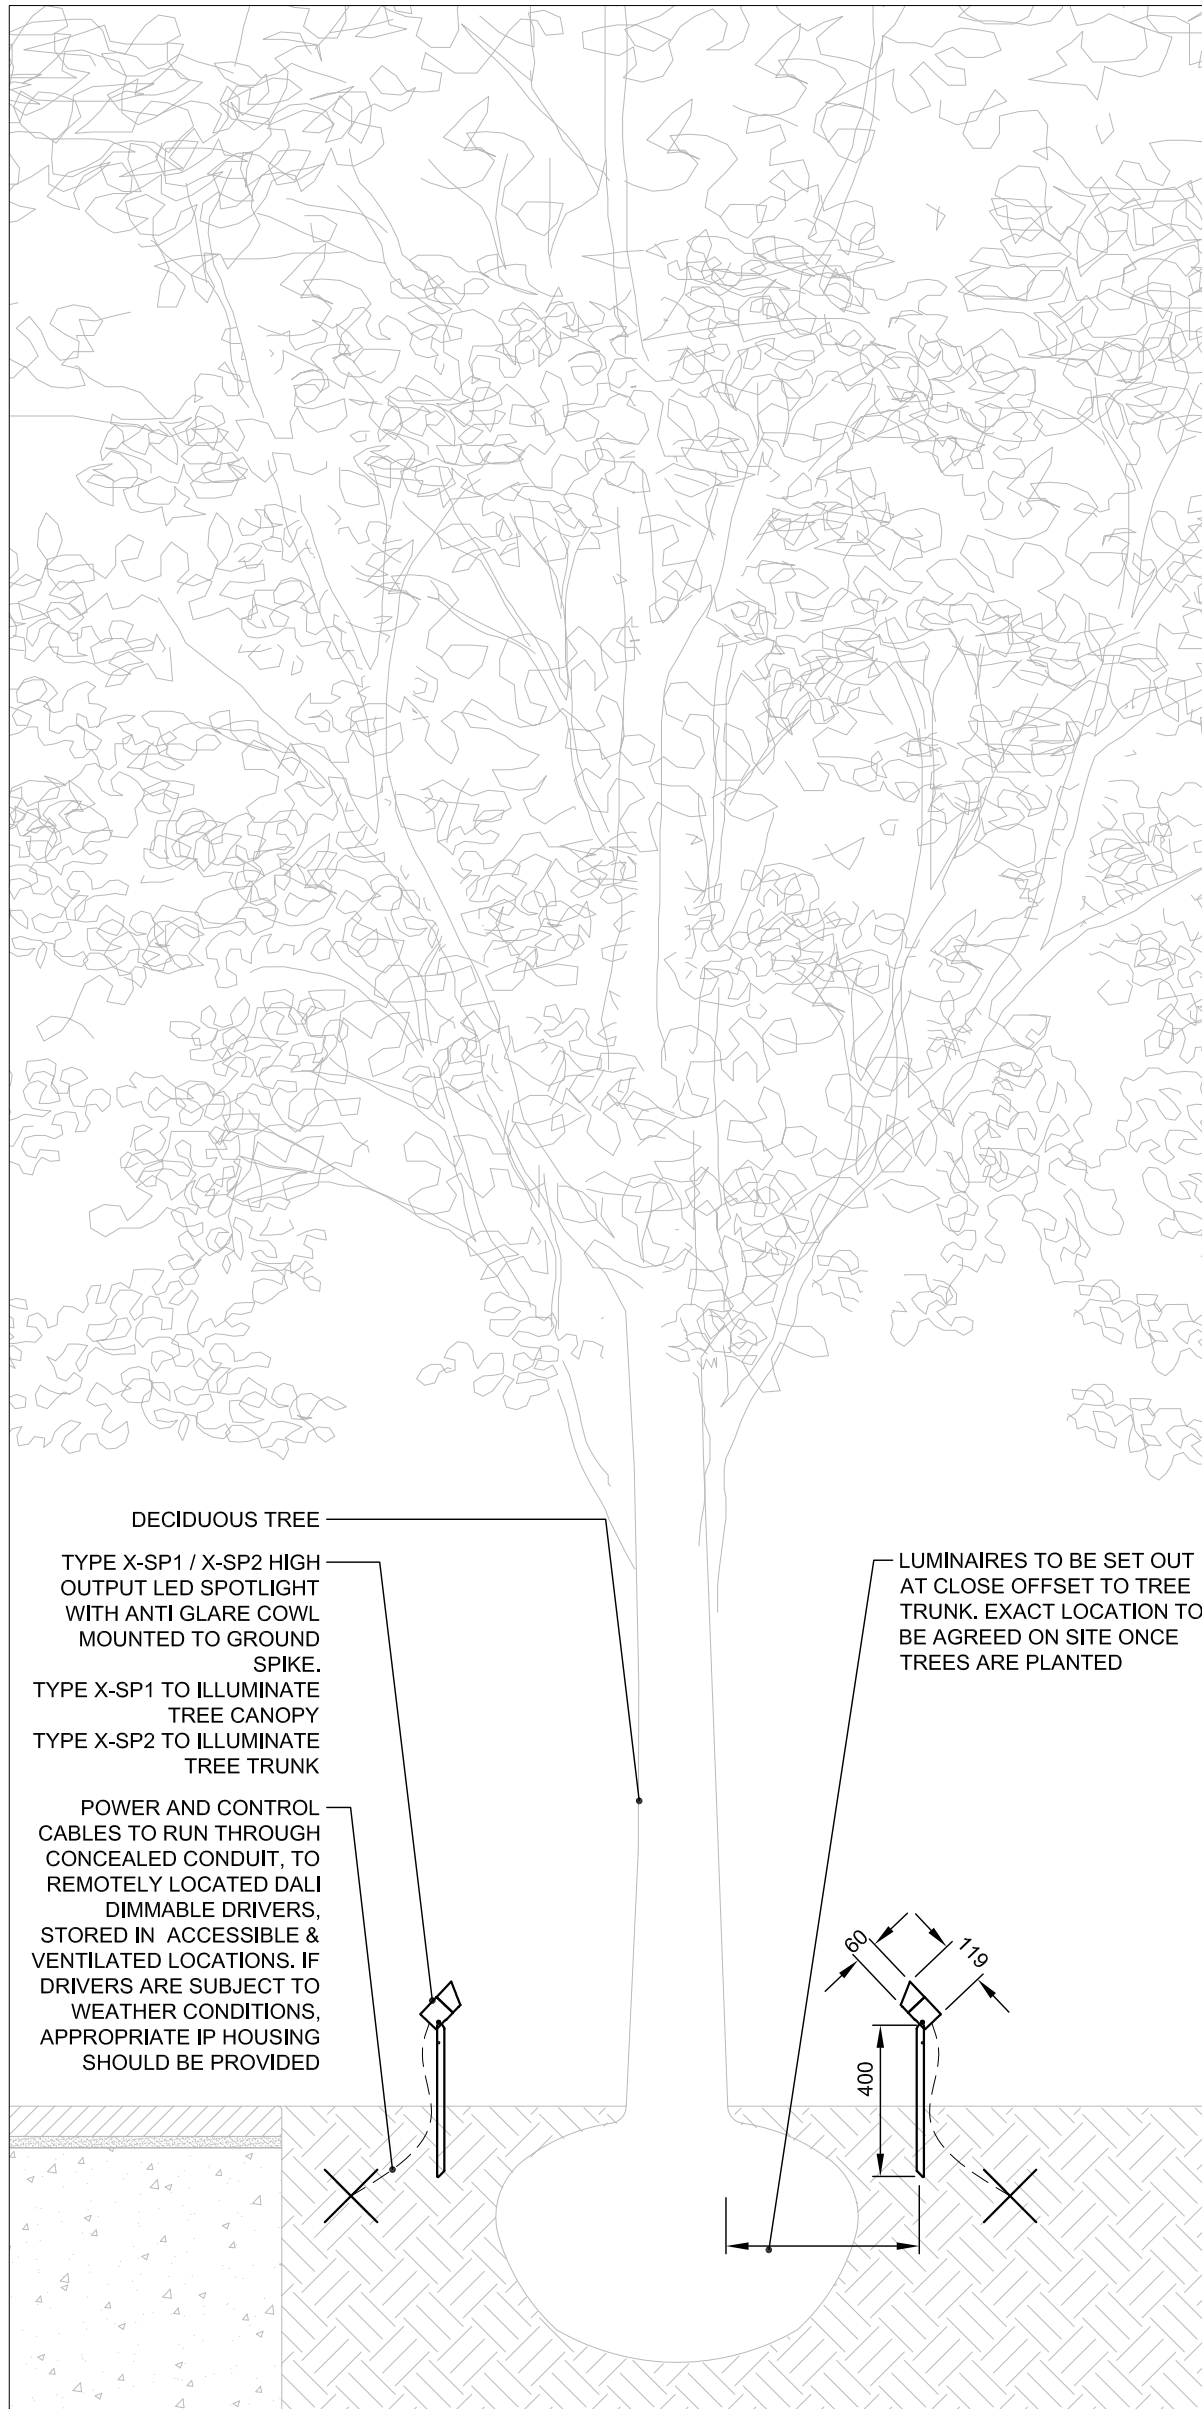


2004 - 1 - TREES - SCALE 1:20

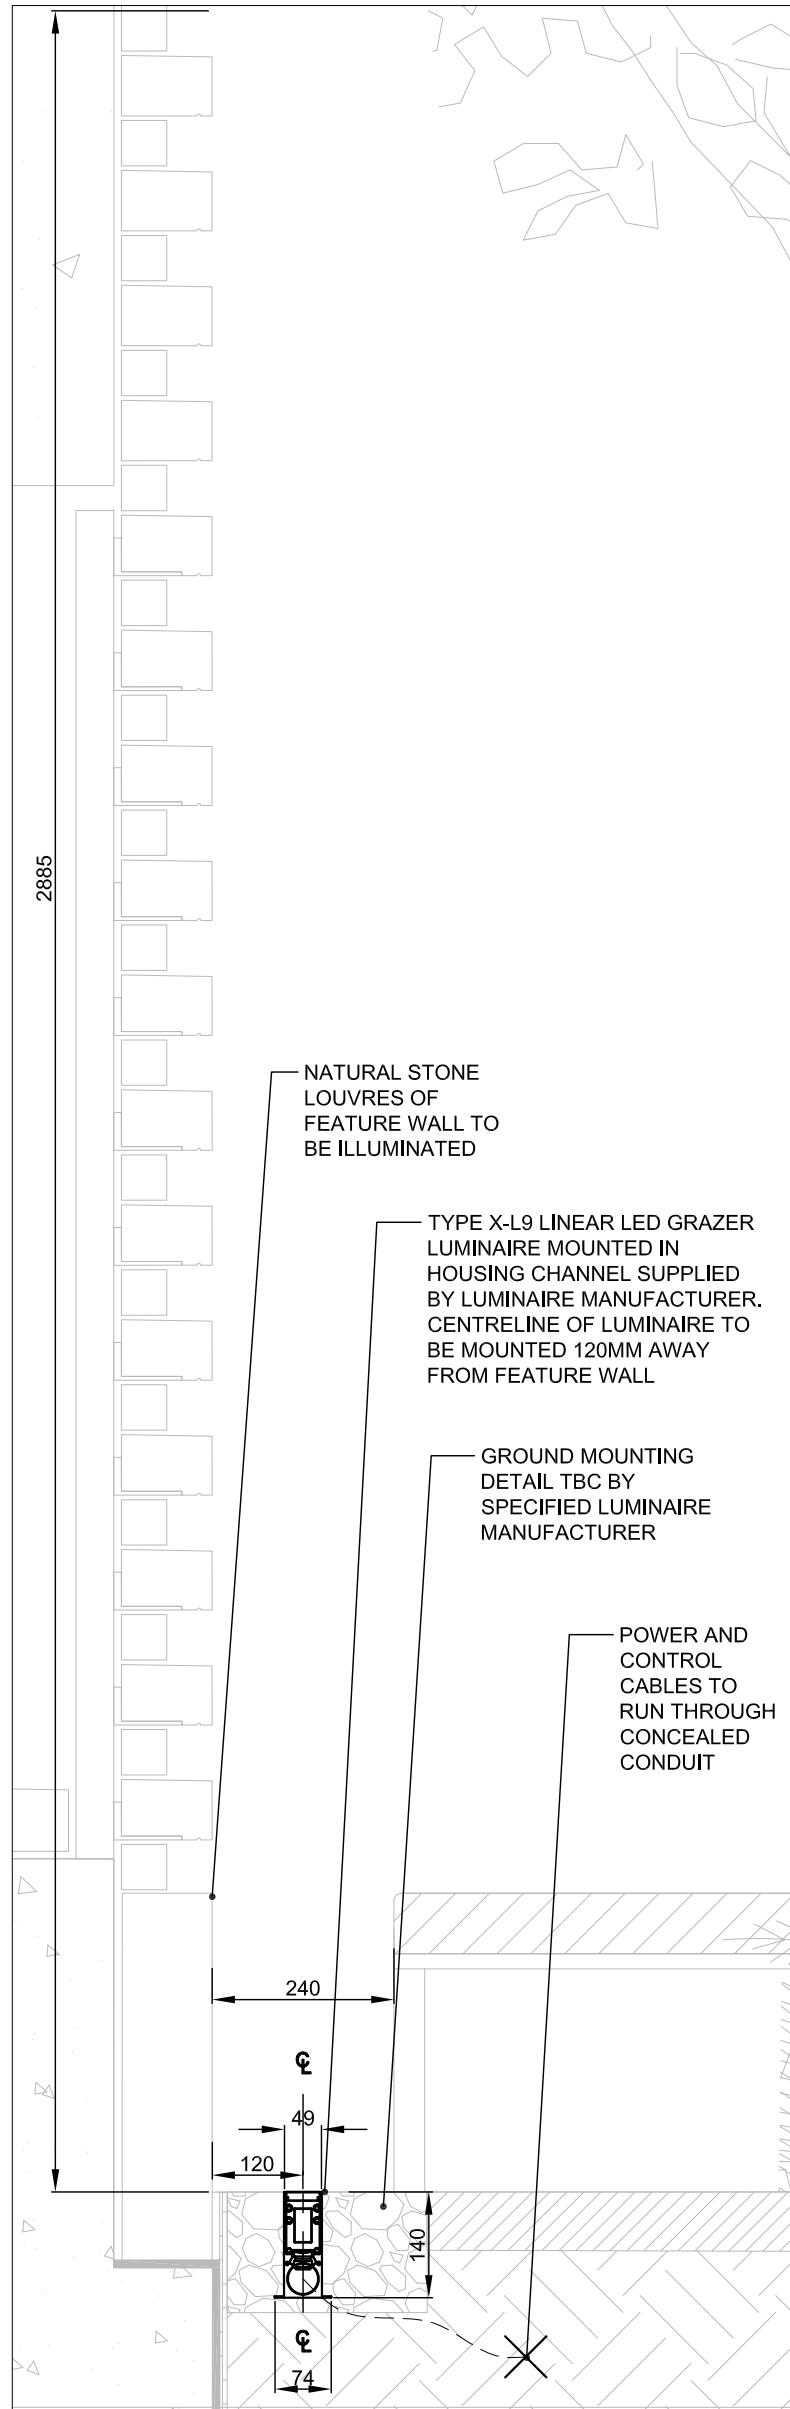


2005 - 1 - FEATURE WALL - SCALE 1:10

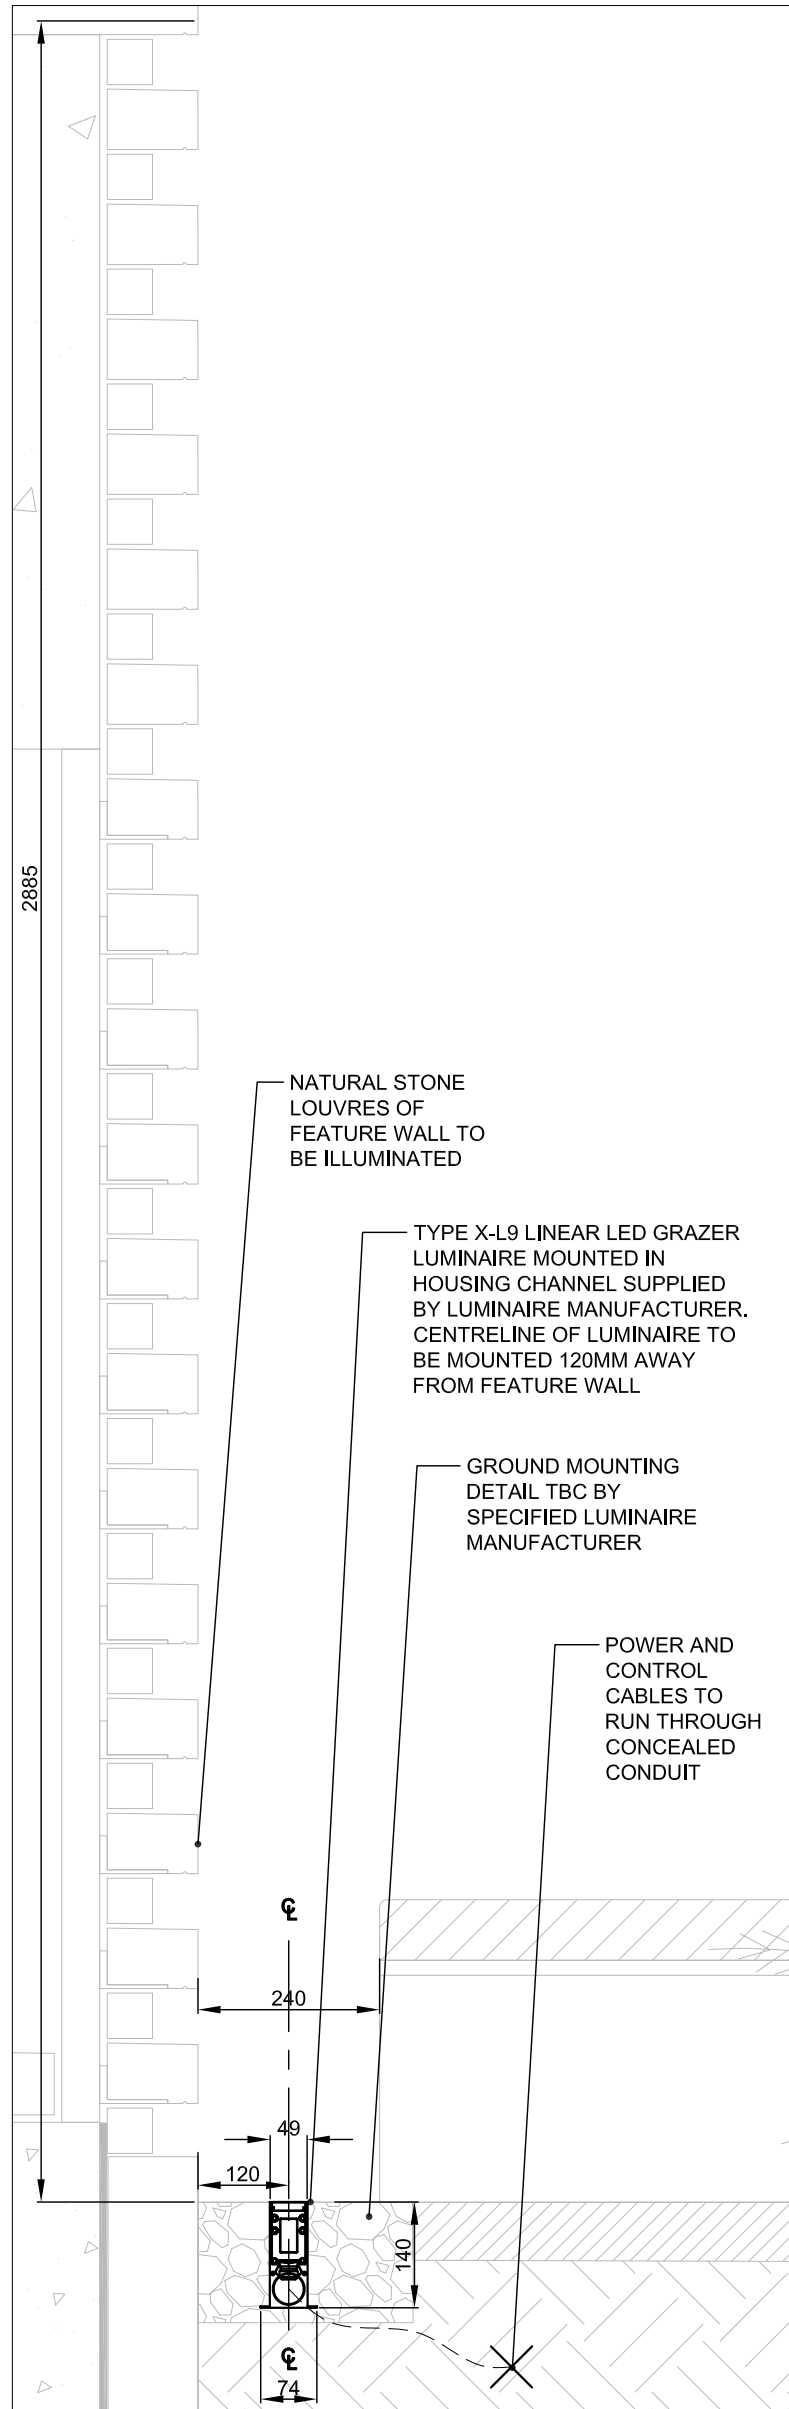

2005 - 2 - FEATURE WALL - SCALE 1:10

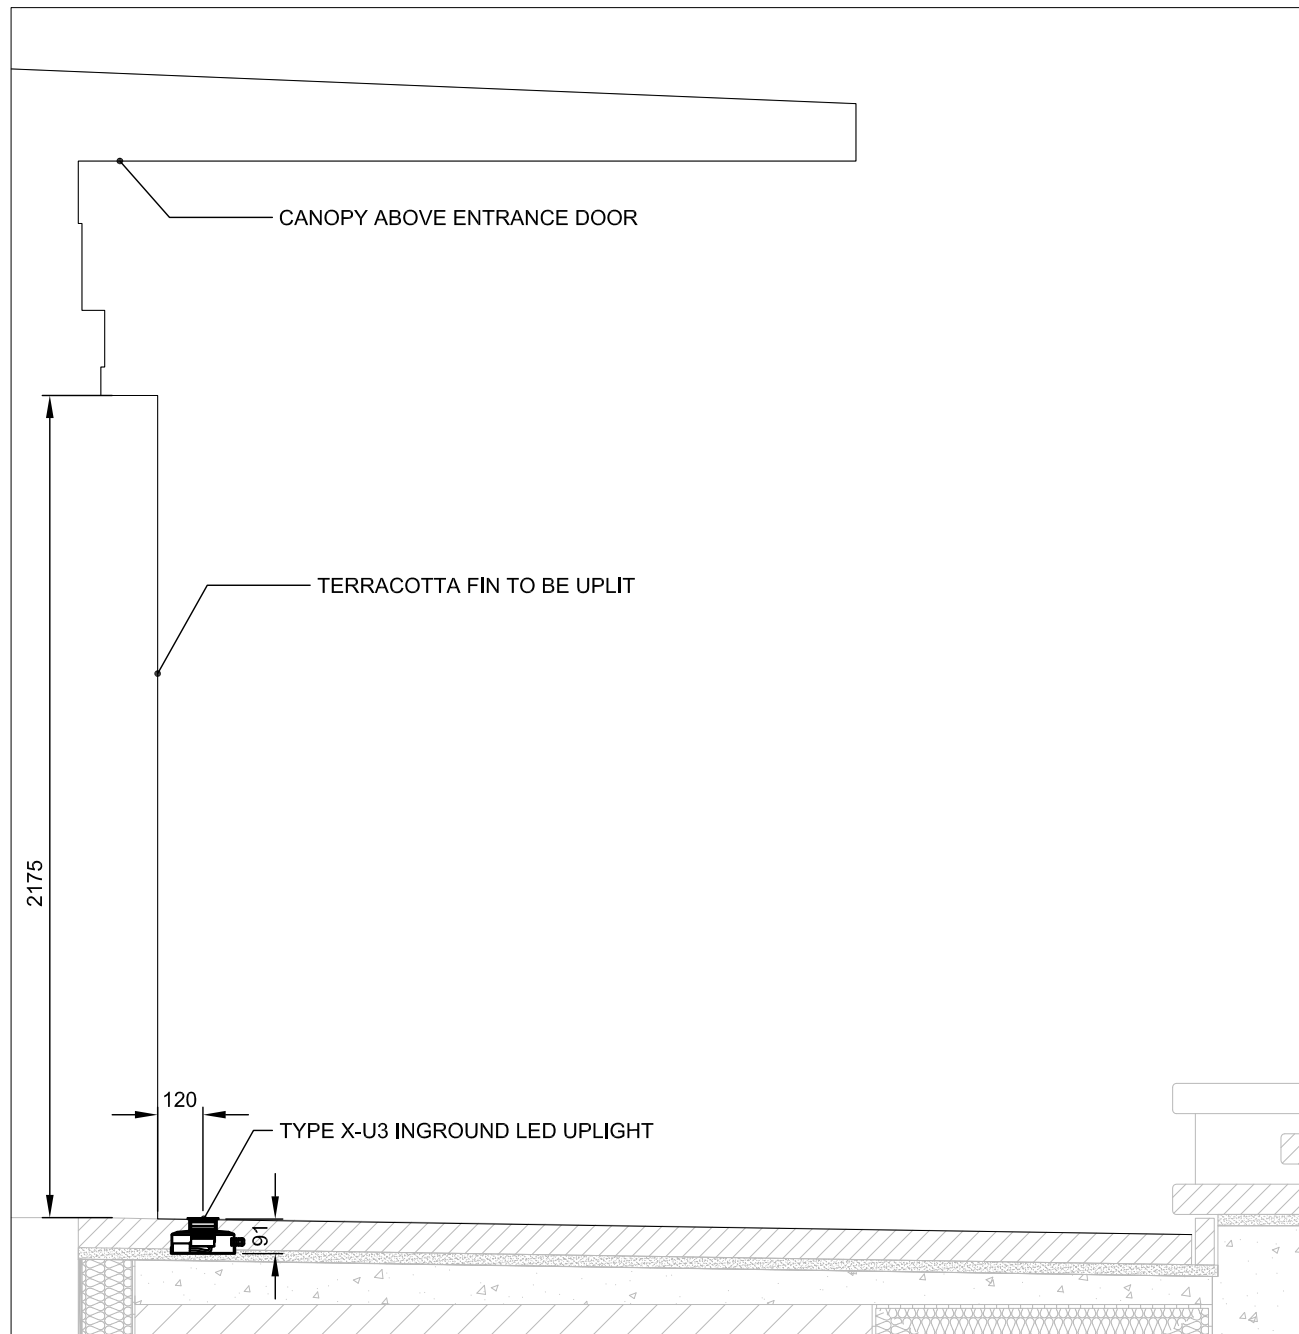

2006 - 1 - TERRACOTTA FIN - SCALE 1:20

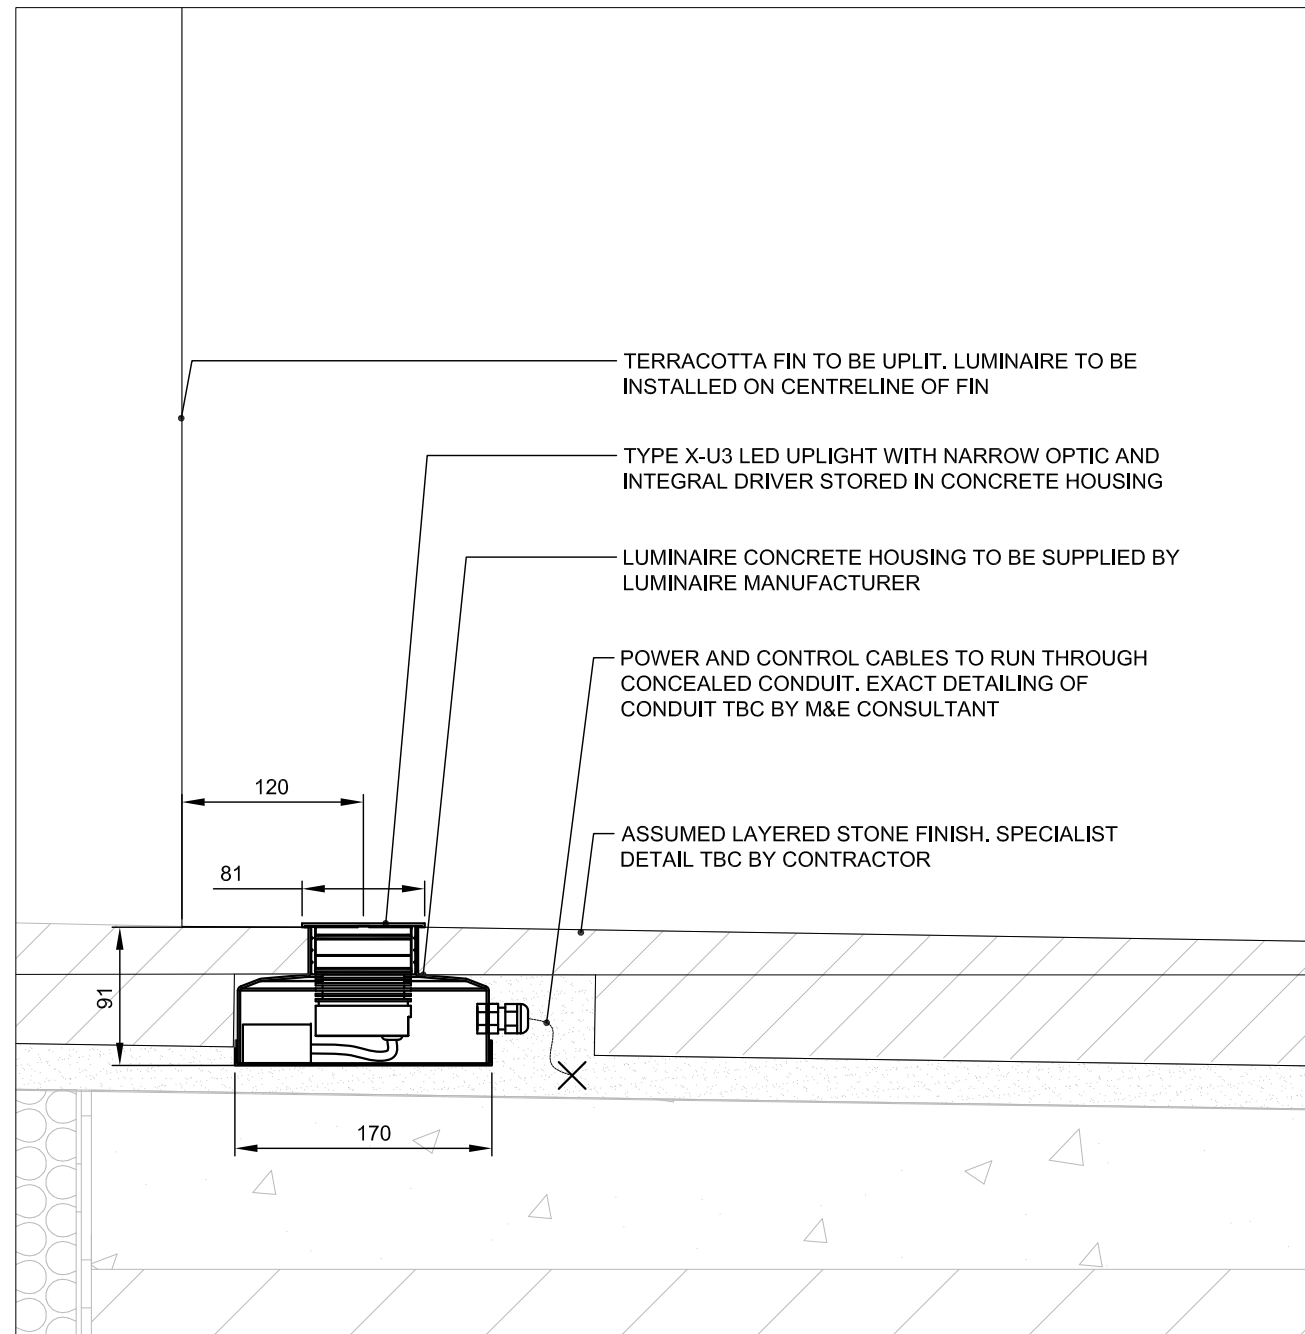

2006 - 2 - TERRACOTTA FIN - SCALE 1:5

LIGHTING KEY (SYMBOLS NOT TO SCALE)	
☐ Floor mounted 5 Amp socket	☐ Wall mounted 5 Amp socket
☐ Recessed downlight	☐ Surface-mounted downlight
☐ Wallwash (critical dimensions as indicated)	☐ Gimbal
☐ Surface-mounted spotlight	☐ Track-mounted spotlight
☐ Pendant	☐ Table/floor luminaire
--- Lighting track	--- Fluorescent batten
--- Linear light source (direct view)	--- Linear light source (concealed)
☐ Recessed modular luminaire	☐ Linear tag - approximate dimension in mm
☐ Recessed wall light	☐ Surface-mounted wall light
☐ Ground-recessed uplight	☐ Bollard
☐ Lighting column	☐ Street luminaire
☐ Lighting control group	☐ Lighting control panel
☐ Sensor	☐ Centre Line - for alignment

The drawing is based on dwgs ref:
GPB-312-D-4110 received 07.03.19
GPB-312-D-4030 received 07.03.19
GPB-312-S-3010 received 07.03.19
GPB-312-D-4400 received 07.03.19
GPB-312-S-3012 received 07.03.19

NOTES:

1: DRIVER(S) TO BE INSTALLED IN DRY AND WELL VENTILATED LOCATION. ACCESSIBLE FOR MAINTENANCE. CONTRACTOR TO CONFIRM LOCATION ON SITE. REFER TO LIGHTING MANUFACTURER REQUIREMENTS FOR MAX. DISTANCE BETWEEN DRIVERS AND LUMINAIRES.

2: ALL CONNECTION CABLES TO BE NEATLY CLIPPED IN PLACE TO AVOID SHADOWING ON TO THE SOFFIT SURFACES.

3: REFER TO GIA EQUATION'S LIGHTING LAYOUTS FOR FURTHER INFORMATION ON QUANTITIES AND LUMINAIRE LOCATIONS.

P3	Stage 4 Issue Revision	26.03.19	AM/VM
P2	Stage 4 Issue	16.07.18	AM/VM
P1	Stage 4 Issue	04.07.18	AM/VM
REV	DESCRIPTION	DATE	BY

NOTE: Drawing to be read in conjunction with the latest revision of GIA Equation's equipment specification schedule:
2503_SPEC Shell and Core (Latest Issue)

All dimensions to be verified by the contractor on site. Do not scale from this drawing. This is not a construction drawing. Where critical to lighting design, specific setting out dimensions for the particular luminaires are indicated on this drawing and are to be adhered to. Proposed lighting construction drawing including all final setting out dimensions and details to be issued by the contractor for GIA Equation review and comment in good time before the lighting installation on site.

All electrical works associated with this drawing to be in accordance with the latest edition of IEE wiring regulations and electrical engineer's specification. For emergency and exit lighting please refer to engineer's design documentation.

THIS DRAWING IS PROPERTY OF GIA EQUATION

All copyright is reserved and the drawing is issued on the condition that it is not copied, reproduced, retained or disclosed to any unauthorised person, either wholly or in part without the consent of GIA Equation.

Client:

Brockton Capital

Project:

Project TT
60 Curzon St

Area:

Garden Landscape

Drawing Title:

Garden Landscape Details

Filename:

2503_Landscape Details

Scale:

Various @ A1

Job No:

2503

Created on:

08.06.2018

Rev. No:

P3

Drawn By:

AM

Checked By:

VM

GIA Equation

17 Ribborough Street, London SE1 0HG

T 020 3772 2760

Info@giaequation.co.uk

GIA
EQUATION