



TYPICAL ILLUSTRATION

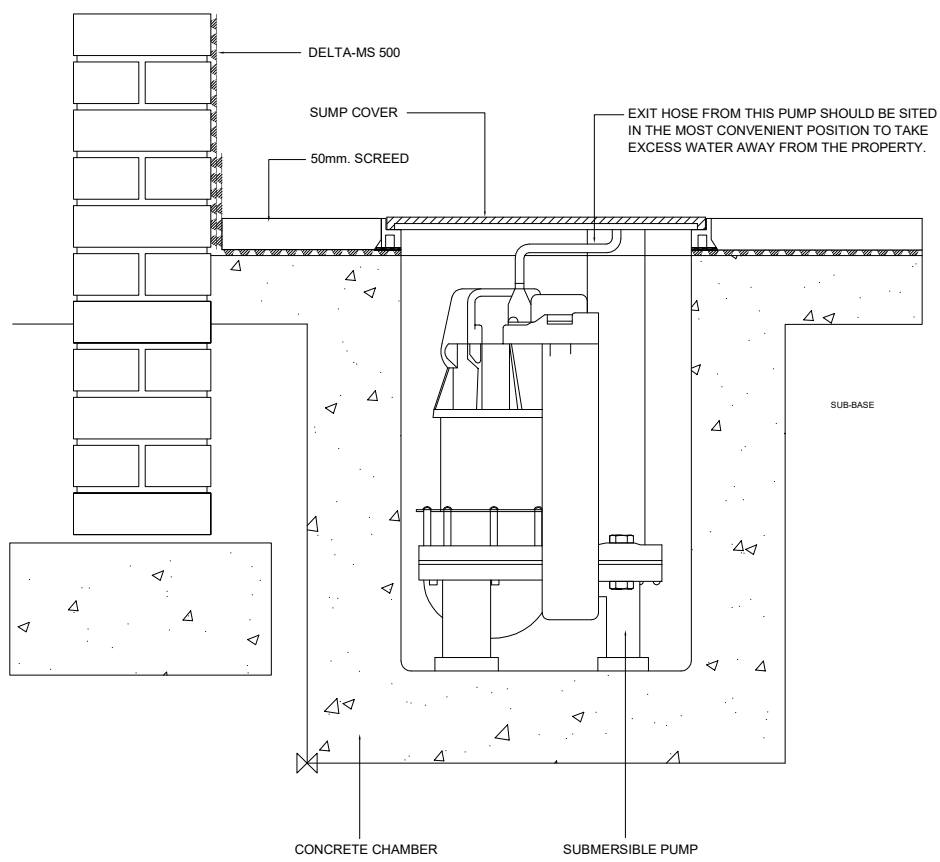

SUMP AND PUMP DETAIL

DELTA - MS
SEALING TO COLUMN BASE

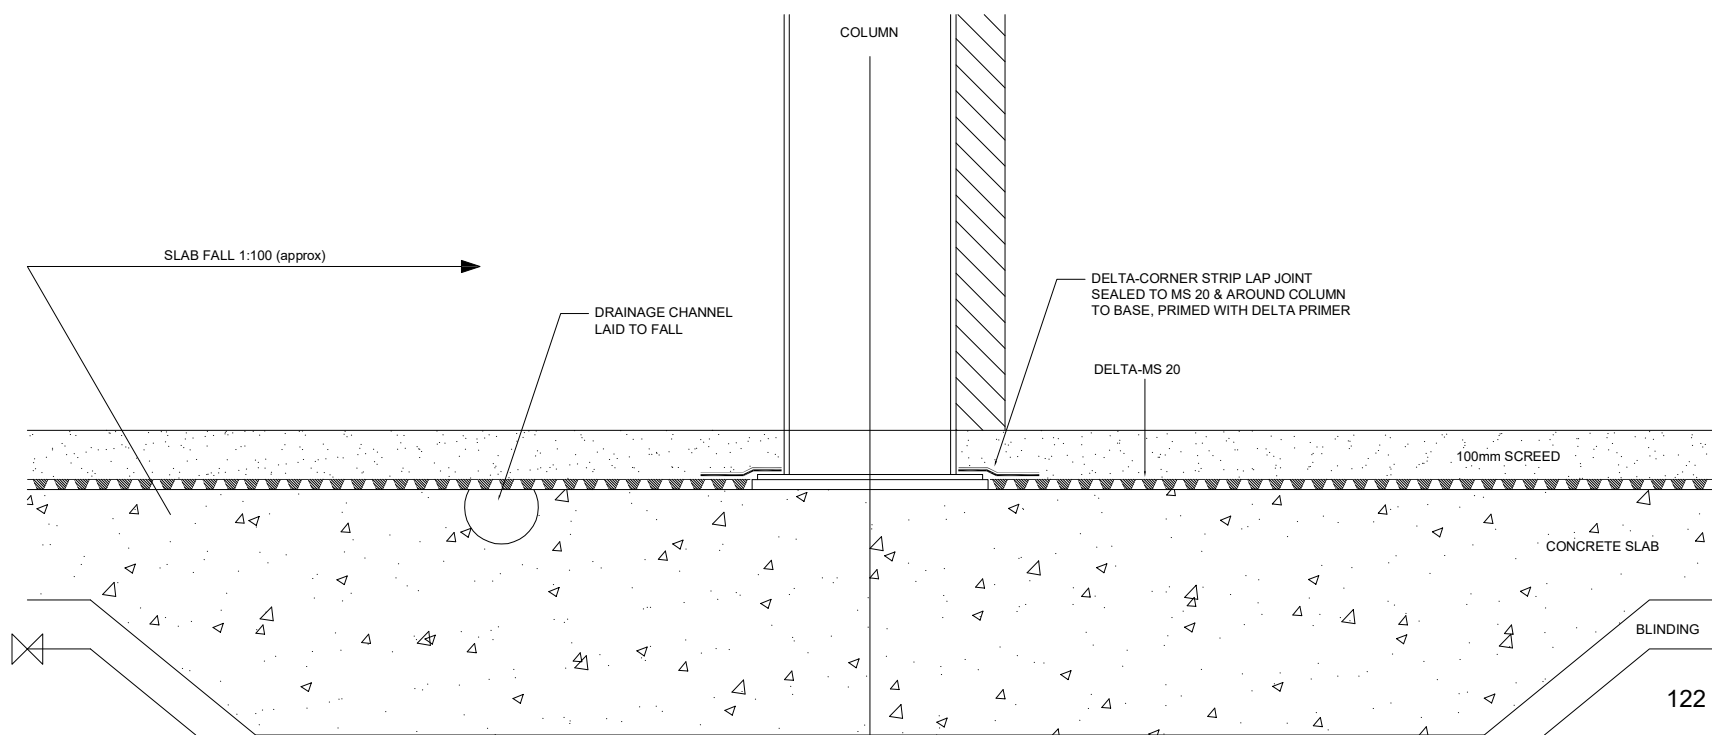

TANKING DETAILS

TITLE	PROPOSED DRAWINGS	ADDRESS	95 MALVERN ROAD LONDON. NW6
CLIENT	Mr. C. NORMAN	SCALE	1:50 @ A3
		DRAWING NO.	190328/26
		DATE	MARCH 2019
		REV.	