




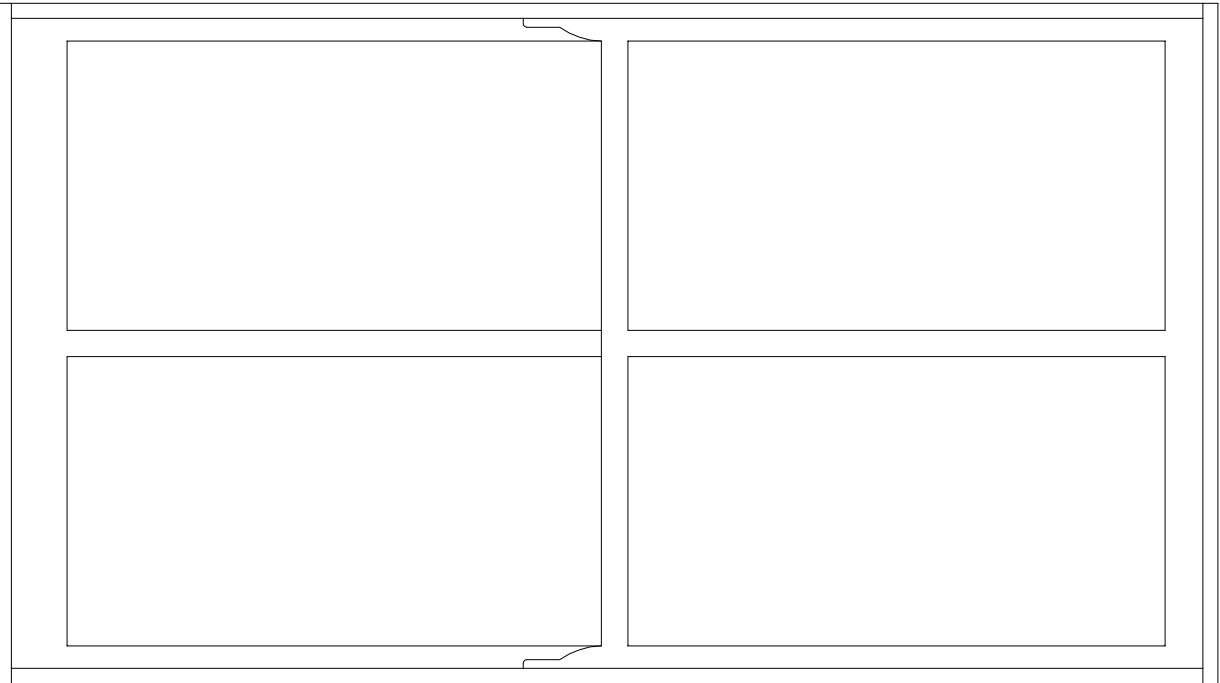

ELEVATION

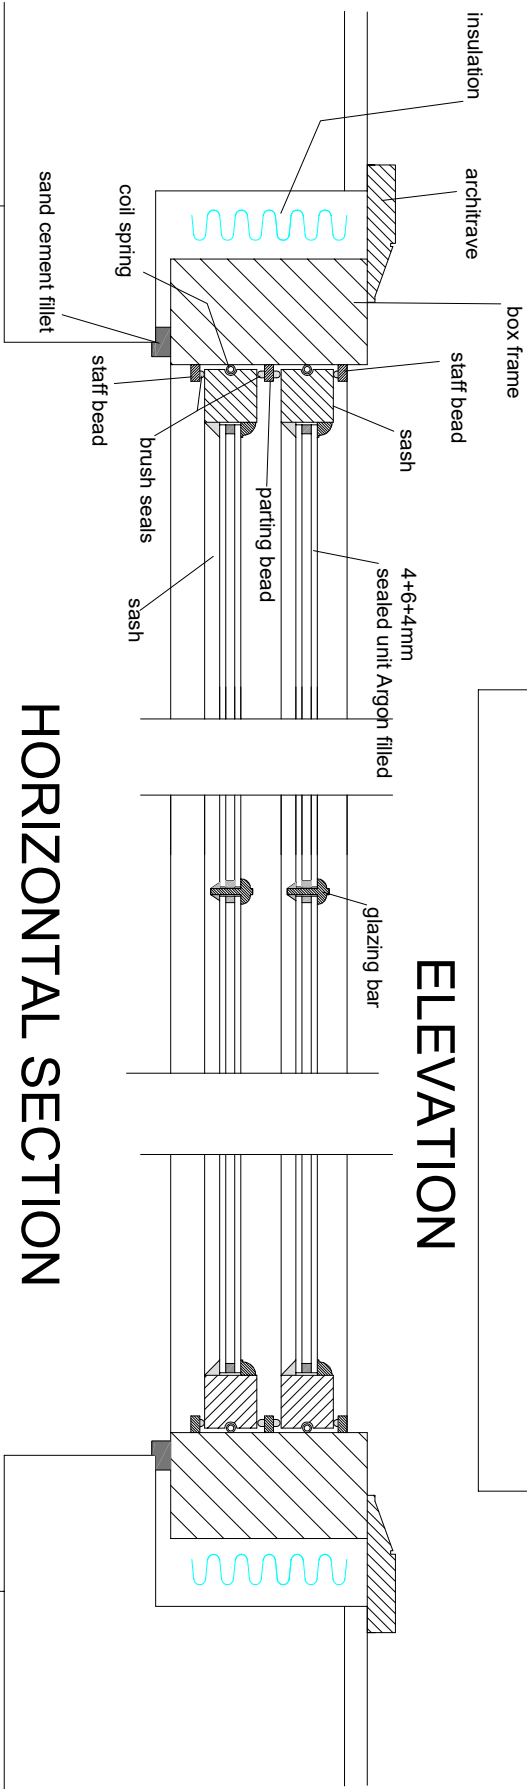

HORIZONTAL SECTION

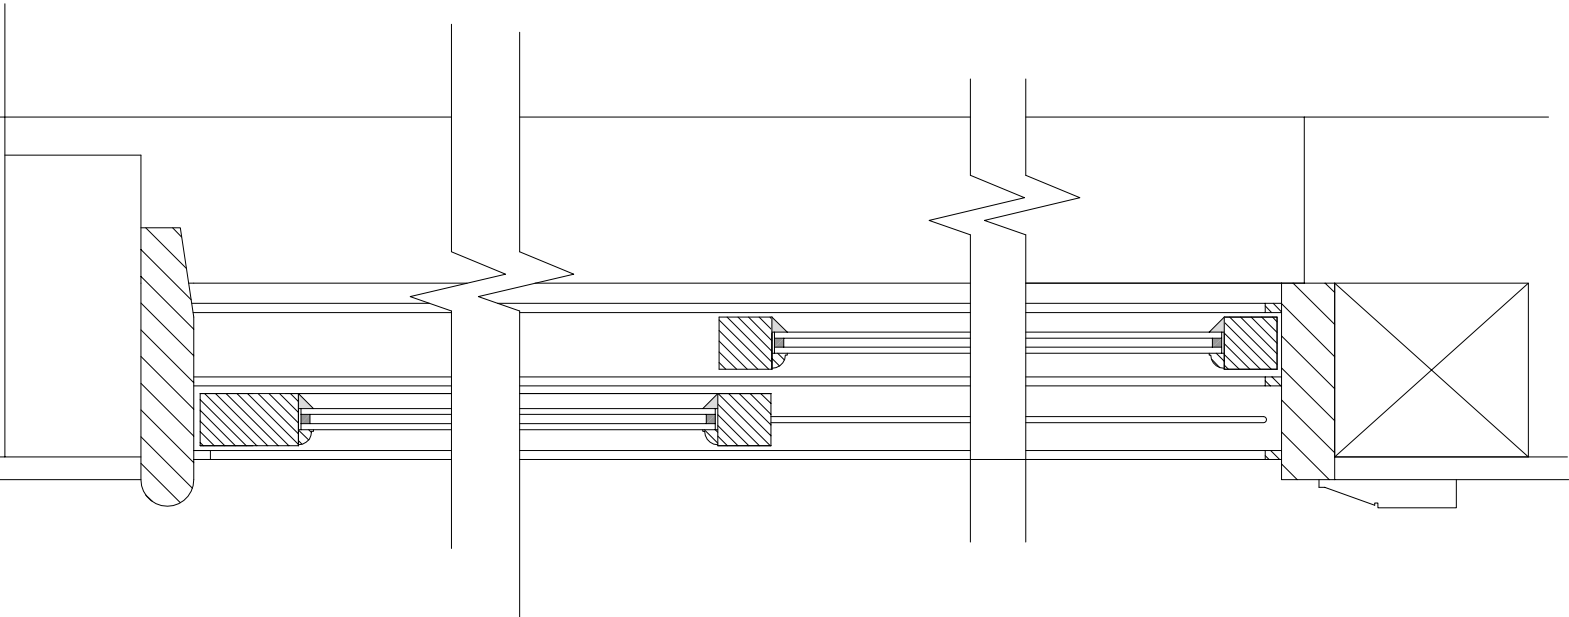

VERTICAL SECTION

TITLE PROPOSED DRAWINGS

ADDRESS 95 MALVERN ROAD
LONDON. NW6

CLIENT Mr. C. NORMAN

SCALE 1:5 & 1:10 @ A3 DATE MARCH 2019

DRAWING NO. 190328/27 REV.



URBAN REGEN LONDON Ltd.

Tel: 07970 647 449 Fax: 020 8963 9991 Email: urrlondon@aol.com