




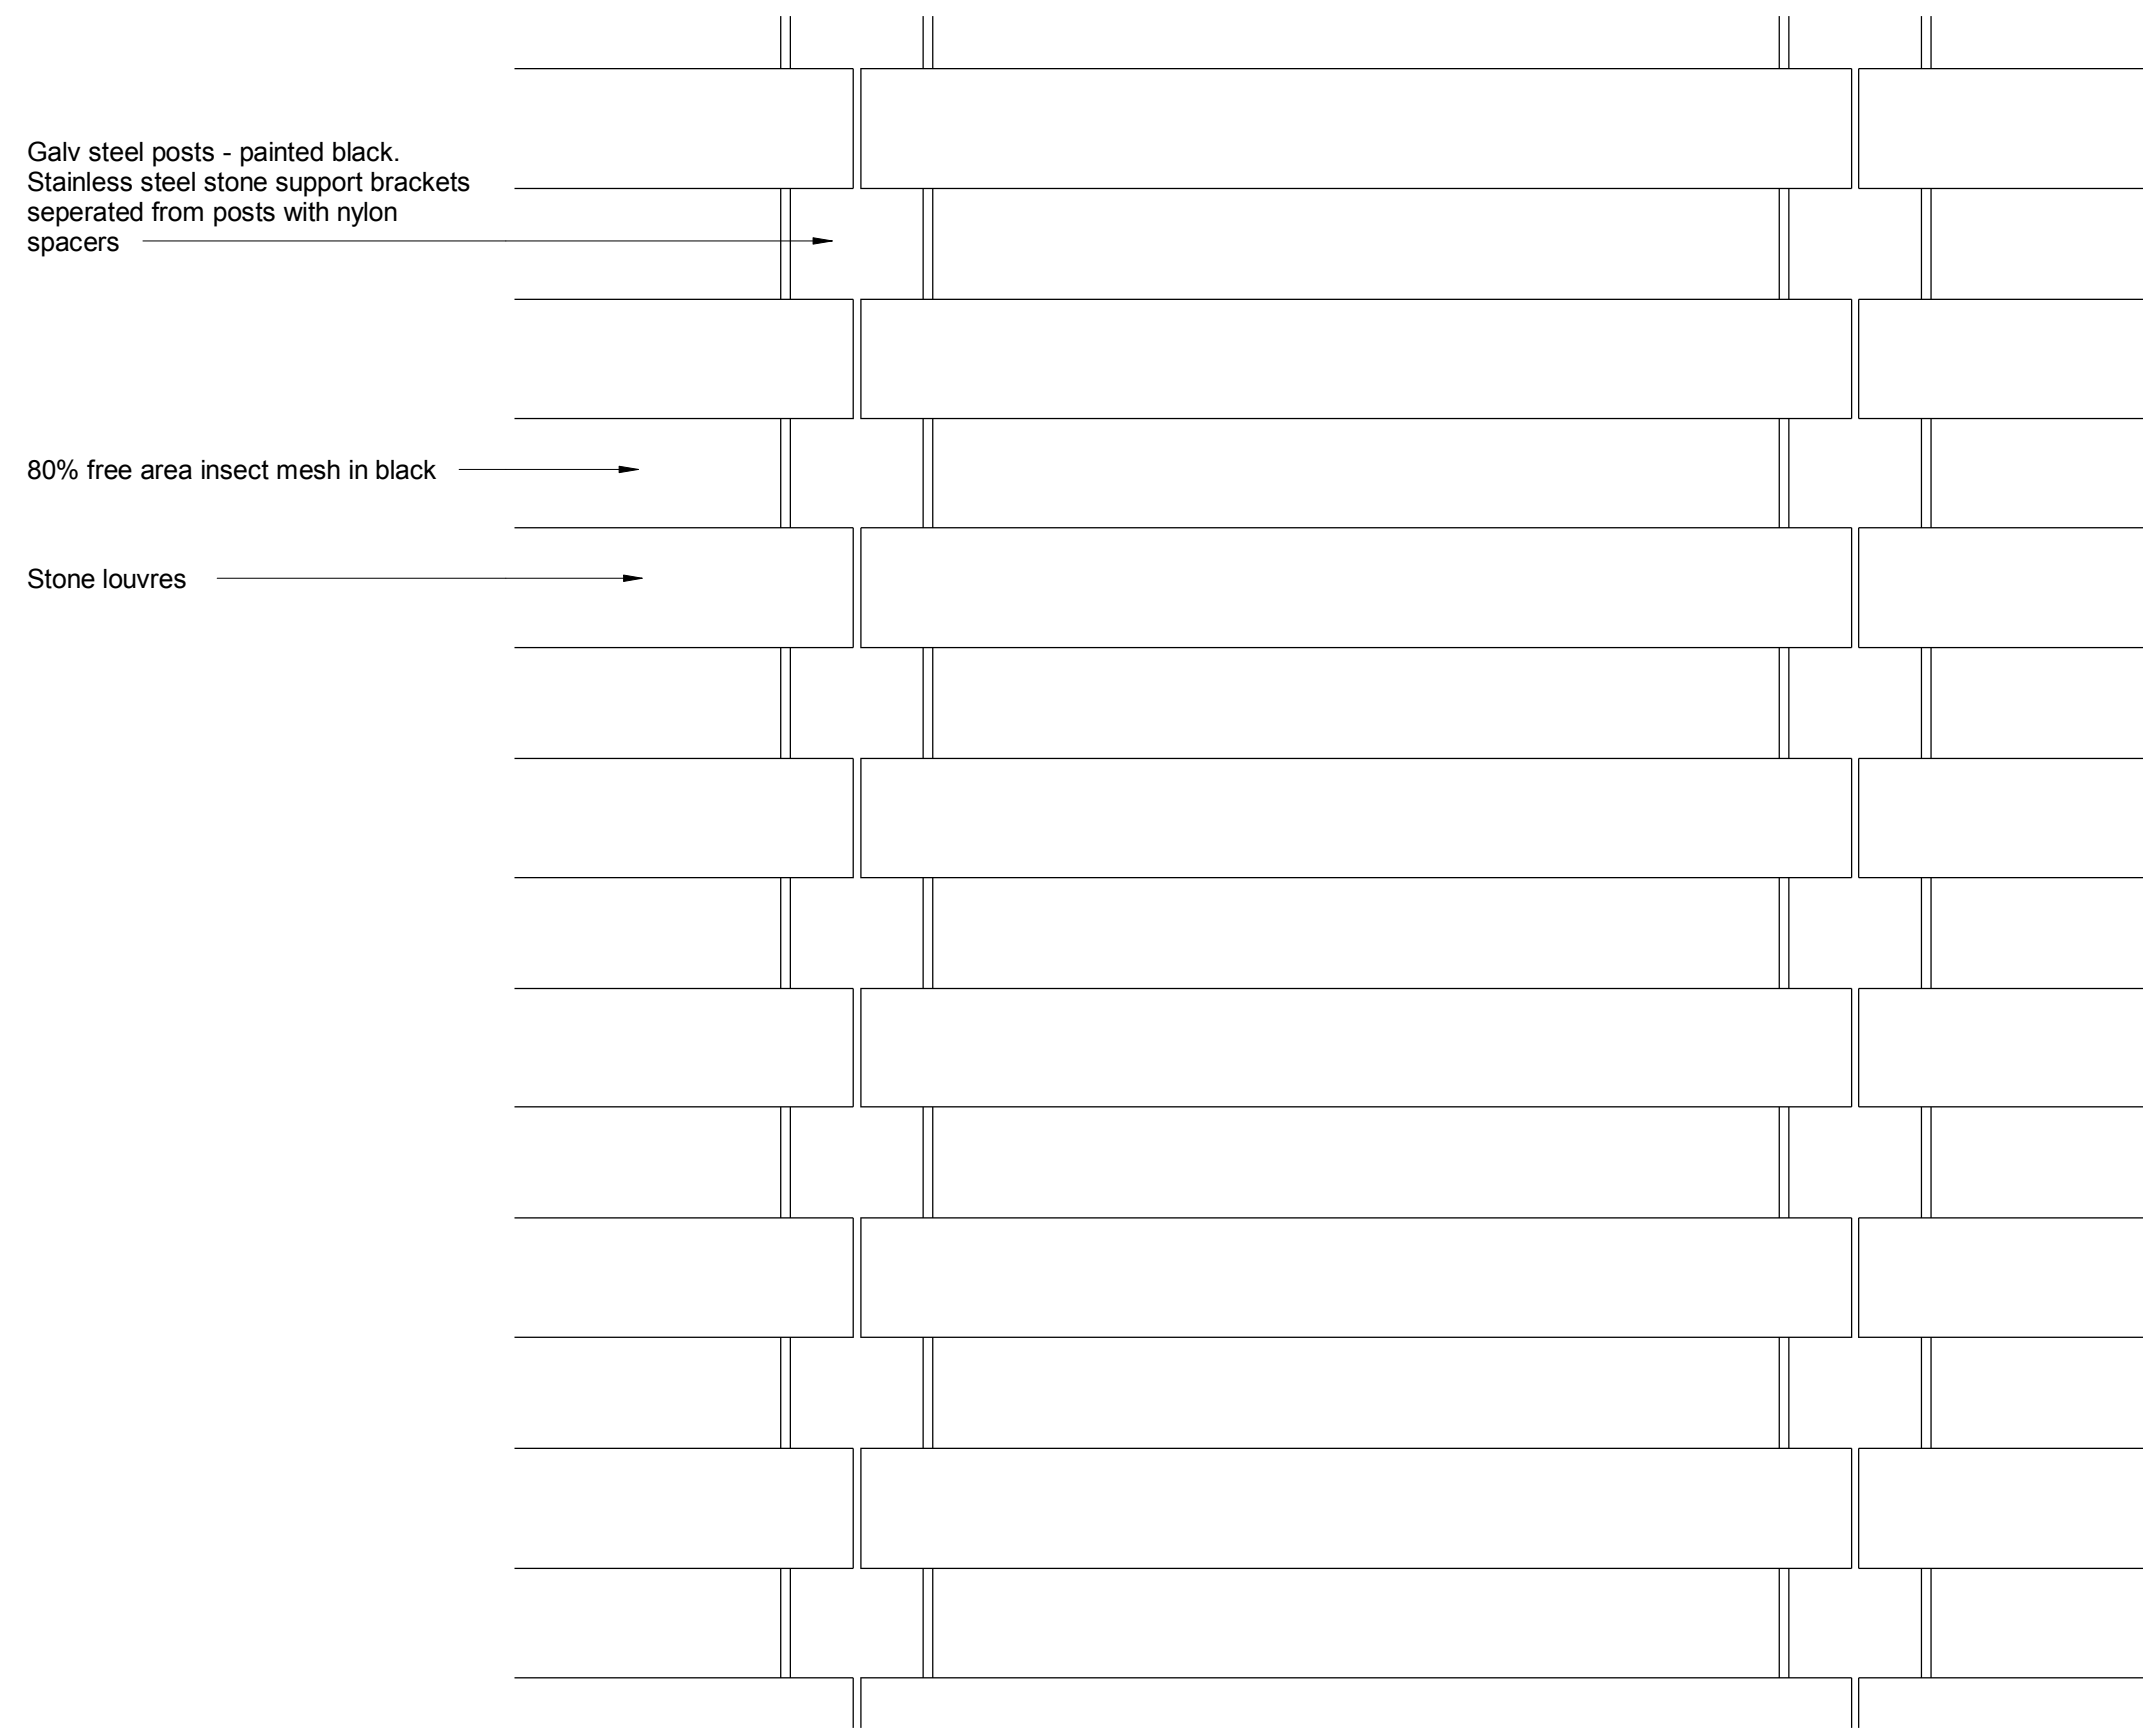


2 580-23 - Elevation
1:5

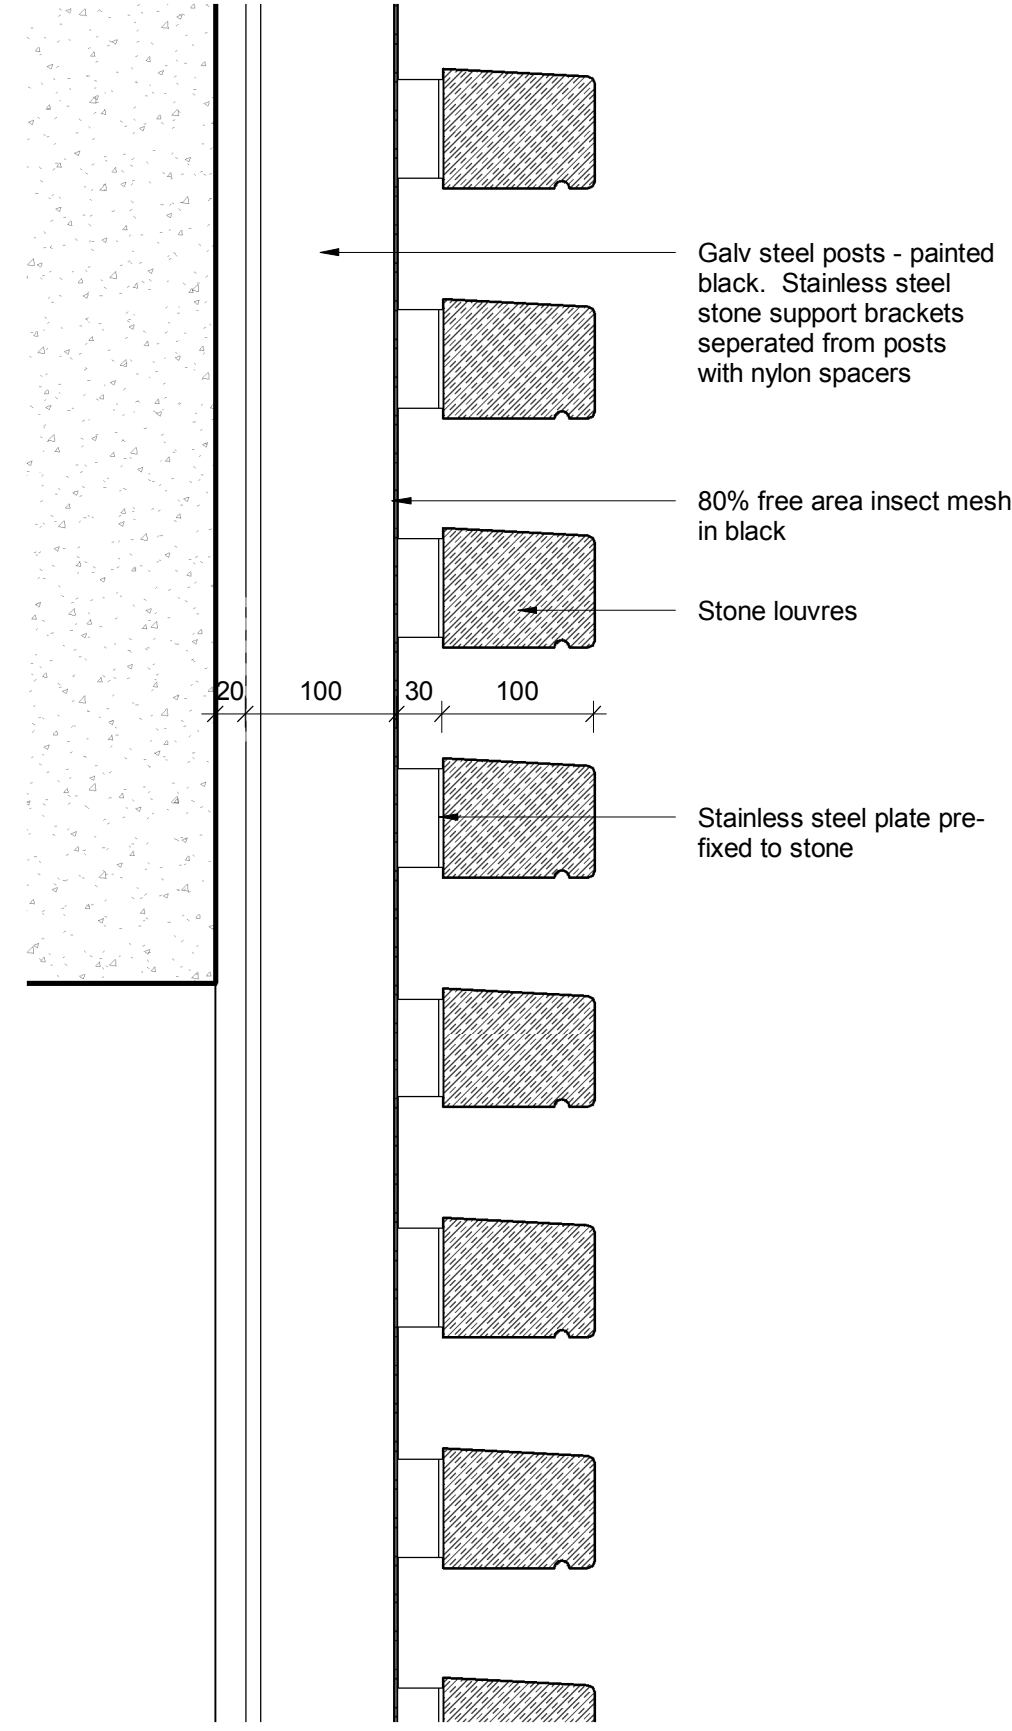


3 580-23 - Section
1:5

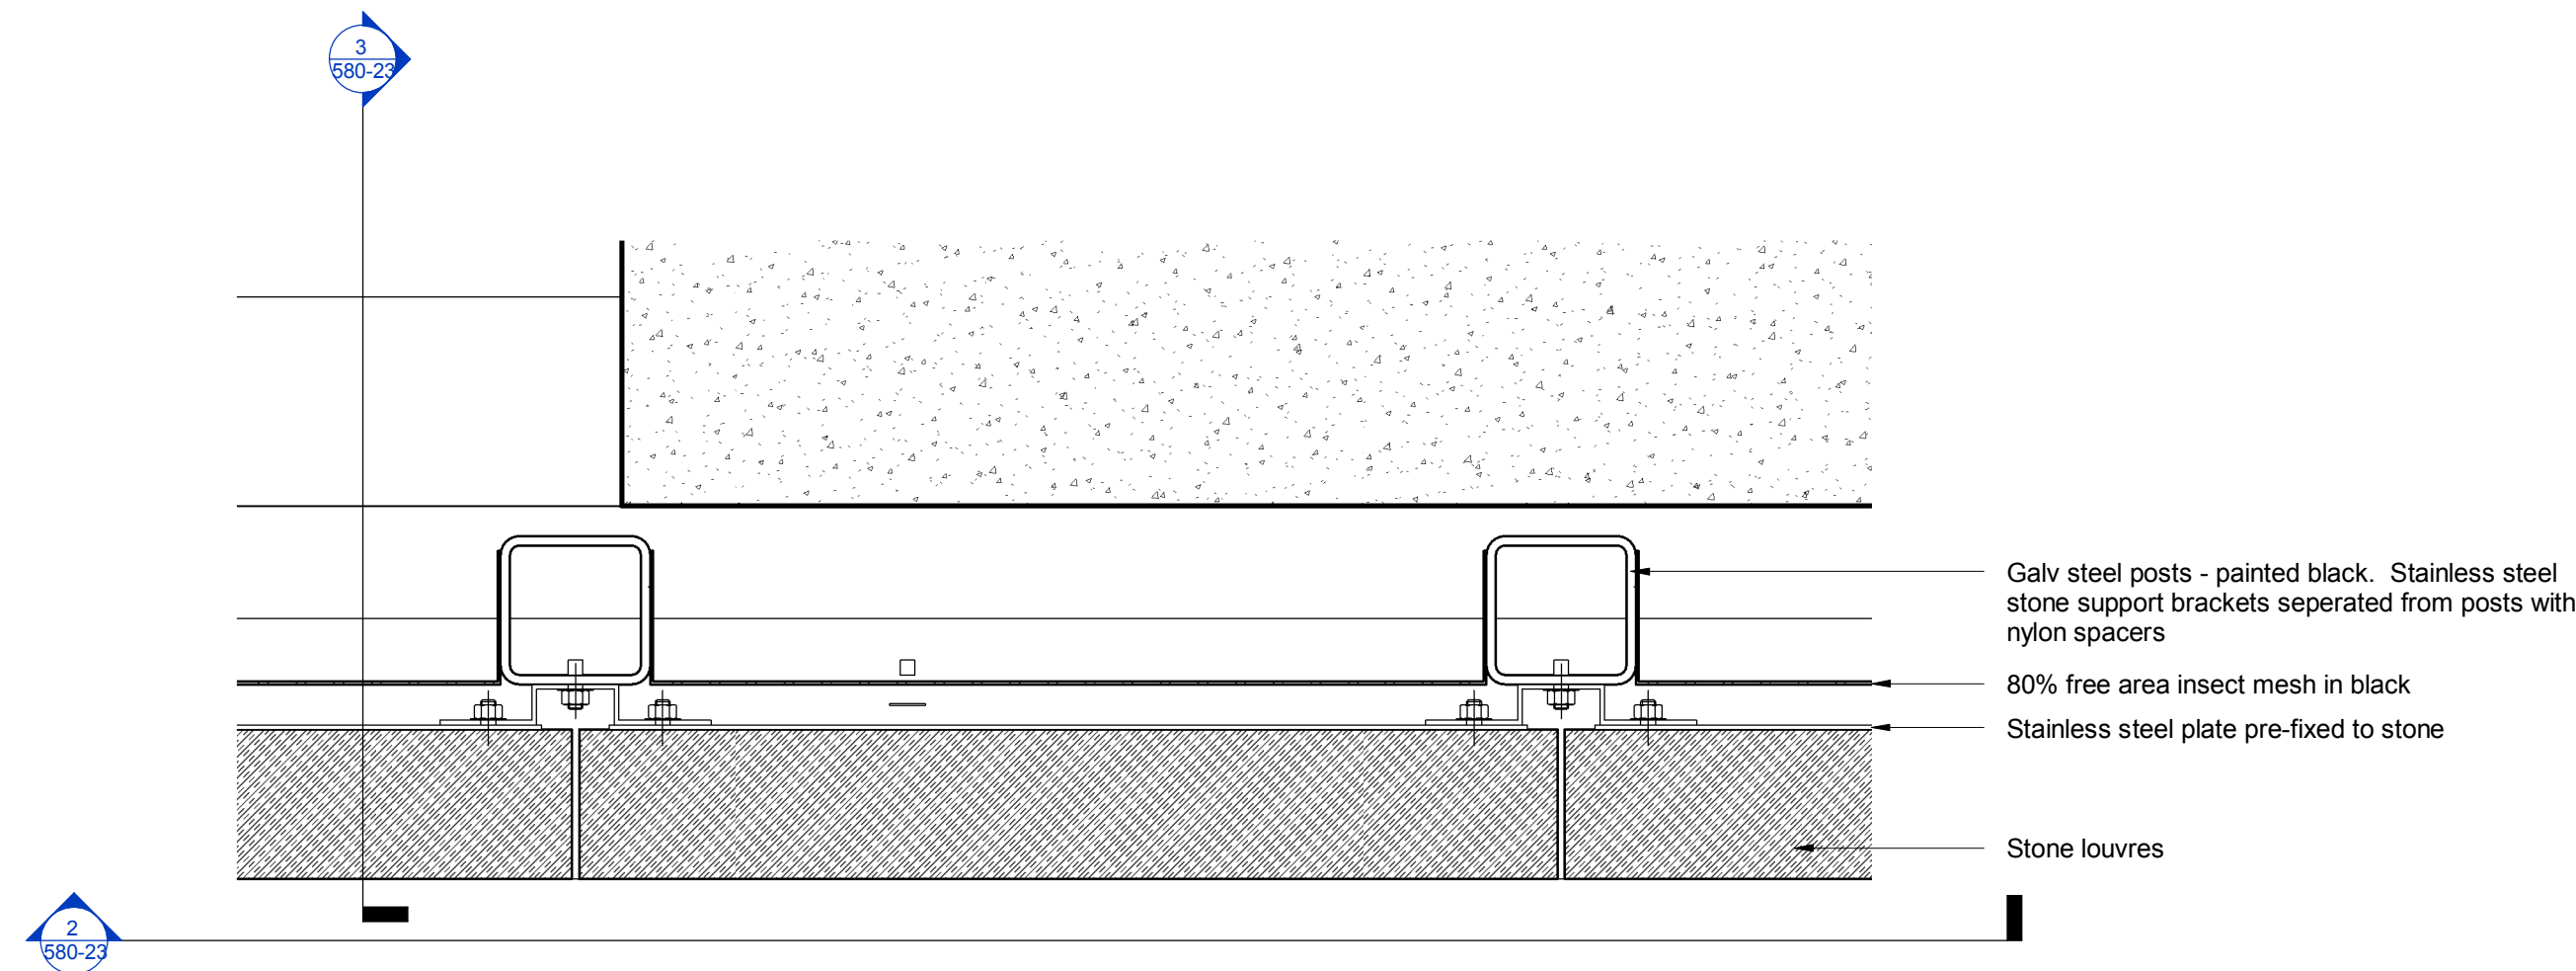

1 580-23 - Plan
1:5

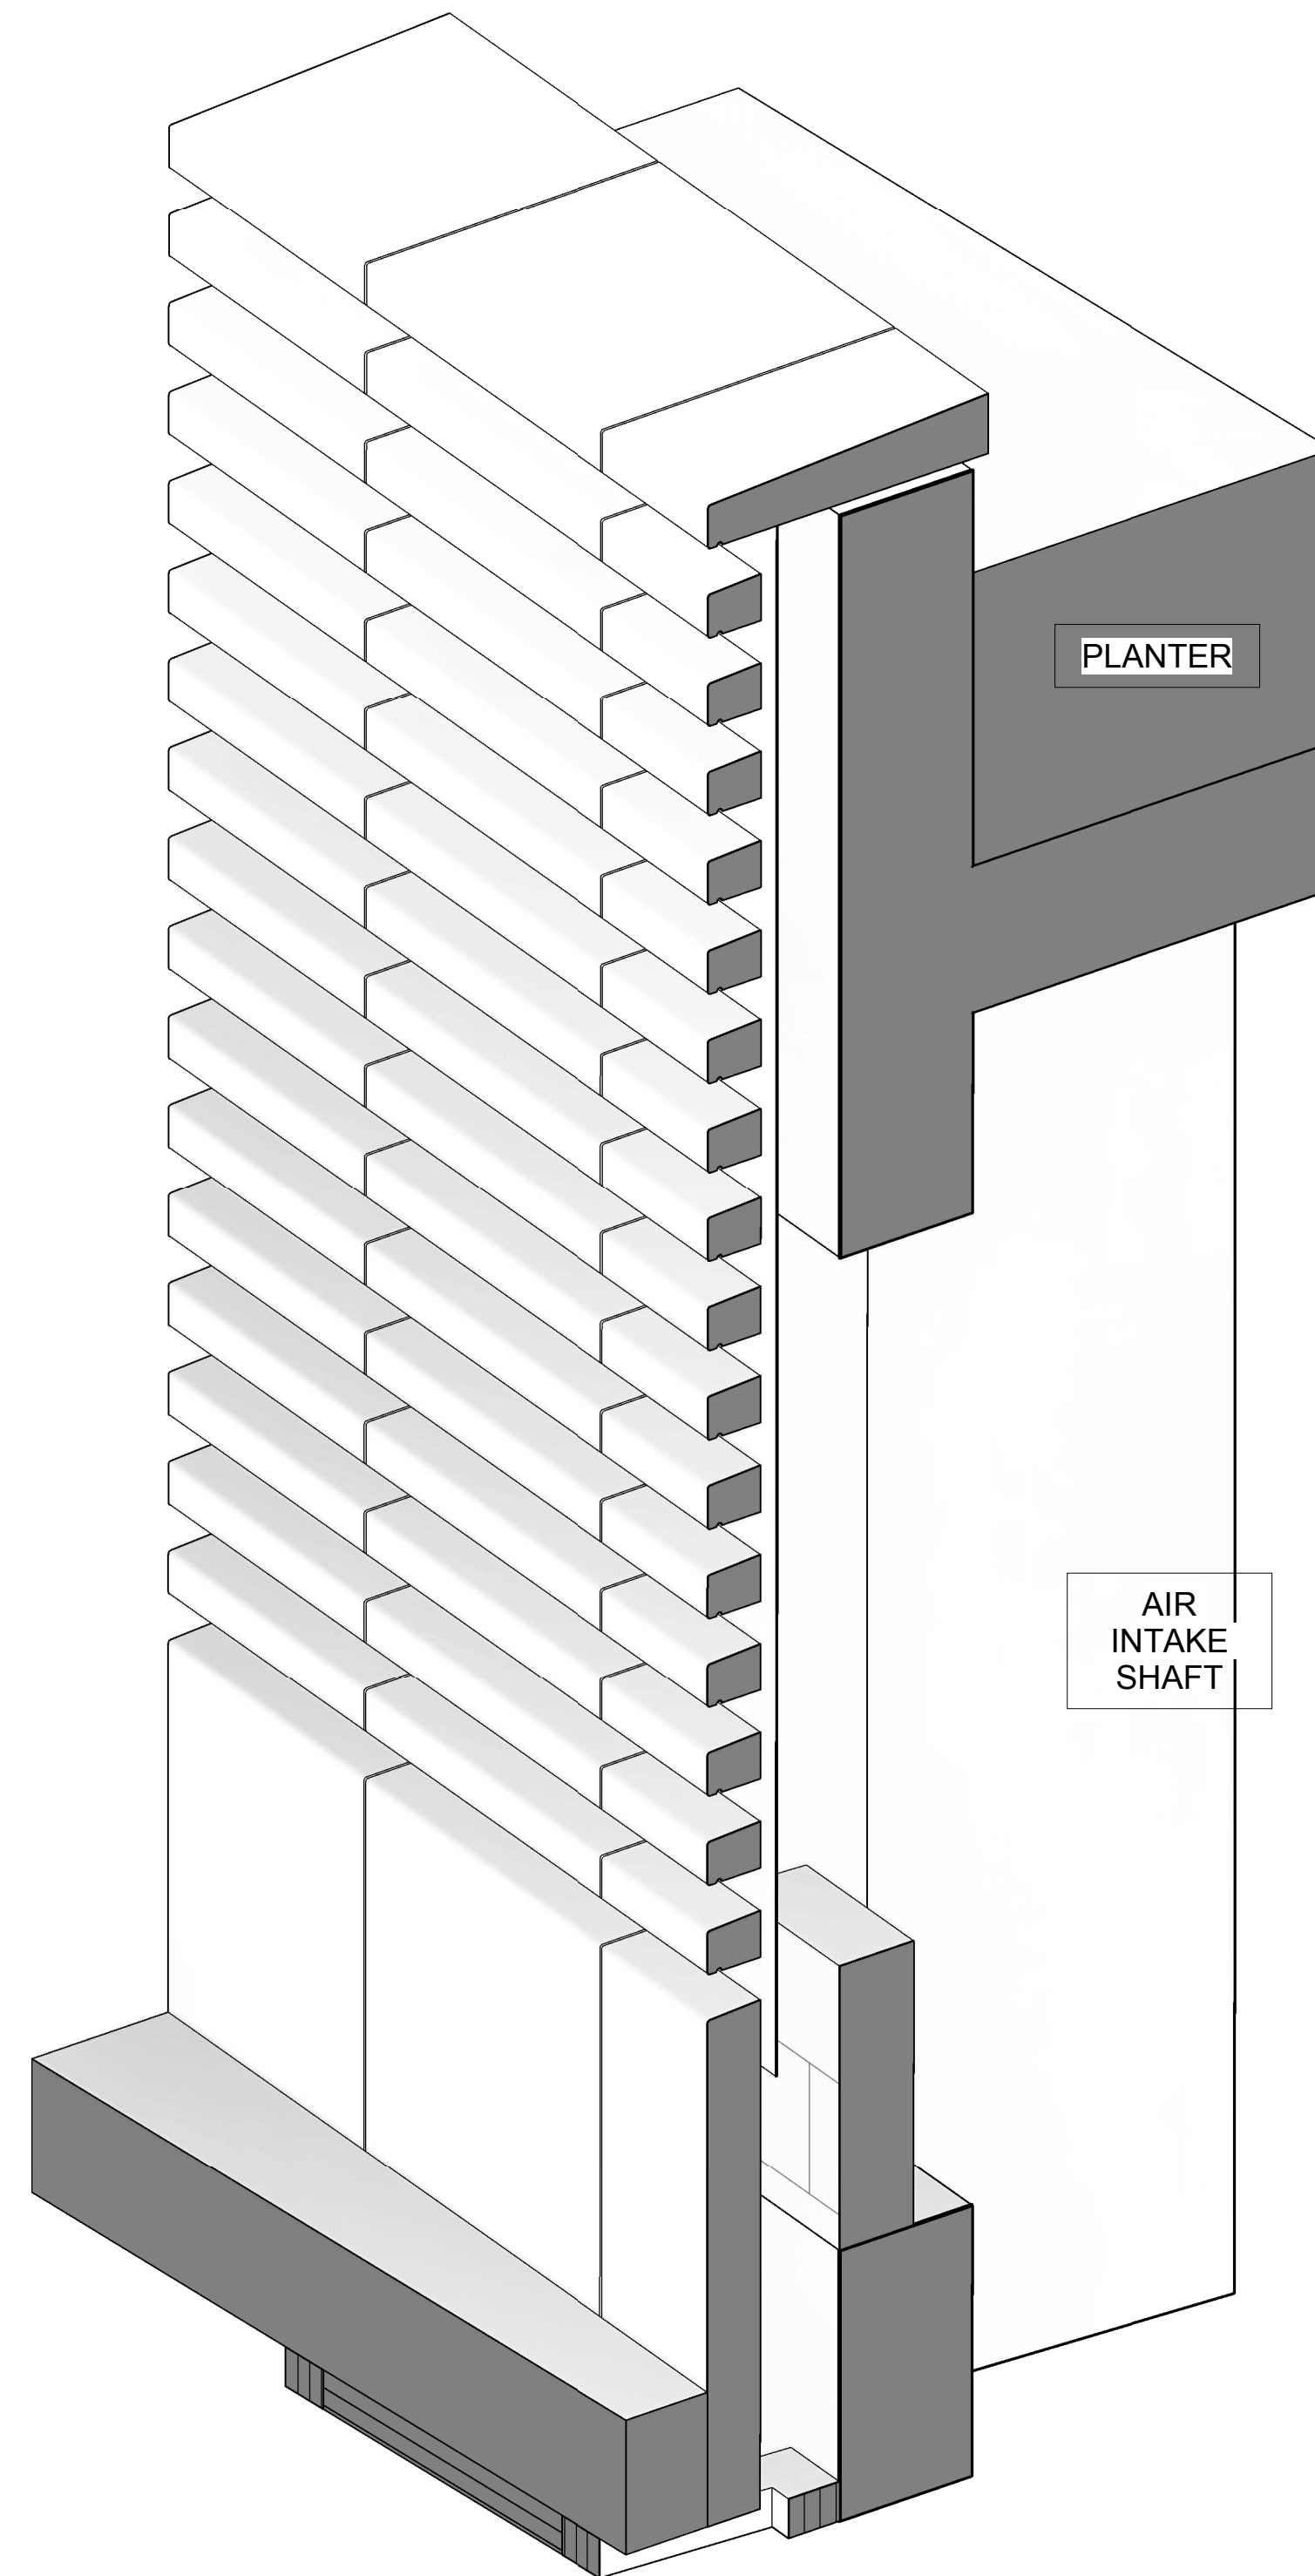

4 580-21 - Garden Airwell Axo

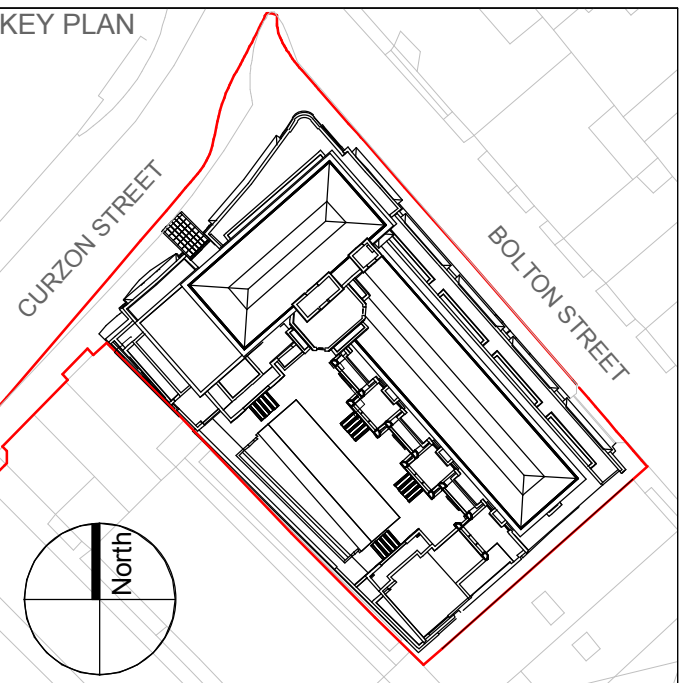

Do not scale dimensions. Dimensions govern.
All dimensions are in millimetres unless noted otherwise.
PLP Architecture shall be notified in writing of any discrepancies.
Planning approval required for design changes since consent was granted.

- Notes:**
- Nb1:** For all builders work and openings in the structure refer to structural engineers drawings.
 - Nb2:** The following areas are at Stage 3 level of design, further coordination will be required:
 - Internal fit-out to Apartments, FOH and Spa areas
 - Landscape design to the rear garden
 - External Architectural Lighting
 - Nb3:** The following areas are at Stage 2 level of design, further coordination will be required:
 - Street side External works as part of S106 obligations
 - Nb4:** The Restaurant spaces are designed as shell spaces
 - Nb5:** Refer to Stonework contractor drawings for detailed stone coursing set out

Rev	Date	Notes	Iss By	Ckd By
1	14/11/2018	Issued for Construction	AC	WM

Revisions

PLP/ARCHITECTURE

Ibex House
42-47 Minories
London EC3N 1DY
t: +44 (0) 20 3006 3900
f: +44 (0) 20 3006 3901
e: info@plparchitecture.com

www.plparchitecture.com

Clients Logo and Subconsultants

BROCKTON
CAPITAL

Project Name

60 Curzon Street

Status
CONSTRUCTION

Drawing Title
Garden wall details

Drawing Number
60CS-PLP-A-580-23

Scale	Sheet Size	Creation Date
1 : 5	A1	05/07/18
Revision	Drawn By	Checked By
1	AC	WM