



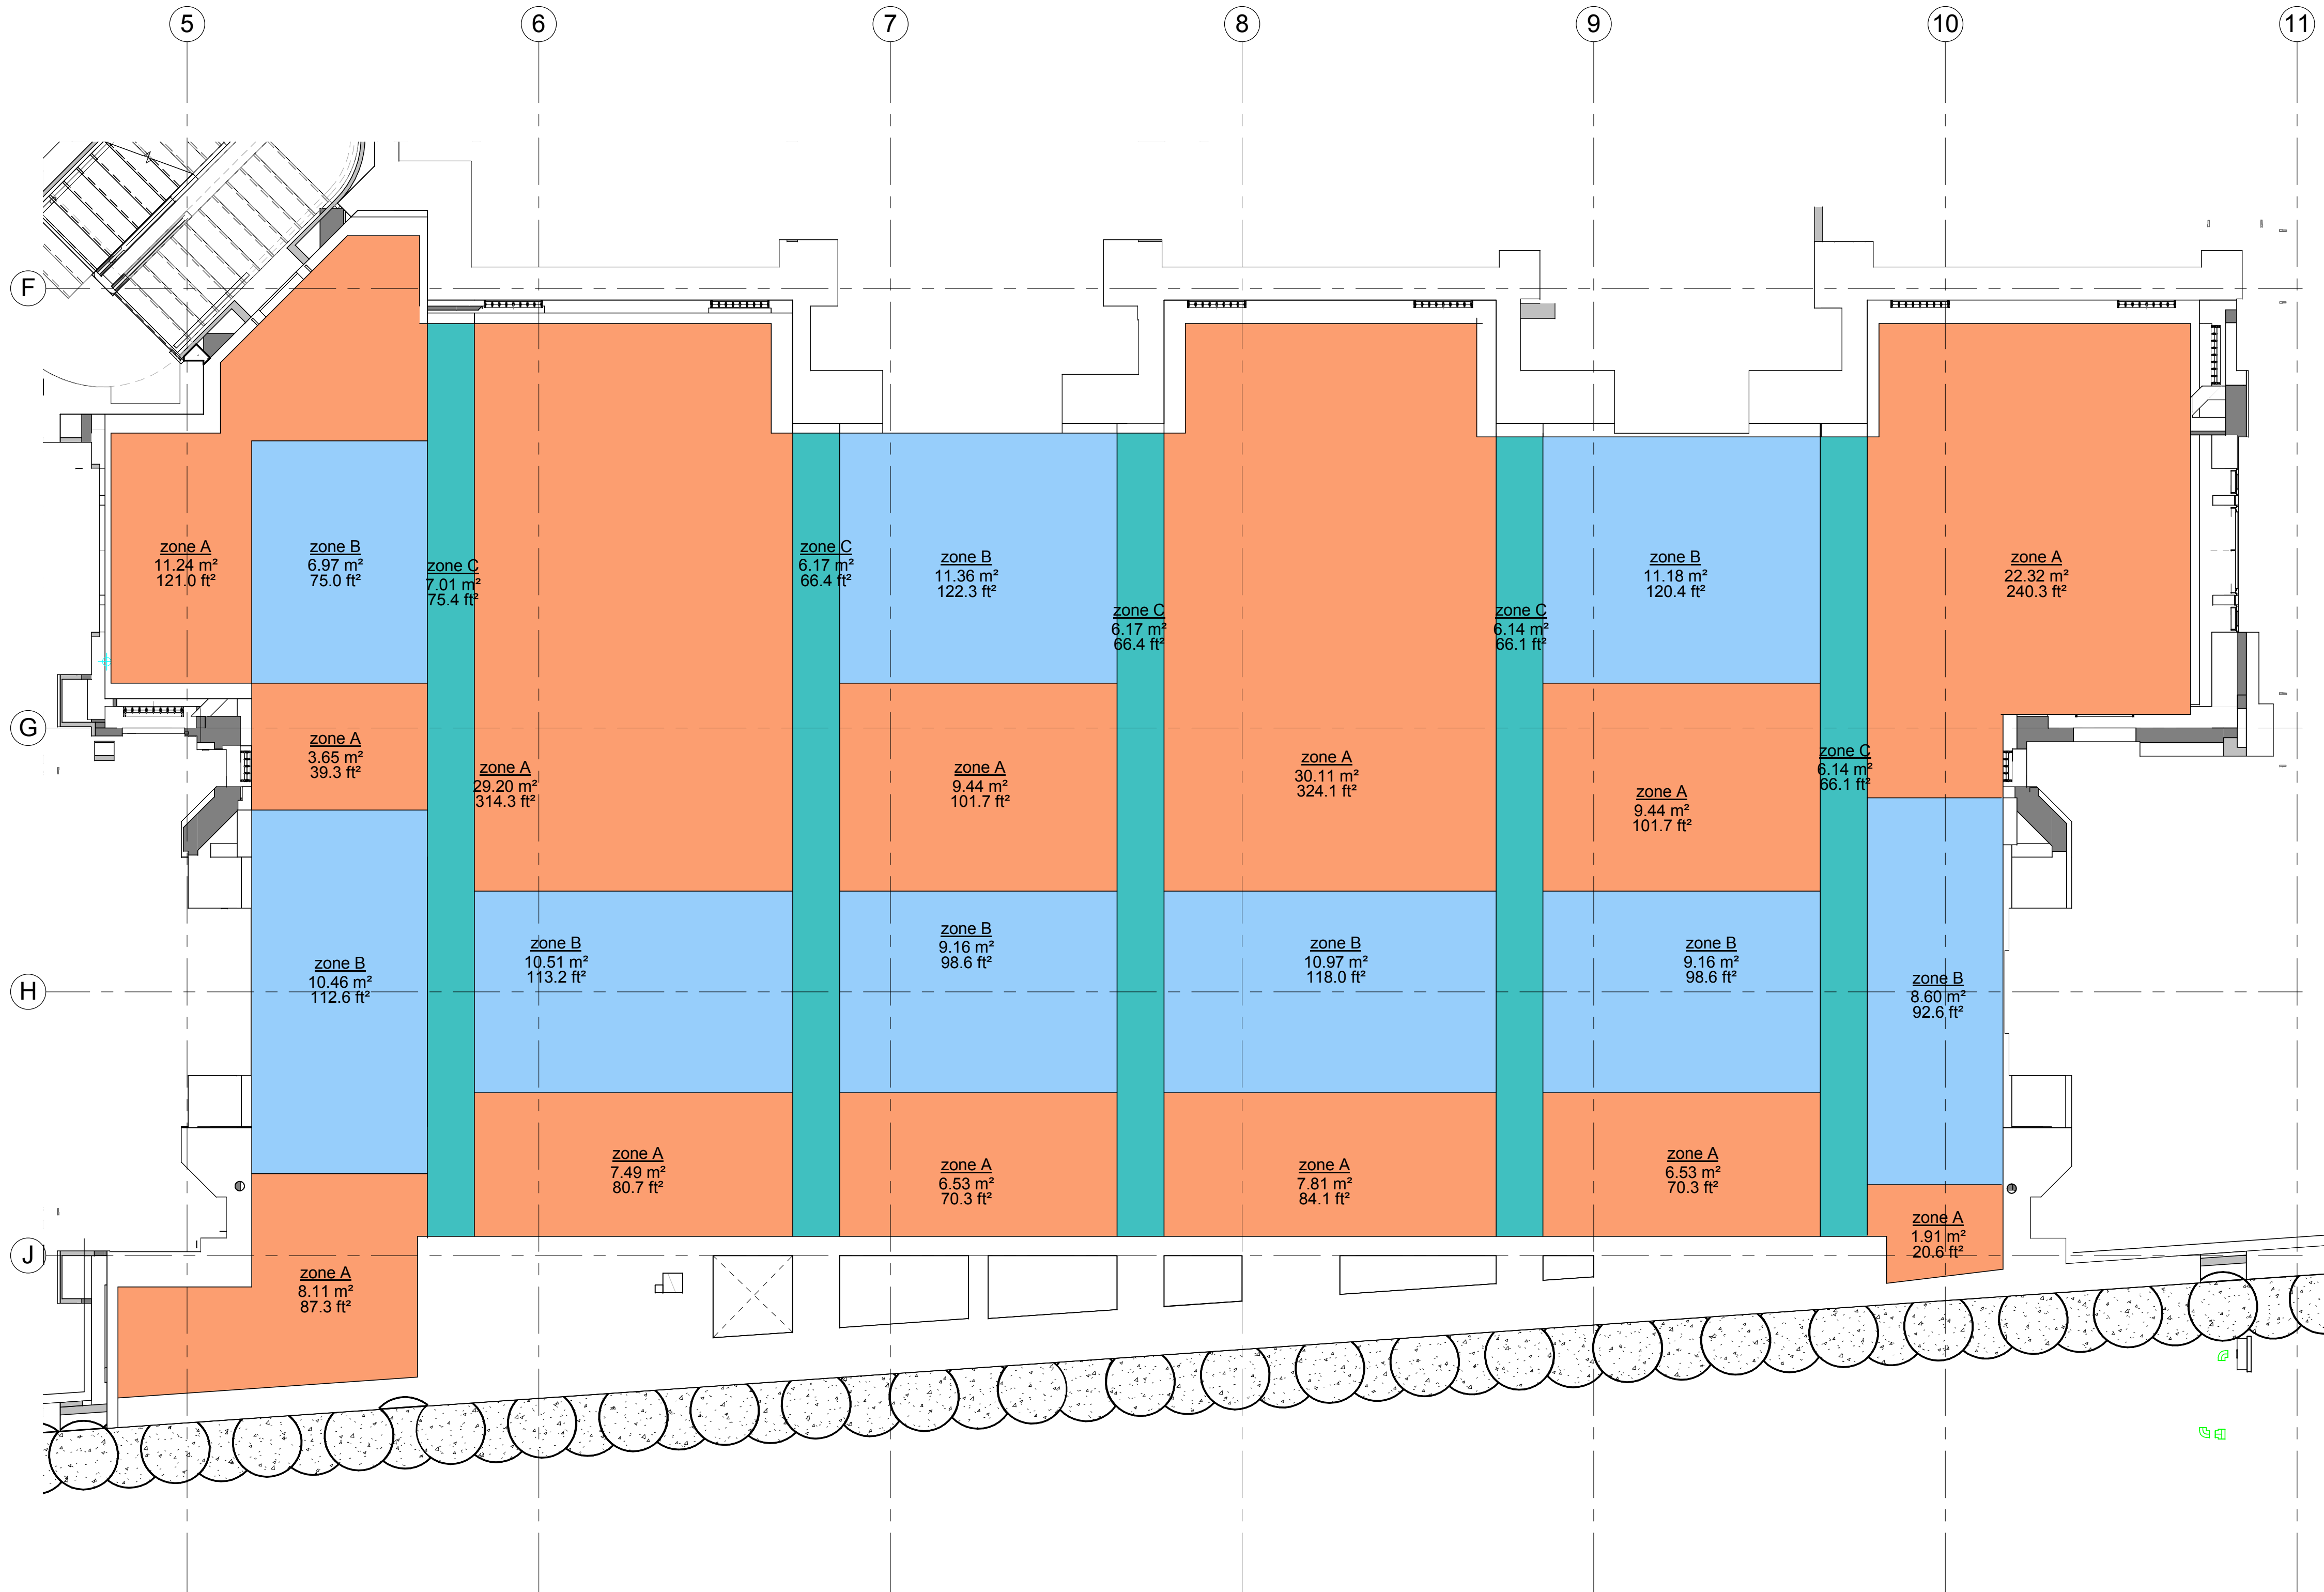

1 SK-226 - Garden insulation thickness
1 : 50

SK-226 Garden areas - ...	
Name	Area

zone A	22 m²
zone A	29 m²
zone A	9 m²
zone A	30 m²
zone A	9 m²
zone A	8 m²
zone A	7 m²
zone A	8 m²
zone A	2 m²
zone A	4 m²
zone A	11 m²
zone A	7 m²
zone A	7 m²
zone A: 13	154 m²
zone B	7 m²
zone B	11 m²
zone B	9 m²
zone B	11 m²
zone B	11 m²
zone B	9 m²
zone B	11 m²
zone B	9 m²
zone B	10 m²
zone B: 9	88 m²
zone C	6 m²
zone C	6 m²
zone C	6 m²
zone C	7 m²
zone C	6 m²
zone C: 5	32 m²
Grand total: 27	274 m²

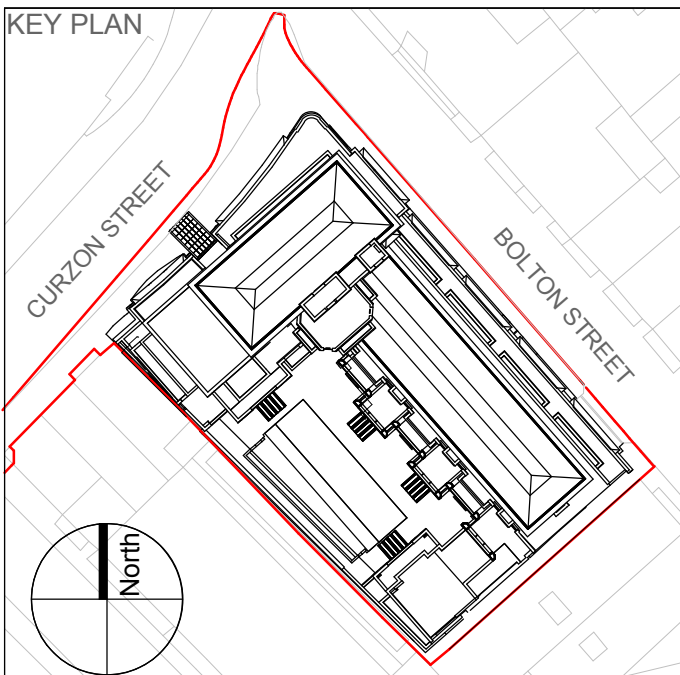

Do not scale dimensions. Dimensions govern.
All dimensions are in millimetres unless noted otherwise.
PLP Architecture shall be notified in writing of any discrepancies.
Planning approval required for design changes since consent was granted.

Notes:

Nb1. For all builders work and openings in the structure refer to structural engineers drawings.

Nb2. The following areas are at Stage 3 level of design, further coordination will be required:

- Internal fit-out to Apartments, FOH and Spa areas
- Landscape design to the rear garden
- External Architectural Lighting

Nb3. The following areas are at Stage 2 level of design, further coordination will be required:

- Street side External works as part of S106 obligations

Nb4. The Restaurant spaces are designed as shell spaces

Nb5. Refer to Stonework contractor drawings for detailed stone coursing set out

- Zone A - 130mm XPS
- Zone B - 130mm XPS & 350 EPS
- Zone C - 75mm XPS

1 28/02/2018 Change Control Items & RFI's - Issued for Construction MF WM

Revisions

PLP/ARCHITECTURE

Ibex House
42-47 Minories
London EC3N 1DY
t: +44 (0) 20 3006 3900
f: +44 (0) 20 3006 3901
e: info@plparchitecture.com

www.plparchitecture.com

Clients Logo and Subconsultants

BROCKTON
CAPITAL

Project Name

60 Curzon Street

Status
CONSTRUCTION

Drawing Title
Garden insulation thickness - Plan

Drawing Number
60CS-PLP-A-580-26

Scale	Sheet Size	Creation Date
As indicated	A1	11/28/17
Revision	Drawn By	Checked By
1	AC	WM