
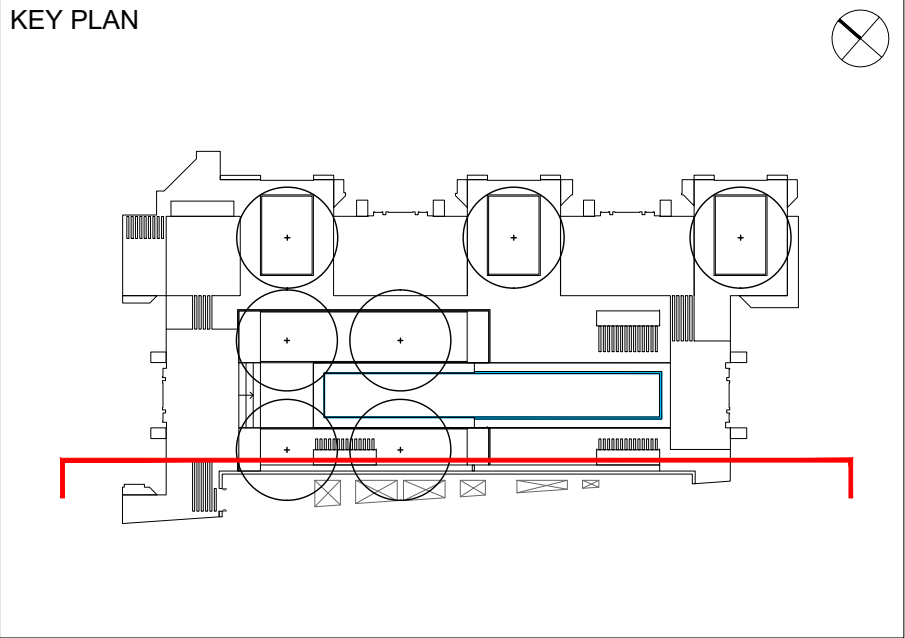


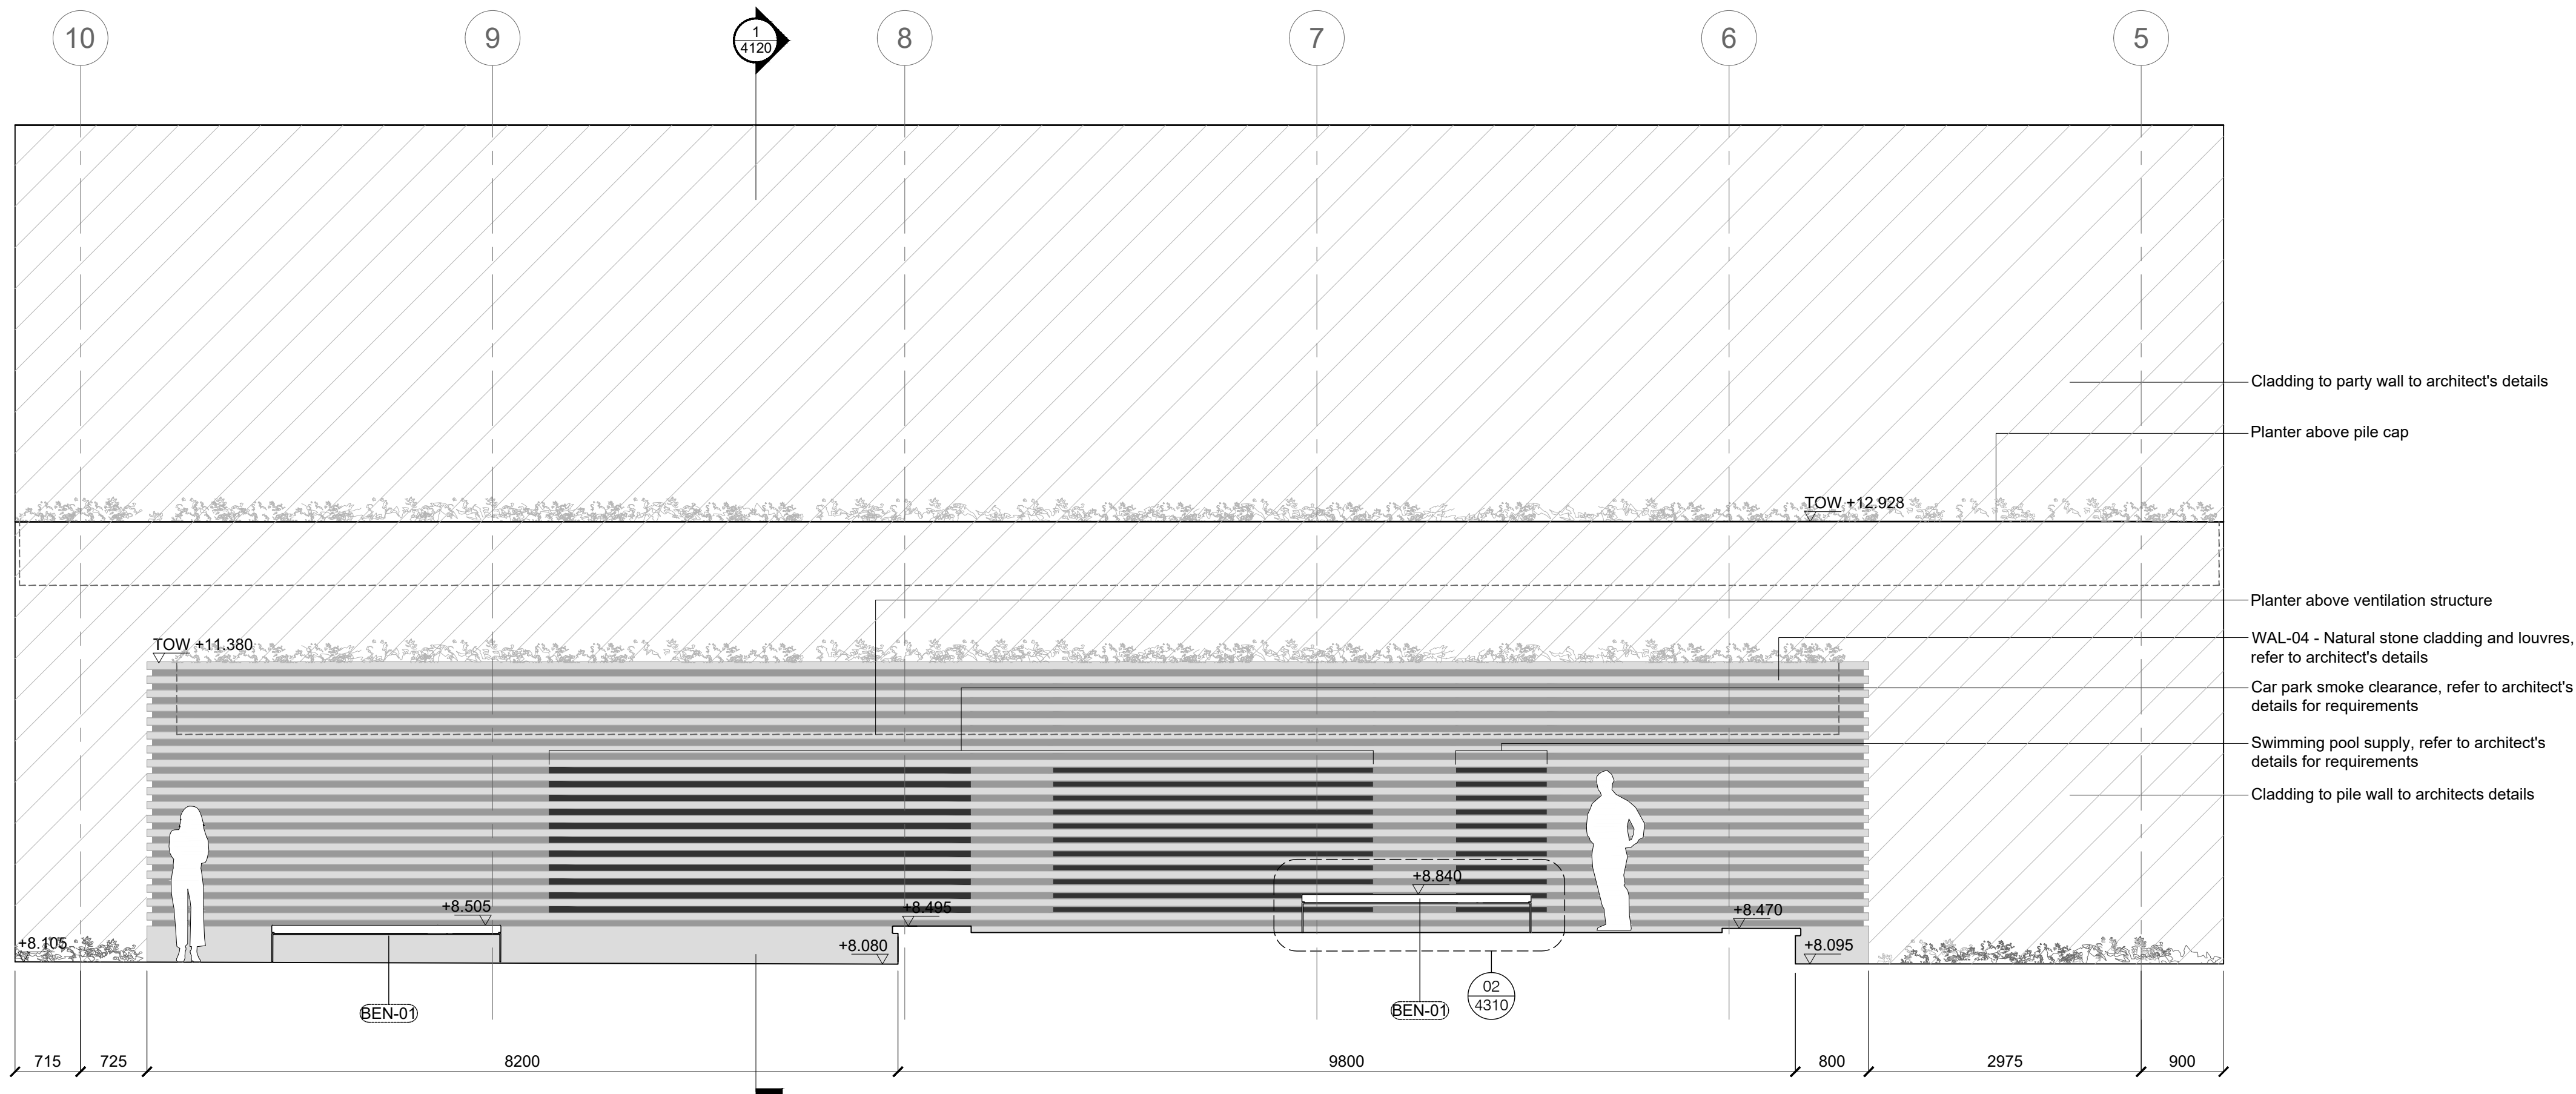

- NOTE
- Refer to PLP Architecture drawings for details of louvre wall and garden wall cladding
  - Fall protection anchor points to be incorporated to assist maintenance of planters, refer to architect's details

|          |            |     |      |      |             |
|----------|------------|-----|------|------|-------------|
|          |            |     |      |      |             |
|          |            |     |      |      |             |
|          |            |     |      |      |             |
| P03      | 07/03/2019 | LMN | DOS  | NP   | FOR TENDER  |
| P02      | 27/07/2018 | LMN | DOS  | NP   | STAGE 4     |
| P01      | 02/03/2018 | LMN | DOS  | NP   | STAGE 3     |
| P00      | 19/05/2017 | TC  | DOS  | NP   | STAGE 3     |
| revision | date       | by  | chkd | appr | description |

Gustafson  
Porter +  
Bowman

1 Cobham Mews  
Agar Grove  
London NW1 9SB  
t: +44 (0) 207 284 8850  
e: enquiries@gp-b.com  
www.gp-b.com

|                               |                                       |
|-------------------------------|---------------------------------------|
| architect<br>PLP ARCHITECTURE | engineer<br>WSP<br>HOARE LEA          |
| project manager<br>GVA SLW    | quantity surveyor<br>CAST CONSULTANCY |

client  
60 Curzon Street Developments Limited  
Brockton Capital

project  
312 CZN - 60 Curzon Street

drawing title  
Vent Wall Elevation

drawing number  
GPB-312-E-2010

|                     |            |          |
|---------------------|------------|----------|
| scale               | date       | revision |
| 1:50@A1<br>1:100@A3 | 19/05/2017 | P03      |

|                 |                   |                   |
|-----------------|-------------------|-------------------|
| drawn by<br>LMN | checked by<br>DOS | approved by<br>NP |
|-----------------|-------------------|-------------------|

Do not scale off this drawing. Use figured dimensions only. All dimensions and levels to be checked and confirmed on site. Gustafson Porter + Bowman does not accept responsibility for accuracy of survey information. Do not build from this drawing. This drawing is copyright.